TÊN DỰ ÁN/ PROJECT NAME:

XÂY DỰNG NHÀ Ở TẠI LÔ ĐẤT NO-22

ĐỊA ĐIỂM XÂY DỰNG / PROJECT ADDRESS:

LÔ ĐẤT NO-22, PHƯỜNG BỒ ĐỀ, HÀ NỘI

HỒ SƠ THIẾT KẾ CƠ SỞ

SCHEMATIC DESIGN PHASE

CHỦ ĐẦU TƯ / OWNER:

CÔNG TY CỔ PHẦN THƯƠNG MẠI DƯƠNG PHÚC THẮNG

DUONG PHUC THANG TRADING JOINT STOCK COMPANY

TƯ VẤN THIẾT KẾ / CONSULTANT:

CÔNG TY CỔ PHẦN INNO

INNO.,JSC

BỘ MÔN: KIẾN TRÚC
DISCIPLINE: ARCHITECTURE

PHIÊN BẢN / REVISION: 0
NGÀY PHÁT HÀNH / ISSUED DATE: .../.../2026

© 2025 - INNO.jsc

TÊN DỰ ÁN/ PROJECT NAME:

XÂY DỰNG NHÀ Ở TẠI LÔ ĐẤT NO-22

ĐỊA ĐIỂM XÂY DỰNG / PROJECT ADDRESS:

LÔ ĐẤT NO-22, PHƯỜNG BỒ ĐỀ, HÀ NỘI

HỒ SƠ THIẾT KẾ CƠ SỞ

SCHEMATIC DESIGN PHASE

CHỦ ĐẦU TƯ / OWNER: **CÔNG TY CỔ PHẦN THƯƠNG MẠI DƯƠNG PHÚC THẮNG** DUONG PHUC THANG TRADING JOINT STOCK COMPANY GIÁM ĐỐC	TƯ VẤN THIẾT KẾ / CONSULTANT: **CÔNG TY CỔ PHẦN INNO** TỔNG GIÁM ĐỐC	ĐƠN VỊ THẨM TRA / APPRAISAL CONSULTANT : **TRUNG TÂM TƯ VẤN XD CÔNG NGHIỆP VÀ HẠ TẦNG**

BỘ MÔN: KIẾN TRÚC
DISCIPLINE: ARCHITECTURE

PHIÊN BẢN / REVISION: 0
NGÀY PHÁT HÀNH / ISSUED DATE: .../.../2026

© 2025 - INNO Jsc

DANH MỤC BẢN VẼ

STT	KÝ HIỆU	TÊN BẢN VẼ	PHIÊN BẢN
1. PHẦN CHUNG			
1	A-00.001	DANH MỤC BẢN VẼ	0
2	A-00.002	GHI CHÚ KÝ HIỆU	0
3	A-00.003	GHI CHÚ CẤU TẠO	0
2.TỔNG THỂ			
4	A-00.101	MẶT BẰNG TỔNG THỂ	0
5	A-00.102	MẶT BẰNG ĐỊNH VỊ TẦNG 1	0
3.HẦM			
6	A.0-01.101	MẶT BẰNG TẦNG HẦM B1	0
7	A.0-01.102	MẶT BẰNG TẦNG HẦM B2	0
4.TOWER1			
8	A.1-01.101	MẶT BẰNG TẦNG 1	0
9	A.1-01.102	MẶT BẰNG TẦNG 2	0
10	A.1-01.103	MẶT BẰNG TẦNG 3-5	0
11	A.1-01.104	MẶT BẰNG TẦNG 4-6	0
12	A.1-01.105	MẶT BẰNG TẦNG 7	0
13	A.1-01.106	MẶT BẰNG TẦNG TUM	0
14	A.1-01.107	MẶT BẰNG MÁI	0
5.TOWER2			
15	A.2-01.101	MẶT BẰNG TẦNG 1	0
16	A.2-01.102	MẶT BẰNG TẦNG 2	0
17	A.2-01.103	MẶT BẰNG TẦNG 3-5	0
18	A.2-01.104	MẶT BẰNG TẦNG 4	0
19	A.2-01.105	MẶT BẰNG TẦNG 6	0
20	A.2-01.106	MẶT BẰNG TẦNG 7-8	0
21	A.2-01.107	MẶT BẰNG TẦNG 9	0
22	A.2-01.108	MẶT BẰNG TẦNG TUM	0
23	A.2-01.109	MẶT BẰNG MÁI	0
6.TOWER3			
25	A.3-01.101	MẶT BẰNG TẦNG 1	0
26	A.3-01.102	MẶT BẰNG TẦNG 2	0
27	A.3-01.103	MẶT BẰNG TẦNG 4-6-8-10	0
28	A.3-01.104	MẶT BẰNG TẦNG 3-5-7-9	0
29	A.3-01.105	MẶT BẰNG TẦNG 11	0
30	A.3-01.106	MẶT BẰNG TẦNG TUM	0
31	A.3-01.107	MẶT BẰNG MÁI	0
7. MẶT ĐỨNG			
33	A-02.101	MẶT ĐỨNG 1	0
34	A-02.102	MẶT ĐỨNG 2	0
35	A-02.103	MẶT ĐỨNG 3	0
36	A-02.104	MẶT ĐỨNG 4	0
8. MẶT CẮT			
37	A-03.101	MẶT CẮT A-A	0
38	A-03.102	MẶT CẮT B-B	0

PHIÊN BẢN	NỘI DUNG ĐIỀU CHỈNH	NGÀY NỘP

GHI CHÚ:

- CỐT +0.000 LẤY TẠI SÀN HOÀN THIỆN TẦNG 1 CÔNG TRÌNH TƯƠNG ĐƯƠNG COTE TUYỆT ĐỐI +7.900 (HỆ TỌA ĐỘ VN-2000)

- TÒA 1 CHIỀU CAO CÔNG TRÌNH TÍNH TỪ:
  + COTE HOÀN THIỆN +0.000: 43M
  + COTE NỀN TỰ NHIÊN THẤP NHẤT -1.000: 44M
- TÒA 2 CHIỀU CAO CÔNG TRÌNH TÍNH TỪ:
  + COTE HOÀN THIỆN +0.000: 50M
  + COTE NỀN TỰ NHIÊN THẤP NHẤT -1.000: 51M
- TÒA 3 CHIỀU CAO CÔNG TRÌNH TÍNH TỪ:
  + COTE HOÀN THIỆN +0.000: 59M
  + COTE NỀN TỰ NHIÊN THẤP NHẤT -1.000: 60M

- KHU VỰC TMDV BÀN GIAO THÔ, VỆ SINH KHÔNG XÂY, CHỈ BỐ TRÍ LAYOUT ĐỊNH HƯỚNG ĐẶT CÁC ĐẦU CHỜ.

- TỶ LỆ SỬ DỤNG VẬT LIỆU XANH KHÔNG NUNG ĐÁP ỨNG TỚI 90% KHỐI LƯỢNG GẠCH TRONG CÔNG TRÌNH

- TRONG PHÒNG RÁC KHÔNG BỐ TRÍ CÁC CHẤT, VẬT LIỆU CÓ KHẢ NĂNG GÂY CHÁY NỔ

- TƯỜNG NGĂN CHÁY, VÁCH NGĂN CHÁY TRONG CÁC GIAN PHÒNG ĐƯỢC NGĂN CHIA ĐẾN TRẦN BÊ TÔNG.

- VẬT LIỆU HOÀN THIỆN TRẦN, TƯỜNG, SÀN TRÊN CÁC ĐƯỜNG THOÁT NẠN, TRONG SẢNH THANG MÁY, SẢNH CHUNG, TẦNG KỸ THUẬT LÀ VẬT LIỆU KHÔNG CHÁY ĐẠT CV0

- TRONG CÁC KHÔNG GIAN TRẦN TREO KHÔNG BỐ TRÍ CÁC KÊNH, ĐƯỜNG ỐNG DẪN VẬN CHUYỂN CÁC CHẤT CHÁY DẠNG KHÍ, HỖN HỢP KHÍ, CHẤT LỎNG VÀ VẬT LIỆU CHÁY.

- TRONG CÔNG TRÌNH KHÔNG BỐ TRÍ TRẦN TREO CHO CÁC GIAN PHÒNG HẠNG A VÀ HẠNG B

- KHÔNG CÓ KÊNH, GIẾNG, ĐƯỜNG ỐNG ĐI QUA TƯỜNG NGĂN CHÁY LOẠI 1

CHỦ ĐẦU TƯ / OWNER:
CÔNG TY CỔ PHẦN THƯƠNG MẠI DƯƠNG PHÚC THẮNG
DUONG PHUC THANG TRADING JOINT STOCK COMPANY

ĐỊA CHỈ / ADDRESS:
Tầng 16, Tòa OSI Tower, Khu tây Hồ Tây, Phường Xuân Đỉnh, Thành phố Hà Nội, Việt Nam.
Hotline : 0243 2077 272

TƯ VẤN KIẾN TRÚC CHÍNH / MAIN ARCHITECTURAL CONSULTANT:
CÔNG TY TNHH KIẾN TRÚC DP VIỆT NAM
DP ARCHITECTS VIETNAM CO.,LTD.

ĐỊA CHỈ / ADDRESS:
Tầng 4, số 82 Võ Văn Tần, Phường Xuân Hòa, TP.Hồ Chí Minh
Hotline : 0283 5357 507
Fax: 0283 5357 517
Email : dparchitects@dpa.com.sg

TƯ VẤN THIẾT KẾ / CONSULTANT:
CÔNG TY CỔ PHẦN INNO
INNO.,JSC

ĐỊA CHỈ / ADDRESS:
HN: 39 Thượng Thụy, Phú Thượng, Hà Nội
HCM: 37 Nguyễn Văn Hưởng, An Khánh, TP. HCM
Hotline: 0243 212 1776 Email : ad@innojsc.com

TỔNG GIÁM ĐỐC / GENERAL DIRECTOR:
ĐOÀN VĂN ĐỘNG

CHỦ NHIỆM THIẾT KẾ / PROJECT MANAGER:
LƯU GIANG NAM

CHỦ TRÌ THIẾT KẾ / DESIGN MANAGER:
NGÔ NGỌC BÌNH

KIỂM / CHECKED BY:
VŨ TUẤN ANH

THIẾT KẾ / DESIGNER
LÊ THỊ THANH **NGUYỄN XUÂN HIỆN**
PHƯƠNG THỊ ÁNH TUYẾT **VŨ TIẾN DƯƠNG**

TÊN DỰ ÁN / PROJECT NAME:
XÂY DỰNG NHÀ Ở TẠI LÔ ĐẤT NO-02

ĐỊA ĐIỂM XÂY DỰNG / PROJECT ADDRESS:
LÔ ĐẤT NO-22, PHƯỜNG BỒ ĐỀ, HÀ NỘI

HẠNG MỤC / ITEM:
KIẾN TRÚC

HOÀN THÀNH / FINISHED DATE:	MÃ SỐ DỰ ÁN / PROJECT No:
TKCS	2501
HOÀN THÀNH / FINISHED DATE: 2026	PHIÊN BẢN / REVISION: 0

TÊN BẢN VẼ / SHEET NAME:
DANH MỤC BẢN VẼ

SỐ HIỆU BẢN VẼ / SHEET NUMBER:
A-00.001

© 2025 - INNO.,jsc

BẢNG CHÚ GIẢI KÝ HIỆU

STT	KÝ HIỆU	CHÚ GIẢI
1	Tầng 1 ±0.000 CỐT THÔ; Tầng 1 +0.000 CỐT HOÀN THIỆN	KÝ HIỆU CỐT CAO ĐỘ VÀ TÊN CHỨC NĂNG TRÊN MẶT ĐỨNG / MẶT CẮT
2	A1 — A1	KÝ HIỆU TRỤC TỌA ĐỘ Tên trục: 3.5mm (A0-A1) / 2.5mm (A2-A3) Nét trục: Dash 6mm - Dash 1.5mm
3	A A	KÝ HIỆU MỐC, ĐIỂM ĐỊNH VỊ
4	A: X: 0000.000 Y: 0000.000	KÝ HIỆU TỌA ĐỘ ĐIỂM A: X: TRỤC DỌC Y: TRỤC NGANG
5	SSL: +0.000 FFL: +0.000 SSL: -0.050	KÝ HIỆU CAO ĐỘ TRÊN MẶT BẰNG SSL: Lớp thô / FFL: Lớp hoàn thiện
6	SSL: +0.000 FFL: +0.050 CỐT THÔ CỐT HOÀN THIỆN	KÝ HIỆU CAO ĐỘ TRÊN MẶT ĐỨNG, MẶT CẮT SSL: Lớp thô / FFL: Lớp hoàn thiện
7	i=2%	KÝ HIỆU ĐỘ DỐC
8		KÝ HIỆU CHỈNH CỐT
7		KÝ HIỆU LÕ MỞ KẾT CẤU
8		KÝ HIỆU THÔNG TẦNG
9		KÝ HIỆU LÕ THẢM TRẦN
10		KÝ HIỆU CẮT TRÍCH
11		KÝ HIỆU ĐỐI XỨNG
12	B B B	GHI CHÚ HƯỚNG BẮC
13	0m 5m 10m THƯỚC ĐO TỶ LỆ	

BẢNG GHI CHÚ VẬT LIỆU

ĐỐI TƯỢNG	MẪU (TỈ LỆ 1/100)
TƯỜNG	
VỮA, CHẤT KẾT DÍNH	
LỚP CÁCH LY	
BÊ TÔNG CỐT THÉP	
BÊ TÔNG LÓT	
BÊ TÔNG SỎI	
BÊ TÔNG ĐÁ DĂM	
CÁT TÔN NỀN	
ĐẤT TỰ NHIÊN 01	
ĐẤT TỰ NHIÊN 02	
ĐẤT MÀU	
ĐÁ HỌC	
SỎI	
CỎ	
KÍNH	
GỖ	
KIM LOẠI	

GỖ

KÝ HIỆU	TÊN VẬT LIỆU
	GỖ TYPE NAME : FR_Material_Go_01
	GỖ TYPE NAME : FR_Material_Go_02
	GỖ TYPE NAME : FR_Material_Go_03
	GỖ FLYWOOD TYPE NAME : FR_Material_Go-Flywood_01
	GỖ FLYWOOD TYPE NAME : FR_Material_Go-Flywood_02
	GỖ FLYWOOD TYPE NAME : FR_Material_Go-Flywood_03
	GỖ TẤM TYPE NAME : FR_Material_Go-Tam_01
	GỖ TẤM TYPE NAME : FR_Material_Go-Tam_02

KÍNH - KIM LOẠI

KÝ HIỆU	TÊN VẬT LIỆU
	KIM LOẠI TYPE NAME : FR_Material_Kim-Loai
	KÍNH TYPE NAME : FR_Material_Kinh_01
	KÍNH TYPE NAME : FR_Material_Kinh_02
	KÍNH SOLID TYPE NAME : FR_Material_Kinh_Solid
	NHÔM TYPE NAME : FR_Material_Nhom
	SÀN THÉP TYPE NAME : FR_Material_San-Thep
	THÉP TYPE NAME : FR_Material_Thep

GẠCH - NGÓI

KÝ HIỆU	TÊN VẬT LIỆU
	GẠCH TYPE NAME : FR_Material_Gach_01
	GẠCH TYPE NAME : FR_Material_Gach_02
	GẠCH CHỈ 60X220MM TYPE NAME : FR_Material_Gach-Chi_60x220mm
	GẠCH MEN 300X600 TYPE NAME : FR_Material_Gach-Men_300x600mm
	GẠCH MEN 600X600 TYPE NAME : FR_Material_Gach-Men_600x600mm

BÊ TÔNG - VỮA - THẠCH CAO

KÝ HIỆU	TÊN VẬT LIỆU
	BÊ TÔNG CỐT THÉP TYPE NAME : FR_Material_Be-Tong-Cot-Thep
	BÊ TÔNG CỐT THÉP TYPE NAME : FR_Material_Be-Tong-Cot-Thep-Xam
	BÊ TÔNG ĐÁ DĂM TYPE NAME : FR_Material_Be-Tong-Da-Dam
	BÊ TÔNG ĐẶC TYPE NAME : FR_Material_Be-Tong-Dac
	BÊ TÔNG THƯA TYPE NAME : FR_Material_Be-Tong-Thua
	THẠCH CAO TYPE NAME : FR_Material_Thach-cao
	VỮA TRÁT TYPE NAME : FR_Material_Vua-Trat

CÁT - ĐÁ - SỎI

KÝ HIỆU	TÊN VẬT LIỆU
	CÁT TÔN NỀN TYPE NAME : FR_Material_Cat-Ton-Nen
	ĐÁ TYPE NAME : FR_Material_Da
	ĐÁ GRANITE TYPE NAME : FR_Material_Da-Granite
	ĐÁ HỌC TYPE NAME : FR_Material_Da-Hoc
	ĐÁ TỰ NHIÊN TYPE NAME : FR_Material_Da-Tu-Nhien

KÝ HIỆU VẬT LIỆU

ĐẤT TỰ NHIÊN - ĐẤT NỀN

KÝ HIỆU	TÊN VẬT LIỆU
	ĐẤT TYPE NAME : FR_Material_Dat_01
	ĐẤT TYPE NAME : FR_Material_Dat_02
	ĐẤT TYPE NAME : FR_Material_Dat_03
	ĐẤT MÀU TYPE NAME : FR_Material_Dat-Mau
	ĐẤT TỰ NHIÊN TYPE NAME : FR_Material_Dat-Tu-Nhien

0_FILL VẬT LIỆU
TL: 1 : 10

CHÚ GIẢI THAM CHIẾU BẢN VẼ

STT	KÝ HIỆU	CHÚ GIẢI
1	View Name	TÊN BẢN GHI CHÚ KÝ HIỆU Chữ chính: 5mm
2	View Name TL: View Scale	TÊN BẢN VẼ MB MĐ MC TỔNG THỂ Chữ chính: 5mm Chữ tỉ lệ: 2.5mm
3	A-000 View Name TL: View Scale	TÊN BẢN VẼ CHI TIẾT Tên bản vẽ: A0-A1 5mm / A2-A3 3.5mm Chữ tỉ lệ: A0-A1 3.5mm / A2-A3 2.5mm Chữ ký hiệu bản vẽ: A0-A1 5mm / A2-A3 3.5mm
4	MC-01 A101	KÝ HIỆU MẶT CẮT CHỈNH Số hiệu chi tiết Xem bản vẽ chi tiết Hướng cắt
5	MC_CT-01 A001 — MC_CT-01 A101	KÝ HIỆU MẶT CẮT TRÍCH CHI TIẾT Số hiệu chi tiết Xem bản vẽ chi tiết Hướng cắt
6	DD01_CNL_MB DD01_CNL_MB A101	KÝ HIỆU TRÍCH CHI TIẾT Khu vực trích chi tiết Số hiệu chi tiết Xem bản vẽ chi tiết
7	A D A001 B C MẶT ĐỨNG CHÍNH; A D A001 B C MẶT ĐỨNG CHI TIẾT	KÝ HIỆU THAM CHIẾU MẶT ĐỨNG Xem bản vẽ chi tiết Số hiệu chi tiết Hướng mặt đứng

CÁC LOẠI CHÚ THÍCH (TAG)

STT	KÝ HIỆU	CHÚ GIẢI
1	TÊN PHÒNG P-101 123.4 m²	CHÚ THÍCH PHÒNG: Tên phòng, số phòng, diện tích.
2	D01 1200 x 2100 LOẠI CỬA; Mark 1200 x 2100 MÃ CỬA	CHÚ THÍCH CỬA ĐI Loại cửa, mã cửa. Kích thước hoàn thiện Chiều rộng*Chiều cao
3	T2 T2	CHÚ THÍCH LOẠI TƯỜNG
4	+Cao Do TR2 MẶT BẰNG; +Cao Do TR2 MẶT CẮT	CHÚ THÍCH LOẠI TRẦN
5	S01 MẶT BẰNG; S01 MẶT CẮT	CHÚ THÍCH LOẠI SÀN
6	1t	CHÚ THÍCH CẤU KIỆN
7	W01 1200 x 2100 LOẠI CỬA; Mark 1200 x 2100 MÃ CỬA	CHÚ THÍCH CỬA SỔ Loại cửa, mã cửa. Kích thước hoàn thiện Chiều rộng*Chiều cao
8	1t	CHÚ THÍCH LOẠI MÁI

PHIÊN BẢN	NỘI DUNG ĐIỀU CHỈNH	NGÀY NỘP

GHI CHÚ:

- CỐT +0.000 LẤY TẠI SÀN HOÀN THIỆN TẦNG 1 CÔNG TRÌNH TƯƠNG ĐƯƠNG COTE TUYỆT ĐỐI +7.900 (HỆ TỌA ĐỘ VN-2000)

- TÒA 1 CHIỀU CAO CÔNG TRÌNH TÍNH TỪ:
  + COTE HOÀN THIỆN +0.000: 43M
  + COTE NỀN TỰ NHIÊN THẤP NHẤT -1.000: 44M
- TÒA 2 CHIỀU CAO CÔNG TRÌNH TÍNH TỪ:
  + COTE HOÀN THIỆN +0.000: 50M
  + COTE NỀN TỰ NHIÊN THẤP NHẤT -1.000: 51M
- TÒA 3 CHIỀU CAO CÔNG TRÌNH TÍNH TỪ:
  + COTE HOÀN THIỆN +0.000: 59M
  + COTE NỀN TỰ NHIÊN THẤP NHẤT -1.000: 60M

- KHU VỰC TMDV BÀN GIAO THÔ, VỆ SINH KHÔNG XÂY, CHỈ BỐ TRÍ LAYOUT ĐỊNH HƯỚNG ĐẶT CÁC ĐẦU CHỜ.

- TỶ LỆ SỬ DỤNG VẬT LIỆU XANH KHÔNG NUNG ĐÁP ỨNG TỚI 90% KHỐI LƯỢNG GẠCH TRONG CÔNG TRÌNH

- TRONG PHÒNG RÁC KHÔNG BỐ TRÍ CÁC CHẤT, VẬT LIỆU CÓ KHẢ NĂNG GÂY CHÁY NỔ

- TƯỜNG NGĂN CHÁY, VÁCH NGĂN CHÁY TRONG CÁC GIAN PHÒNG ĐƯỢC NGĂN CHIA ĐẾN TRẦN BÊ TÔNG.

- VẬT LIỆU HOÀN THIỆN TRẦN, TƯỜNG, SÀN TRÊN CÁC ĐƯỜNG THOÁT NẠN, TRONG SẢNH THANG MÁY, SẢNH CHUNG, TẦNG KỸ THUẬT LÀ VẬT LIỆU KHÔNG CHÁY ĐẠT CV0

- TRONG CÁC KHÔNG GIAN TRẦN TREO KHÔNG BỐ TRÍ CÁC KÊNH, ĐƯỜNG ỐNG DẪN VẬN CHUYỂN CÁC CHẤT CHÁY DẠNG KHÍ, HỖN HỢP KHÍ, CHẤT LỎNG VÀ VẬT LIỆU CHÁY.

- TRONG CÔNG TRÌNH KHÔNG BỐ TRÍ TRẦN TREO CHO CÁC GIAN PHÒNG HẠNG A VÀ HẠNG B

- KHÔNG CÓ KÊNH, GIẾNG, ĐƯỜNG ỐNG ĐI QUA TƯỜNG NGĂN CHÁY LOẠI 1

CHỦ ĐẦU TƯ / OWNER:
CÔNG TY CỔ PHẦN THƯƠNG MẠI DƯƠNG PHÚC THẮNG
DUONG PHUC THANG TRADING JOINT STOCK COMPANY
ĐỊA CHỈ / ADDRESS: Tầng 16, Tòa OSI Tower, Khu tây Hồ Tây, Phường Xuân Đỉnh, Thành phố Hà Nội, Việt Nam.
Hotline : 0243 2077 272

TƯ VẤN KIẾN TRÚC CHÍNH / MAIN ARCHITECTURAL CONSULTANT:
CÔNG TY TNHH KIẾN TRÚC DP VIỆT NAM
DP ARCHITECTS VIETNAM CO.,LTD.
ĐỊA CHỈ / ADDRESS: Tầng 4, số 82 Võ Văn Tần, Phường Xuân Hòa, TP.Hồ Chí Minh
Hotline : 0283 5357 507
Fax: 0283 5357 517
Email : dparchitects@dpa.com.sg

TƯ VẤN THIẾT KẾ / CONSULTANT:
CÔNG TY CỔ PHẦN INNO
INNO.,JSC
ĐỊA CHỈ / ADDRESS: HN: 39 Thượng Thụy, Phú Thượng, Hà Nội
HCM: 37 Nguyễn Văn Hưởng, An Khánh, TP. HCM
Hotline: 0243 212 1776 Email : ad@innojsc.com

TỔNG GIÁM ĐỐC / GENERAL DIRECTOR: **ĐOÀN VĂN ĐỘNG**
CHỦ NHIỆM THIẾT KẾ / PROJECT MANAGER: **LƯU GIANG NAM**
CHỦ TRÌ THIẾT KẾ / DESIGN MANAGER: **NGÔ NGỌC BÌNH**
KIỂM / CHECKED BY: **VŨ TUẤN ANH**
THIẾT KẾ / DESIGNER: **LÊ THỊ THANH** **NGUYỄN XUÂN HIỆN** **PHƯƠNG THỊ ÁNH TUYẾT** **VŨ TIẾN DƯƠNG**

TÊN DỰ ÁN / PROJECT NAME:
XÂY DỰNG NHÀ Ở TẠI LÔ ĐẤT NO-02

ĐỊA ĐIỂM XÂY DỰNG / PROJECT ADDRESS:
LÔ ĐẤT NO-22, PHƯỜNG BỒ ĐỀ, HÀ NỘI

HẠNG MỤC / ITEM: KIẾN TRÚC

HOÀN THÀNH / FINISHED DATE:	MÃ SỐ DỰ ÁN / PROJECT No:
TKCS	2501
HOÀN THÀNH / FINISHED DATE: 2026	PHIÊN BẢN / REVISION: 0

TÊN BẢN VẼ / SHEET NAME: **GHI CHÚ KÝ HIỆU**

SỐ HIỆU BẢN VẼ / SHEET NUMBER: **A-00.002**

© 2025 - INNO.,jsc

CÁC KIỂU CẤU TẠO TRẦN

TR.1 - TRẦN THẠCH CAO XƯƠNG CHÌM - SẢNH, HÀNH LANG, BẾP, PHÒNG NGỦ, PHÒNG KHÁCH

TR.1

HỆ KHUNG XƯƠNG CHÌM
(THEO TIÊU CHUẨN NHÀ CUNG CẤP)
TẤM THẠCH CAO DÀY 9MM
TRẦN BÊ TÔNG MÁI NHÂN

TR.2 - TRẦN THẠCH CAO CHỐNG ẨM - KHU VỆ SINH, TẠP VỤ

TR.2

HỆ KHUNG XƯƠNG CHÌM
(THEO TIÊU CHUẨN NHÀ CUNG CẤP)
TẤM THẠCH CAO CHỐNG ẨM DÀY 9MM
TRẦN BÊ TÔNG MÁI NHÂN

TR.3 - TRẦN THẠCH CAO KHUNG XƯƠNG NỔI - VĂN PHÒNG, PHÒNG BẢO VỆ TẦNG HẦM

TR.3

HỆ KHUNG XƯƠNG NỔI KÍCH THƯỚC 600x600MM
TẤM THẠCH CAO DÀY 9MM
TRẦN BÊ TÔNG MÁI NHÂN

TR.4 - TRẦN BTCT - KHU VỰC SHOPHOUSE, ĐỂ XE, CÁC PHÒNG KỸ THUẬT

TR.4

TRẦN BTCT

TR.4* - TRẦN BTCT MÀI NHẴN, HT SƠN NƯỚC - KHU VỰC THANG BỘ, BUỒNG ĐỆM

TR.4*

TRẦN BTCT
MÀI NHẴN LÀM SẠCH BỀ MẶT
BẢ TRÁM TRẾT BẰNG SKIMCOAT
SƠN MÀU TRẮNG (1 LÓT, 2 MÀU)

TR.5 - TRẦN NHÔM VÂN GỖ - KHU VỰC LOGIA, BAN CÔNG

TR.5

TRẦN BTCT
TRẦN NHÔM VÂN GỖ ĐỘ DÀY THEO THIẾT KẾ ID

CÁC KIỂU CẤU TẠO SÀN

S1 - SÀN LÁT GẠCH POCELAINCE - SẢNH, HÀNH LANG

S1

GẠCH POCELAINCE DÀY TB 10MM
(HOẶC TƯƠNG ĐƯƠNG)
VỮA XI MĂNG #75 DÀY TRUNG BÌNH 30MM
SÀN BTCT LÀM SẠCH BỀ MẶT

S2 - SÀN GỖ CÔNG NGHIỆP - PHÒNG KHÁCH, BẾP, NGỦ, KHO

S2

- GỖ CÔNG NGHIỆP DÀY 12MM (HOẶC TƯƠNG ĐƯƠNG)
- LỚP XỐP LÓT SÀN
- VỮA XI MĂNG #75 TẠO PHẲNG DÀY 30MM
- SÀN BTCT LÀM SẠCH BỀ MẶT (XEM BVKC).

S4 - SÀN BTCT THÔ - KHU VỰC SHOPHOUSE

S4

SÀN BTCT LÀM SẠCH BỀ MẶT

S5 - SÀN SƠN EPOXY - PHÒNG KỸ THUẬT (THÁP)

S5

SƠN EPOXY DÀY 2MM (HOẶC TƯƠNG ĐƯƠNG)
SÀN BTCT LÀM SẠCH BỀ MẶT

S6 - GẠCH POCELAINCE CHỐNG TRƠN - KHU VỰC VỆ SINH, LOGIA

S6

- GẠCH POCELAINCE CHỐNG TRƠN DÀY TB 10MM
- KEO DÁN GẠCH CHUYÊN DỤNG
- LỚP VỮA XI MĂNG #75 DỐC 1% VỀ PHỄU THU VỊ TRÍ MỎNG NHẤT DÀY 20MM
- LỚP CHỐNG THẤM
- SÀN BTCT LÀM SẠCH BỀ MẶT (XEM BVKC).

S7 - SÀN GỖ NHỰA - KHU VỰC BỂ BƠI

S7

- GỖ NHỰA COMPOSITE DÀY 25MM
- KHUNG THÉP HỘP MẠ KẼM 30X30X2MM
- LỚP VỮA XI MĂNG #75 DÀY TB 40MM TẠO DỐC VỀ GA THU NƯỚC
- LỚP CHỐNG THẤM
- SÀN BTCT LÀM SẠCH BỀ MẶT (XEM BVKC).

ST1 - LỚP CẤU TẠO BẬN THANG - KHU VỰC THANG BỘ

ST1

GẠCH POCELAINCE CHỐNG TRƠN DÀY TB 10MM (HOẶC TƯƠNG ĐƯƠNG)
- LỚP VỮA TẠO PHẲNG MÁC 100 DÀY 20MM.
- BẢN BÊ TÔNG CỐT THÉP (XEM BVTC).
- HOÀN THIỆN ĐÁY BẬN THANG SƠN MÀU TRẮNG

ST2 - LỚP CẤU TẠO BẬN THANG - TẠI CÁC BẬC CẤP NGOÀI NHÀ

ST2

- LỚP ĐÁ TỰ NHIÊN DÀY 20MM.
- LỚP VỮA LIÊN KẾT MÁC 100 DÀY 15MM.
- XÂY GẠCH TẠO BẬC
- BẢN BTCT (XEM BVKC).
- LỚP BÊ TÔNG LÓT DÀY 100MM.
- LỚP CÁT TÔN NỀN ĐẦM CHẶT.

N1 - SÀN PHỦ HARDENER - KHU VỰC ĐỂ XE HẦM

N1

- SÀN PHỦ HARDENER DÀY 2MM (HOẶC TƯƠNG ĐƯƠNG)
- SÀN BTCT LÀM SẠCH BỀ MẶT

N2 - SÀN PHỦ HARDENER - KHU VỰC ĐỂ XE HẦM B2

N2

- SÀN PHỦ HARDENER DÀY 2MM (HOẶC TƯƠNG ĐƯƠNG)
- SÀN BTCT CÓ PHỤ GIA CHỐNG THẤM (XEM BVKC).
- LỚP BÊ TÔNG LÓT #200 DÀY 100MM.
- ĐẤT TỰ NHIÊN ĐẦM CHẶT.

N3 - SÀN HOÀN THIỆN LÁT GẠCH - KHU VỰC HÀNH LANG, SẢNH, VP,... HẦM B2

N3

- GẠCH POCELAINCE DÀY TB 10MM (HOẶC TƯƠNG ĐƯƠNG)
- SÀN BTCT CÓ PHỤ GIA CHỐNG THẤM (XEM BVKC).
- LỚP BÊ TÔNG LÓT MÁC 200 DÀY 100MM.
- ĐẤT TỰ NHIÊN ĐẦM CHẶT.

D1 - LỚP CẤU TẠO ĐƯỜNG DỐC - ĐƯỜNG DỐC Ô TÔ

D1

- BẢN SÀN DỐC BÊ TÔNG CỐT THÉP (XEM BVKC).
KHÍA RÃNH KT 20X10MM, CÁCH ĐỀU NHAU 200MM.

N4 - SÀN SƠN EPOXY - KHU VỰC PHÒNG KỸ THUẬT

N4

- SƠN EPOXY DÀY 2MM (HOẶC TƯƠNG ĐƯƠNG)
- SÀN BTCT LÀM SẠCH BỀ MẶT

N5 - SÀN SƠN EPOXY - KHU VỰC PHÒNG KỸ THUẬT HẦM B2

N5

- SƠN EPOXY DÀY 2MM (HOẶC TƯƠNG ĐƯƠNG)
- SÀN BTCT CÓ PHỤ GIA CHỐNG THẤM (XEM BVKC).
- LỚP BÊ TÔNG LÓT MÁC 200 DÀY 100MM.
- ĐẤT TỰ NHIÊN ĐẦM CHẶT.

N6 - SÀN BÊ TÔNG SƠN CHỐNG THẤM - KHU VỰC THẤP GIÓ

N6

- CHỐNG THẤM BỀ MẶT
- SÀN BTCT LÀM SẠCH BỀ MẶT

BE1 - BỂ NƯỚC PCCC, BỂ XLNT - SÀN HOÀN THIỆN LÁNG VỮA

BE1

- VỮA CÂN NỀN HOÀN THIỆN
- LỚP CHỐNG THẤM
- SÀN BTCT LÀM SẠCH BỀ MẶT

BE2 - BỂ NƯỚC SINH HOẠT - SÀN HOÀN THIỆN LÁT GẠCH

BE2

- GẠCH CERAMIC 300X600MM
- LỚP VỮA XM #75 DÀY 15MM
- LỚP CHỐNG THẤM
- SÀN BTCT LÀM SẠCH BỀ MẶT

BB - GẠCH MOSAIC - ĐÁY, THÀNH BỂ BƠI

BB

- GẠCH MOSAIC
- LỚP KEO DÁN CHUYÊN DỤNG
- VỮA XI MĂNG #75 DÀY 40MM VỚI ĐÁY BỂ VÀ 15MM VỚI THÀNH BỂ
- LỚP CHỐNG THẤM
- SÀN BTCT LÀM SẠCH BỀ MẶT

M1 - GẠCH CERAMIC CHỐNG TRƠN - MÁI TUM

M1

- GẠCH CARAMIC 400x400MM CHỐNG TRƠN DÀY TB 10MM
- VỮA XI MĂNG #75 TẠO DỐC
- LỚP CHỐNG THẤM
- SÀN BTCT LÀM SẠCH BỀ MẶT

CÁC KIỂU CẤU TẠO TƯỜNG

T1 - TƯỜNG SƠN NỘI THẤT - KHU VỰC SHOPHOUSE

TRÁT HOÀN THIỆN DÀY 15MM
TƯỜNG XÂY GẠCH XMCL RỖNG KHÔNG NUNG
TRÁT HOÀN THIỆN DÀY 15MM

T2 - TƯỜNG SƠN NỘI THẤT - KHU VỰC BÊN TRONG CĂN HỘ

SƠN NƯỚC NỘI THẤT (1 LÓT, 2 MÀU)
BẢ MATIT
TRÁT HOÀN THIỆN DÀY 15MM
TƯỜNG XÂY GẠCH XMCL RỖNG KHÔNG NUNG
TRÁT HOÀN THIỆN DÀY 15MM
BẢ MATIT
SƠN NƯỚC NỘI THẤT (1 LÓT, 2 MÀU)

T3 - TƯỜNG SƠN NỘI THẤT - KHU VỰC THANG BỘ, PHÒNG VẬT TƯ KHÔNG CHÁY

SƠN NƯỚC NỘI THẤT
TRÁT HOÀN THIỆN DÀY 15MM
TƯỜNG XÂY GẠCH XMCL RỖNG KHÔNG NUNG
TRÁT HOÀN THIỆN DÀY 15MM
SƠN NƯỚC NỘI THẤT

T4 - TƯỜNG ỐP GẠCH - KHU VỰC VỆ SINH CÔNG CỘNG, VỆ SINH CĂN HỘ, PHÒNG RÁC

- GẠCH POCELAINCE
- TRÁT VỮA XI MĂNG DÀY 15MM
- TƯỜNG XÂY GẠCH XMCL ĐẶC KHÔNG NUNG
- TRÁT VỮA XI MĂNG DÀY 15MM
- SƠN NƯỚC NỘI THẤT (1 LÓT, 2 MÀU)

T5 - TƯỜNG NGOẠI THẤT - TƯỜNG BAO NGOÀI NHÀ

LỚP NHÔM COMPOSITE DÀY 3-4MM
TRÁT VỮA XI MĂNG DÀY 15MM
LỚP CHỐNG THẤM
TƯỜNG XÂY GẠCH XMCL ĐẶC KHÔNG NUNG
TRÁT VỮA XI MĂNG DÀY 15MM
BẢ MATIT
SƠN NƯỚC NỘI THẤT (1 LÓT, 2 MÀU)

T5* - TƯỜNG NGOẠI THẤT - TƯỜNG BAO NGOÀI NHÀ KHU VỰC YARD

TRÁT VỮA XI MĂNG DÀY 15MM
LỚP CHỐNG THẤM
TƯỜNG XÂY GẠCH XMCL ĐẶC KHÔNG NUNG
TRÁT VỮA XI MĂNG DÀY 15MM
BẢ MATIT
SƠN NƯỚC NỘI THẤT (1 LÓT, 2 MÀU)

T6 - VÁCH BÊ TỰ HOẠI, BÊ PCCC - VÁCH BÊ TÔNG

VÁCH BÊ TÔNG
TRÁT VỮA XI MĂNG DÀY 15MM
ĐÁNH BÓNG XI MĂNG NGUYÊN CHẤT
LỚP VẬT LIỆU CHỐNG THẤM

T7 - VÁCH BÊ NƯỚC SINH HOẠT - VÁCH BÊ TÔNG ỐP GẠCH

GẠCH ỐP
TRÁT VỮA XI MĂNG DÀY 15MM
VÁCH BÊ TÔNG
TRÁT VỮA XI MĂNG DÀY 15MM
SƠN NƯỚC NỘI THẤT (1 LÓT, 2 MÀU)

T8 - TƯỜNG SƠN NỘI THẤT - TƯỜNG CÁC PHÒNG KỸ THUẬT

SƠN NƯỚC NỘI THẤT
TRÁT HOÀN THIỆN DÀY 15MM
TƯỜNG XÂY GẠCH XMCL ĐẶC KHÔNG NUNG
TRÁT HOÀN THIỆN DÀY 15MM
SƠN NƯỚC NỘI THẤT

T9 - TƯỜNG SƠN NỘI/NGOẠI THẤT - TƯỜNG HỘP KỸ THUẬT

TƯỜNG XÂY GẠCH XMCL ĐẶC KHÔNG NUNG
TRÁT HOÀN THIỆN DÀY 15MM
SƠN NƯỚC NỘI/NGOẠI THẤT

T10 - TƯỜNG SƠN NỘI THẤT - TƯỜNG HÀNH LANG TẦNG CĂN HỘ

SƠN NƯỚC NỘI THẤT (1 LÓT, 2 MÀU)
BẢ MATIT
TRÁT HOÀN THIỆN DÀY 15MM
TƯỜNG XÂY GẠCH XMCL RỖNG KHÔNG NUNG
HOÀN THIỆN THEO TK NỘI THẤT

PHIÊN BẢN	NỘI DUNG ĐIỀU CHỈNH	NGÀY NỘP

GHI CHÚ:

- CỐT +0.000 LẤY TẠI SÀN HOÀN THIỆN TẦNG 1 CÔNG TRÌNH TƯƠNG ĐƯƠNG COTE TUYỆT ĐỐI +7.900 (HỆ TỌA ĐỘ VN-2000)

- TÒA 1 CHIỀU CAO CÔNG TRÌNH TÍNH TỪ:
  + COTE HOÀN THIỆN +0.000: 43M
  + COTE NỀN TỰ NHIÊN THẤP NHẤT -1.000: 44M
- TÒA 2 CHIỀU CAO CÔNG TRÌNH TÍNH TỪ:
  + COTE HOÀN THIỆN +0.000: 50M
  + COTE NỀN TỰ NHIÊN THẤP NHẤT -1.000: 51M
- TÒA 3 CHIỀU CAO CÔNG TRÌNH TÍNH TỪ:
  + COTE HOÀN THIỆN +0.000: 59M
  + COTE NỀN TỰ NHIÊN THẤP NHẤT -1.000: 60M

- KHU VỰC TMDV BÀN GIAO THÔ, VỆ SINH KHÔNG XÂY, CHỈ BỐ TRÍ LAYOUT ĐỊNH HƯỚNG ĐẶT CÁC ĐẦU CHỜ.

- TỶ LỆ SỬ DỤNG VẬT LIỆU XANH KHÔNG NUNG ĐÁP ỨNG TỐI 90% KHỐI LƯỢNG GẠCH TRONG CÔNG TRÌNH

- TRONG PHÒNG RÁC KHÔNG BỐ TRÍ CÁC CHẤT, VẬT LIỆU CÓ KHẢ NĂNG GÂY CHÁY NỔ

- TƯỜNG NGĂN CHÁY, VÁCH NGĂN CHÁY TRONG CÁC GIAN PHÒNG ĐƯỢC NGĂN CHIA ĐẾN TRẦN BÊ TÔNG.

- VẬT LIỆU HOÀN THIỆN TRẦN, TƯỜNG, SÀN TRÊN CÁC ĐƯỜNG THOÁT NẠN, TRONG SẢNH THANG MÁY, SẢNH CHUNG, TẦNG KỸ THUẬT LÀ VẬT LIỆU KHÔNG CHÁY ĐẠT CV0

- TRONG CÁC KHÔNG GIAN TRẦN TREO KHÔNG BỐ TRÍ CÁC KÊNH, ĐƯỜNG ỐNG DẪN VẬN CHUYỂN CÁC CHẤT CHÁY DẠNG KHÍ, HỖN HỢP KHÍ, CHẤT LỎNG VÀ VẬT LIỆU CHÁY.

- TRONG CÔNG TRÌNH KHÔNG BỐ TRÍ TRẦN TREO CHO CÁC GIAN PHÒNG HẠNG A VÀ HẠNG B

- KHÔNG CÓ KÊNH, GIẾNG, ĐƯỜNG ỐNG ĐI QUA TƯỜNG NGĂN CHÁY LOẠI 1

CHỦ ĐẦU TƯ / OWNER:
CÔNG TY CỔ PHẦN THƯƠNG MẠI DƯƠNG PHÚC THĂNG
DUONG PHUC THANG TRADING JOINT STOCK COMPANY
ĐỊA CHỈ / ADDRESS:
Tầng 16, Tòa Odi Tower, Khu tây Hồ Tây, Phường Xuân Đỉnh, Thành phố Hà Nội, Việt Nam.
Hotline : 0243 2077 272

TƯ VẤN KIẾN TRÚC CHÍNH / MAIN ARCHITECTURAL CONSULTANT:
CÔNG TY TNHH KIẾN TRÚC DP VIỆT NAM
DP ARCHITECTS VIETNAM CO.,LTD.
ĐỊA CHỈ / ADDRESS:
Tầng 4, số 82 Võ Văn Tần, Phường Xuân Hòa, TP.Hồ Chí Minh
Hotline : 0283 5357 507
Fax: 0283 5357 517
Email : dparchitects@dpa.com.sg

TƯ VẤN THIẾT KẾ / CONSULTANT:
CÔNG TY CỔ PHẦN INNO
INNO.,JSC
ĐỊA CHỈ / ADDRESS:
HN: 39 Thượng Thụy, Phú Thượng, Hà Nội
HCM: 37 Nguyễn Văn Hưởng, An Khánh, TP. HCM
Hotline: 0243 212 1776 Email : ad@innojsc.com

TỔNG GIÁM ĐỐC / GENERAL DIRECTOR:
ĐOÀN VĂN ĐỘNG
CHỦ NHIỆM THIẾT KẾ / PROJECT MANAGER:
LƯU GIANG NAM
CHỦ TRÌ THIẾT KẾ / DESIGN MANAGER:
NGÔ NGỌC BÌNH
KIỂM / CHECKED BY:
VŨ TUẤN ANH
THIẾT KẾ / DESIGNER
LÊ THỊ THANH **NGUYỄN XUÂN HIỆN**
PHƯƠNG THỊ ÁNH TUYẾT **VŨ TIẾN DƯƠNG**

TÊN DỰ ÁN / PROJECT NAME:
XÂY DỰNG NHÀ Ở TẠI LÔ ĐẤT NO-02

ĐỊA ĐIỂM XÂY DỰNG / PROJECT ADDRESS:
LÔ ĐẤT NO-22, PHƯỜNG BỒ ĐỀ, HÀ NỘI

HẠNG MỤC / ITEM:
KIẾN TRÚC

HOÀN THÀNH / FINISHED DATE:	MÃ SỐ DỰ ÁN / PROJECT No:
TKCS	2501
HOÀN THÀNH / FINISHED DATE: 2026	PHIÊN BẢN / REVISION: 0

TÊN BẢN VẼ / SHEET NAME:
GHI CHÚ CẤU TẠO

SỐ HIỆU BẢN VẼ / SHEET NUMBER:
A-00.003

© 2025 - INNO.,jsc

CÔNG TY PHYTOPHARCO
(Kho bảo quản thuốc, bậc chịu lửa IV,
cấp nguy hiểm cháy S0, hạng sản xuất C

MÁI CỔNG VÀO HẦM
KẾT CẤU MÁI NHẸ

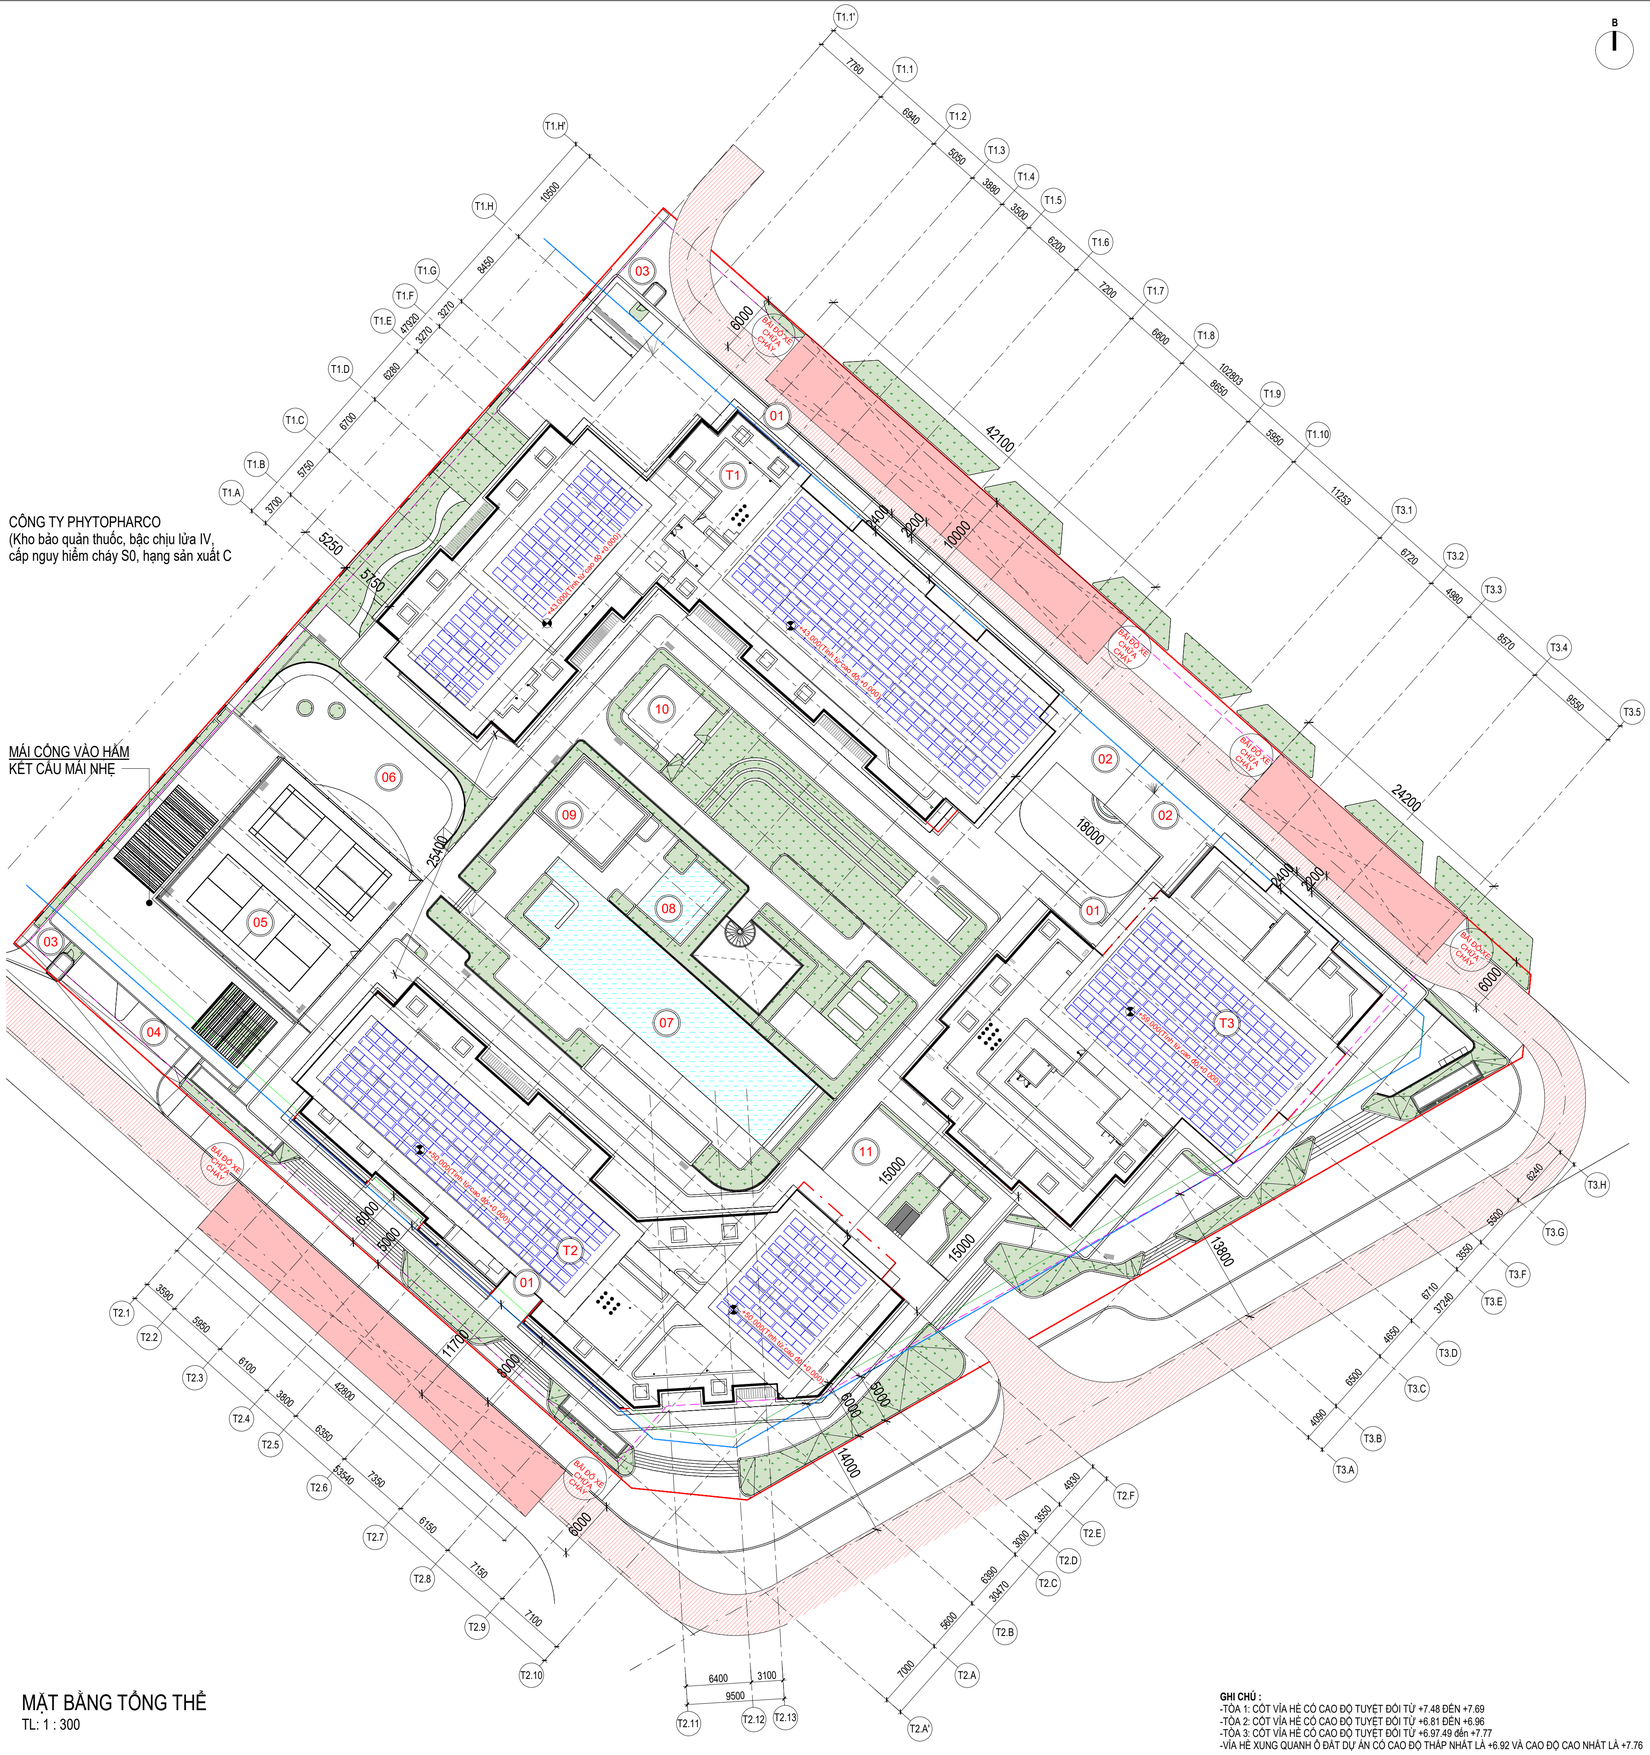

MẶT BẰNG TỔNG THỂ
TL: 1 : 300

GHI CHÚ :
-TÒA 1: CỐT VỈA HÈ CÓ CAO ĐỘ TUYỆT ĐỐI TỪ +7.48 ĐẾN +7.69
-TÒA 2: CỐT VỈA HÈ CÓ CAO ĐỘ TUYỆT ĐỐI TỪ +6.81 ĐẾN +6.96
-TÒA 3: CỐT VỈA HÈ CÓ CAO ĐỘ TUYỆT ĐỐI TỪ +6.97.49 đến +7.77
-VỈA HÈ XUNG QUANH Ô ĐẤT DỰ ÁN CÓ CAO ĐỘ THẤP NHẤT LÀ +6.92 VÀ CAO ĐỘ CAO NHẤT LÀ +7.76

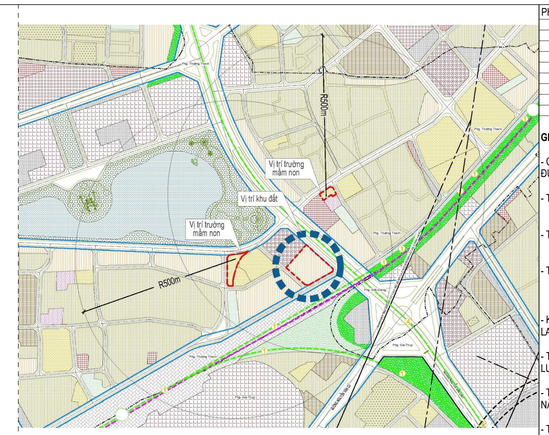

T1	THÁP 1	02	SẢNH ĐÓN TRẢ KHÁCH	06	SÂN CHƠI ĐA NĂNG
T2	THÁP 2	03	LỐI RA - VÀO HẦM	07	HỒ BƠI CHÍNH
T3	THÁP 3	04	KHU VỰC SẠC XE ĐIỆN	08	HỒ BƠI TRẺ EM
01	SẢNH CĂN HỘ	05	SÂN PICKLEBALL	09	KHU TẮM TRẮNG NGOÀI TRỜI
				10	KHU VỰC TẬP YOGA
				11	KHU VỰC TỔ CHỨC SỰ KIỆN

SỐ TẦNG CAO

BÃI ĐỖ XE PCCC
CÁC GÓC BÃI ĐỖ SƠN PHẢN QUANG KHÔNG CÓ KẾT CẤU CHẮN PHÍA TRÊN

ĐƯỜNG CHO XE CHỮA CHÁY
TẢI TRỌNG PHÙ HỢP VỚI CÁC PHƯƠNG TIỆN PCCC VÀ CỨU NẠN CỦA ĐỊA PHƯƠNG
KHÔNG CÓ KẾT CẤU CHẮN PHÍA TRÊN

BÃI ĐỖ XE CHỮA CHÁY
BIỂN BÁO BÃI ĐỖ XE CHỮA CHÁY
(TẠI ĐIỂM ĐẦU VÀ CUỐI BÃI ĐỖ XE CHỮA CHÁY)

CHỈ GIỚI XÂY DỰNG

KHOẢNG LÙI XÂY DỰNG TỪ TẦNG 6 TRỞ LÊN

RANH GIỚI XÂY DỰNG PHẦN HẦM

CHỈ GIỚI ĐƯỜNG ĐỎ (TRÙNG VỚI RANH GIỚI KHU ĐẤT)

GHI CHÚ:
KHOẢNG KHÔNG GIỮA BÃI ĐỖ XE PCCC TỚI MÁI CANO(Y 2200MM KHÔNG CÓ CÂY XANH VÀ VẬT THỂ CỐ ĐỊNH.

PHIÊN BẢN	NỘI DUNG ĐIỀU CHỈNH	NGÀY NỘP

GHI CHÚ:

- CỐT +0.000 LẤY TẠI SÀN HOÀN THIỆN TẦNG 1 CÔNG TRÌNH TƯƠNG ĐƯƠNG COTE TUYỆT ĐỐI +7.900 (HỆ TỌA ĐỘ VN-2000)

- TÒA 1 CHIỀU CAO CÔNG TRÌNH TÍNH TỪ:
  + COTE HOÀN THIỆN +0.000: 43M
  + COTE NỀN TỰ NHIÊN THẤP NHẤT -1.000: 44M
- TÒA 2 CHIỀU CAO CÔNG TRÌNH TÍNH TỪ:
  + COTE HOÀN THIỆN +0.000: 50M
  + COTE NỀN TỰ NHIÊN THẤP NHẤT -1.000: 51M
- TÒA 3 CHIỀU CAO CÔNG TRÌNH TÍNH TỪ:
  + COTE HOÀN THIỆN +0.000: 59M
  + COTE NỀN TỰ NHIÊN THẤP NHẤT -1.000: 60M

- KHU VỰC TMDV BÀN GIAO THÔ, VỆ SINH KHÔNG XÂY, CHỈ BỐ TRÍ LAYOUT ĐỊNH HƯỚNG ĐẶT CÁC ĐẦU CHỜ.

- TỶ LỆ SỬ DỤNG VẬT LIỆU XANH KHÔNG NUNG ĐÁP ỨNG TỚI 90% KHỐI LƯỢNG GẠCH TRONG CÔNG TRÌNH

- TRONG PHÒNG RÁC KHÔNG BỐ TRÍ CÁC CHẤT, VẬT LIỆU CÓ KHẢ NĂNG GÂY CHÁY NỔ

- TƯỜNG NGĂN CHÁY, VÁCH NGĂN CHÁY TRONG CÁC GIAN PHÒNG ĐƯỢC NGĂN CHIA ĐẾN TRẦN BÊ TÔNG.

- VẬT LIỆU HOÀN THIỆN TRẦN, TƯỜNG, SÀN TRÊN CÁC ĐƯỜNG THOÁT NẠN, TRONG SẢNH THANG MÁY, SẢNH CHUNG, TẦNG KỸ THUẬT LÀ VẬT LIỆU KHÔNG CHÁY ĐẠT CV0

- TRONG CÁC KHÔNG GIAN TRẦN TREO KHÔNG BỐ TRÍ CÁC KÊNH, ĐƯỜNG ỐNG DẪN VẬN CHUYỂN CÁC CHẤT CHÁY DẠNG KHÍ, HỖN HỢP KHÍ, CHẤT LỎNG VÀ VẬT LIỆU CHÁY.

- TRONG CÔNG TRÌNH KHÔNG BỐ TRÍ TRẦN TREO CHO CÁC GIAN PHÒNG HẠNG A VÀ HẠNG B

- KHÔNG CÓ KÊNH, GIÉNG, ĐƯỜNG ỐNG ĐI QUA TƯỜNG NGĂN CHÁY LOẠI 1

CHỦ ĐẦU TƯ / OWNER:
CÔNG TY CỔ PHẦN THƯƠNG MẠI DƯƠNG PHÚC THẮNG
DUONG PHUC THANG TRADING JOINT STOCK COMPANY
ĐỊA CHỈ / ADDRESS:
Tầng 16, Tòa OSI Tower, Khu tây Hồ Tây, Phường Xuân Đỉnh, Thành phố Hà Nội, Việt Nam.
Hotline : 0243 2077 272

TƯ VẤN KIẾN TRÚC CHÍNH / MAIN ARCHITECTURAL CONSULTANT:
CÔNG TY TNHH KIẾN TRÚC DP VIỆT NAM
DP ARCHITECTS VIETNAM CO.,LTD.
ĐỊA CHỈ / ADDRESS:
Tầng 4, số 82 Võ Văn Tần, Phường Xuân Hòa, TP.Hồ Chí Minh
Hotline : 0283 5357 507
Fax: 0283 5357 517
Email : dparchitects@dpa.com.sg

TƯ VẤN THIẾT KẾ / CONSULTANT:
CÔNG TY CỔ PHẦN INNO
INNO.,JSC
ĐỊA CHỈ / ADDRESS:
HN: 39 Thượng Thụy, Phú Thượng, Hà Nội
HCM: 37 Nguyễn Văn Hưởng, An Khánh, TP. HCM
Hotline: 0243 212 1776 Email : ad@innojsc.com

TỔNG GIÁM ĐỐC / GENERAL DIRECTOR:
ĐOÀN VĂN ĐỘNG
CHỦ NHIỆM THIẾT KẾ / PROJECT MANAGER:
LƯU GIANG NAM
CHỦ TRÌ THIẾT KẾ / DESIGN MANAGER:
NGÔ NGỌC BÌNH
KIỂM / CHECKED BY:
VŨ TUẤN ANH
THIẾT KẾ / DESIGNER
LÊ THỊ THANH **NGUYỄN XUÂN HIỆN**
PHƯƠNG THỊ ÁNH TUYẾT **VŨ TIẾN DƯƠNG**

TÊN DỰ ÁN / PROJECT NAME:
XÂY DỰNG NHÀ Ở TẠI LÔ ĐẤT NO-02

ĐỊA ĐIỂM XÂY DỰNG / PROJECT ADDRESS:
LÔ ĐẤT NO-22, PHƯỜNG BỒ ĐỀ, HÀ NỘI

HẠNG MỤC / ITEM:
KIẾN TRÚC

HOÀN THÀNH / FINISHED DATE:	MÃ SỐ DỰ ÁN / PROJECT No:
TKCS	2501
HOÀN THÀNH / FINISHED DATE: 2026	PHIÊN BẢN / REVISION: 0

TÊN BẢN VẼ / SHEET NAME:
MẶT BẰNG TỔNG THỂ

SỐ HIỆU BẢN VẼ / SHEET NUMBER:
A-00.101

© 2025 - INNO.,jsc

BẢNG KÊ TỌA ĐỘ ĐỊNH VỊ MỐC RANH GIỚI KHU ĐẤT THEO HỆ TỌA ĐỘ VN - 2000		
Mốc	X	Y
01	2329536.0440	591806.5540
02	2329460.9740	591891.5140
03	2329452.8680	591890.6810
04	2329409.5230	591814.7660
05	2329410.6880	591803.4410
06	2329464.1030	591742.9880

BẢNG KÊ TỌA ĐỘ ĐỊNH VỊ CÔNG TRÌNH THEO HỆ TỌA ĐỘ VN - 2000		
N14	2329484.7646	591844.9559
N15	2329475.7721	591837.0102
N30	2329509.3001	591804.9173
N35	2329483.6503	591791.9614
N40	2329495.5689	591778.4726
N50	2329459.3582	591778.5828
N51	2329450.3686	591770.6338
N70	2329418.4301	591802.2304
N80	2329429.1697	591830.1744
N83	2329440.6755	591820.3243
N85	2329436.8683	591804.0168
N92	2329450.8151	591829.9355
N97	2329436.2271	591846.4034
N111	2329458.9399	591876.9845
N116	2329473.5279	591860.5166

CÔNG TY PHYTOPHARCO
(Kho bảo quản thuốc, bậc chịu lửa IV,
cấp nguy hiểm cháy S0, hạng sản xuất C

MẶT BẰNG ĐỊNH VỊ TẦNG 1
TL: 1 : 300

GHI CHÚ :
-TÒA 1: CỐT VỈA HÈ CÓ CAO ĐỘ TUYỆT ĐỐI TỪ +7.48 ĐẾN +7.69
-TÒA 2: CỐT VỈA HÈ CÓ CAO ĐỘ TUYỆT ĐỐI TỪ +6.81 ĐẾN +6.96
-TÒA 3: CỐT VỈA HÈ CÓ CAO ĐỘ TUYỆT ĐỐI TỪ +6.97.49 đến +7.77
-VỈA HÈ XUNG QUANH Ô ĐẤT DỰ ÁN CÓ CAO ĐỘ THẤP NHẤT LÀ +6.92 VÀ CAO ĐỘ CAO NHẤT LÀ +7.76

T1 THÁP 1	02 SẢNH ĐÓN TRẢ KHÁCH	06 SÂN CHƠI ĐA NĂNG
T2 THÁP 2	03 LỐI RA - VÀO HẦM	07 HỒ BƠI CHÍNH
T3 THÁP 3	04 KHU VỰC SẠC XE ĐIỆN	08 HỒ BƠI TRẺ EM
01 SẢNH CĂN HỘ	05 SÂN PICKLEBALL	09 KHU TẮM TRÁNG NGOÀI TRỜI
		10 KHU VỰC TẬP YOGA
SỐ TẦNG CAO		11 KHU VỰC TỔ CHỨC SỰ KIỆN

BÃI ĐỖ XE PCCC
CÁC GÓC BÃI ĐỖ SƠN PHẢN QUANG CÓ KẾT CẤU CHẮN PHÍA TRÊN

ĐƯỜNG CHO XE CHỮA CHÁY
TẢI TRỌNG PHÙ HỢP VỚI CÁC PHƯƠNG TIỆN PCCC VÀ CỨU NẠN CỦA ĐỊA PHƯƠNG
KHÔNG CÓ KẾT CẤU CHẮN PHÍA TRÊN

BÃI ĐỖ XE CHỮA CHÁY
BIỂN BÁO BÃI ĐỖ XE CHỮA CHÁY
(TẠI ĐIỂM ĐẦU VÀ CUỐI BÃI ĐỖ XE CHỮA CHÁY)

CHỈ GIỚI XÂY DỰNG

KHOẢNG LÙI XÂY DỰNG TỪ TẦNG 6 TRỞ LÊN

RANH GIỚI XÂY DỰNG PHẦN HẦM

CHỈ GIỚI ĐƯỜNG ĐỎ (TRÙNG VỚI RANH GIỚI KHU ĐẤT)

GHI CHÚ:
KHOẢNG KHÔNG GIỮA BÃI ĐỖ XE PCCC TỚI MÁI CANO[Y 2200MM KHÔNG CÓ CÂY XANH VÀ VẬT THỂ CỐ ĐỊNH.

PHIÊN BẢN	NỘI DUNG ĐIỀU CHỈNH	NGÀY NỘP

GHI CHÚ:

- CỐT +0.000 LẤY TẠI SÀN HOÀN THIỆN TẦNG 1 CÔNG TRÌNH TƯƠNG ĐƯƠNG COTE TUYỆT ĐỐI +7.900 (HỆ TỌA ĐỘ VN-2000)

- TÒA 1 CHIỀU CAO CÔNG TRÌNH TÍNH TỪ:
  + COTE HOÀN THIỆN +0.000: 43M
  + COTE NỀN TỰ NHIÊN THẤP NHẤT -1.000: 44M
- TÒA 2 CHIỀU CAO CÔNG TRÌNH TÍNH TỪ:
  + COTE HOÀN THIỆN +0.000: 50M
  + COTE NỀN TỰ NHIÊN THẤP NHẤT -1.000: 51M
- TÒA 3 CHIỀU CAO CÔNG TRÌNH TÍNH TỪ:
  + COTE HOÀN THIỆN +0.000: 59M
  + COTE NỀN TỰ NHIÊN THẤP NHẤT -1.000: 60M

- KHU VỰC TMDV BÀN GIAO THÔ, VỆ SINH KHÔNG XÂY, CHỈ BỐ TRÍ LAYOUT ĐỊNH HƯỚNG ĐẶT CÁC ĐẦU CHỜ.

- TỶ LỆ SỬ DỤNG VẬT LIỆU XANH KHÔNG NUNG ĐÁP ỨNG TỐI 90% KHỐI LƯỢNG GẠCH TRONG CÔNG TRÌNH

- TRONG PHÒNG RÁC KHÔNG BỐ TRÍ CÁC CHẤT, VẬT LIỆU CÓ KHẢ NĂNG GÂY CHÁY NỔ

- TƯỜNG NGĂN CHÁY, VÁCH NGĂN CHÁY TRONG CÁC GIAN PHÒNG ĐƯỢC NGĂN CHIA ĐẾN TRẦN BÊ TÔNG.

- VẬT LIỆU HOÀN THIỆN TRẦN, TƯỜNG, SÀN TRÊN CÁC ĐƯỜNG THOÁT NẠN, TRONG SẢNH THANG MÁY, SẢNH CHUNG, TẦNG KỸ THUẬT LÀ VẬT LIỆU KHÔNG CHÁY ĐẠT CV0

- TRONG CÁC KHÔNG GIAN TRẦN TREO KHÔNG BỐ TRÍ CÁC KÊNH, ĐƯỜNG ỐNG DẪN VẬN CHUYỂN CÁC CHẤT CHÁY DẠNG KHÍ, HỖN HỢP KHÍ, CHẤT LỎNG VÀ VẬT LIỆU CHÁY.

- TRONG CÔNG TRÌNH KHÔNG BỐ TRÍ TRẦN TREO CHO CÁC GIAN PHÒNG HẠNG A VÀ HẠNG B

- KHÔNG CÓ KÊNH, GIẾNG, ĐƯỜNG ỐNG ĐI QUA TƯỜNG NGĂN CHÁY LOẠI 1

CHỦ ĐẦU TƯ / OWNER:
CÔNG TY CỔ PHẦN THƯƠNG MẠI DƯƠNG PHÚC THẮNG
DUONG PHUC THANG TRADING JOINT STOCK COMPANY
ĐỊA CHỈ / ADDRESS:
Tầng 16, Tòa Cối Tower, Khu tây Hồ Tây, Phường Xuân Đỉnh, Thành phố Hà Nội, Việt Nam.
Hotline : 0243 2077 272

TƯ VẤN KIẾN TRÚC CHÍNH / MAIN ARCHITECTURAL CONSULTANT:
CÔNG TY TNHH KIẾN TRÚC DP VIỆT NAM
DP ARCHITECTS VIETNAM CO.,LTD.
ĐỊA CHỈ / ADDRESS:
Tầng 4, số 82 Võ Văn Tần, Phường Xuân Hòa, TP.Hồ Chí Minh
Hotline : 0283 5357 507
Fax: 0283 5357 517
Email : dparchitects@dpa.com.sg

TƯ VẤN THIẾT KẾ / CONSULTANT:
CÔNG TY CỔ PHẦN INNO
INNO.,JSC
ĐỊA CHỈ / ADDRESS
HN: 39 Thượng Thụy, Phú Thượng, Hà Nội
HCM: 37 Nguyễn Văn Hưởng, An Khánh, TP. HCM
Hotline: 0243 212 1776 Email : ad@innojsc.com

TỔNG GIÁM ĐỐC / GENERAL DIRECTOR:
ĐOÀN VĂN ĐỘNG
CHỦ NHIỆM THIẾT KẾ / PROJECT MANAGER:
LƯU GIANG NAM
CHỦ TRÌ THIẾT KẾ / DESIGN MANAGER:
NGÔ NGỌC BÌNH
KIỂM / CHECKED BY:
VŨ TUẤN ANH
THIẾT KẾ / DESIGNER
LÊ THỊ THANH **NGUYỄN XUÂN HIỆN**
PHƯƠNG THỊ ÁNH TUYẾT **VŨ TIẾN DƯƠNG**

TÊN DỰ ÁN / PROJECT NAME:
XÂY DỰNG NHÀ Ở TẠI LÔ ĐẤT NO-02

ĐỊA ĐIỂM XÂY DỰNG / PROJECT ADDRESS:
LÔ ĐẤT NO-22, PHƯỜNG BỒ ĐỀ, HÀ NỘI

HẠNG MỤC / ITEM:
KIẾN TRÚC

HOÀN THÀNH / FINISHED DATE:	MÃ SỐ DỰ ÁN / PROJECT No:
TKCS	2501
HOÀN THÀNH / FINISHED DATE: 2026	PHIÊN BẢN / REVISION: 0

TÊN BẢN VẼ / SHEET NAME:
MẶT BẰNG ĐỊNH VỊ TẦNG 1

SỐ HIỆU BẢN VẼ / SHEET NUMBER:
A-00.102

© 2025 - INNO.,JSC

PHIÊN BẢN	NỘI DUNG ĐIỀU CHỈNH	NGÀY NỘP
0	HỒ SƠ TKCS	../../2026

GHI CHÚ:

- CỐT +0.000 LẤY TẠI SÀN HOÀN THIỆN TẦNG 1 CÔNG TRÌNH TƯƠNG ĐƯƠNG COTE TUYỆT ĐỐI +7.900 (HỆ TỌA ĐỘ VN-2000)

- TÒA 1 CHIỀU CAO CÔNG TRÌNH TÍNH TỪ:
  + COTE HOÀN THIỆN +0.000: 43M
  + COTE NỀN TỰ NHIÊN THẤP NHẤT -1.000: 44M
- TÒA 2 CHIỀU CAO CÔNG TRÌNH TÍNH TỪ:
  + COTE HOÀN THIỆN +0.000: 50M
  + COTE NỀN TỰ NHIÊN THẤP NHẤT -1.000: 51M
- TÒA 3 CHIỀU CAO CÔNG TRÌNH TÍNH TỪ:
  + COTE HOÀN THIỆN +0.000: 59M
  + COTE NỀN TỰ NHIÊN THẤP NHẤT -1.000: 60M

- KHU VỰC TMDV BÀN GIAO THÔ, VỆ SINH KHÔNG XÂY, CHỈ BỐ TRÍ LAYOUT ĐỊNH HƯỚNG ĐẶT CÁC ĐẦU CHỜ.

- TỶ LỆ SỬ DỤNG VẬT LIỆU XANH KHÔNG NUNG ĐÁP ỨNG TỚI 90% KHỐI LƯỢNG GẠCH TRONG CÔNG TRÌNH

- TRONG PHÒNG RÁC KHÔNG BỐ TRÍ CÁC CHẤT, VẬT LIỆU CÓ KHẢ NĂNG GÂY CHÁY NỔ

- TƯỜNG NGĂN CHÁY, VÁCH NGĂN CHÁY TRONG CÁC GIAN PHÒNG ĐƯỢC NGĂN CHIA ĐẾN TRẦN BÊ TÔNG.

- VẬT LIỆU HOÀN THIỆN TRẦN, TƯỜNG, SÀN TRÊN CÁC ĐƯỜNG THOÁT NẠN, TRONG SẢNH THANG MÁY, SẢNH CHUNG, TẦNG KỸ THUẬT LÀ VẬT LIỆU KHÔNG CHÁY ĐẠT CV0

- TRONG CÁC KHÔNG GIAN TRẦN TREO KHÔNG BỐ TRÍ CÁC KÊNH, ĐƯỜNG ỐNG DẪN VẬN CHUYỂN CÁC CHẤT CHÁY DẠNG KHÍ, HỖN HỢP KHÍ, CHẤT LỎNG VÀ VẬT LIỆU CHÁY.

- TRONG CÔNG TRÌNH KHÔNG BỐ TRÍ TRẦN TREO CHO CÁC GIAN PHÒNG HẠNG A VÀ HẠNG B

- KHÔNG CÓ KÊNH, GIẾNG, ĐƯỜNG ỐNG ĐI QUA TƯỜNG NGĂN CHÁY LOẠI 1

GHI CHÚ:

- RANH GIỚI KHOANG CHÁY
- VỊ TRÍ THANG THOÁT NẠN
- KHOẢNG CÁCH THOÁT NẠN
- HƯỚNG THOÁT NẠN

- EV — VỊ TRÍ ĐỖ XE Ô TÔ ĐIỆN
- VỊ TRÍ ĐỖ XE Ô TÔ
- EV — VỊ TRÍ ĐỖ XE MÁY ĐIỆN
- VỊ TRÍ ĐỖ XE MÁY
- B — VỊ TRÍ ĐỖ XE ĐẠP

MẶT BẰNG TẦNG HẦM B1
TL: 1 : 200

CHỦ ĐẦU TƯ / OWNER:
CÔNG TY CỔ PHẦN THƯƠNG MẠI DƯƠNG PHÚC THẮNG
DUONG PHUC THANG TRADING JOINT STOCK COMPANY

ĐỊA CHỈ / ADDRESS:
Tầng 16, Tòa OSI Tower, Khu tây Hồ Tây, Phường Xuân Đỉnh, Thành phố Hà Nội, Việt Nam.
Hotline : 0243 2077 272

TƯ VẤN KIẾN TRÚC CHÍNH / MAIN ARCHITECTURAL CONSULTANT:
CÔNG TY TNHH KIẾN TRÚC DP VIỆT NAM
DP ARCHITECTS VIETNAM CO.,LTD.

ĐỊA CHỈ / ADDRESS:
Tầng 4, số 82 Võ Văn Tần, Phường Xuân Hòa, TP.Hồ Chí Minh
Hotline : 0283 5357 507
Fax: 0283 5357 517
Email : dparchitects@dpa.com.sg

TƯ VẤN THIẾT KẾ / CONSULTANT:
CÔNG TY CỔ PHẦN INNO
INNO.,JSC

ĐỊA CHỈ / ADDRESS
HN: 39 Thượng Thụy, Phú Thượng, Hà Nội
HCM: 37 Nguyễn Văn Hưởng, An Khánh, TP. HCM
Hotline: 0243 212 1776 Email : as@innojsc.com

TỔNG GIÁM ĐỐC / GENERAL DIRECTOR:
ĐOÀN VĂN ĐỘNG

CHỦ NHIỆM THIẾT KẾ / PROJECT MANAGER:
LƯU GIANG NAM

CHỦ TRÌ THIẾT KẾ / DESIGN MANAGER:
NGÔ NGỌC BÌNH

KIỂM / CHECKED BY:
VŨ TUẤN ANH

THIẾT KẾ / DESIGNER
LÊ THỊ THANH **NGUYỄN XUÂN HIỆN**
PHƯƠNG THỊ ÁNH TUYẾT **VŨ TIẾN DƯƠNG**

TÊN DỰ ÁN / PROJECT NAME:
XÂY DỰNG NHÀ Ở TẠI LÔ ĐẤT NO-02

ĐỊA ĐIỂM XÂY DỰNG / PROJECT ADDRESS:
LÔ ĐẤT NO-22, PHƯỜNG BỒ ĐỀ, HÀ NỘI

HẠNG MỤC / ITEM:
KIẾN TRÚC

HOÀN THÀNH / FINISHED DATE:	MÃ SỐ DỰ ÁN / PROJECT No:
TKCS	2501
HOÀN THÀNH / FINISHED DATE: 2026	PHIÊN BẢN / REVISION: 2

TÊN BẢN VẼ / SHEET NAME:
MẶT BẰNG TẦNG HẦM B1

SỐ HIỆU BẢN VẼ / SHEET NUMBER:
A0-01.101

© 2025 - INNO.,jsc

MẶT BẰNG TẦNG HẦM B2

TL: 1 : 200

GHI CHÚ:

- CỐT +0.000 LẤY TẠI SÀN HOÀN THIỆN TẦNG 1 CÔNG TRÌNH TƯƠNG ĐƯƠNG COTE TUYỆT ĐỐI +7.900 (HỆ TỌA ĐỘ VN-2000)
- TÒA 1 CHIỀU CAO CÔNG TRÌNH TÍNH TỪ:
  + COTE HOÀN THIỆN +0.000: 43M
  + COTE NỀN TỰ NHIÊN THẤP NHẤT -1.000: 44M
- TÒA 2 CHIỀU CAO CÔNG TRÌNH TÍNH TỪ:
  + COTE HOÀN THIỆN +0.000: 50M
  + COTE NỀN TỰ NHIÊN THẤP NHẤT -1.000: 51M
- TÒA 3 CHIỀU CAO CÔNG TRÌNH TÍNH TỪ:
  + COTE HOÀN THIỆN +0.000: 59M
  + COTE NỀN TỰ NHIÊN THẤP NHẤT -1.000: 60M
- KHU VỰC TMDV BÀN GIAO THÔ, VỆ SINH KHÔNG XÂY, CHỈ BỐ TRÍ LAYOUT ĐỊNH HƯỚNG ĐẶT CÁC ĐẦU CHỜ.
- TỶ LỆ SỬ DỤNG VẬT LIỆU XANH KHÔNG NUNG ĐÁP ỨNG TỐI 90% KHỐI LƯỢNG GẠCH TRONG CÔNG TRÌNH
- TRONG PHÒNG RÁC KHÔNG BỐ TRÍ CÁC CHẤT, VẬT LIỆU CÓ KHẢ NĂNG GÂY CHÁY NỔ
- TƯỜNG NGĂN CHÁY, VÁCH NGĂN CHÁY TRONG CÁC GIAN PHÒNG ĐƯỢC NGĂN CHIA ĐẾN TRẦN BÊ TÔNG.
- VẬT LIỆU HOÀN THIỆN TRẦN, TƯỜNG, SÀN TRÊN CÁC ĐƯỜNG THOÁT NẠN, TRONG SẢNH THANG MÁY, SẢNH CHUNG, TẦNG KỸ THUẬT LÀ VẬT LIỆU KHÔNG CHÁY ĐẠT CV0
- TRONG CÁC KHÔNG GIAN TRẦN TREO KHÔNG BỐ TRÍ CÁC KÊNH, ĐƯỜNG ỐNG DẪN VẬN CHUYỂN CÁC CHẤT CHÁY DẠNG KHÍ, HỖN HỢP KHÍ, CHẤT LỎNG VÀ VẬT LIỆU CHÁY.
- TRONG CÔNG TRÌNH KHÔNG BỐ TRÍ TRẦN TREO CHO CÁC GIAN PHÒNG HẠNG A VÀ HẠNG B
- KHÔNG CÓ KÊNH, GIẾNG, ĐƯỜNG ỐNG ĐI QUA TƯỜNG NGĂN CHÁY LOẠI 1

GHI CHÚ:

- RANH GIỚI KHOANG CHÁY
- VỊ TRÍ THANG THOÁT NẠN
- D — KHOẢNG CÁCH THOÁT NẠN
- HƯỚNG THOÁT NẠN
- EV — VỊ TRÍ ĐỖ XE Ô TÔ ĐIỆN
- VỊ TRÍ ĐỖ XE Ô TÔ
- EV — VỊ TRÍ ĐỖ XE MÁY ĐIỆN
- VỊ TRÍ ĐỖ XE MÁY
- B — VỊ TRÍ ĐỖ XE ĐẠP

PHIÊN BẢN	NỘI DUNG ĐIỀU CHỈNH	NGÀY NỘP
0	HỒ SƠ TKCS	../../2026

CHỦ ĐẦU TƯ / OWNER:
CÔNG TY CỔ PHẦN THƯƠNG MẠI DƯƠNG PHÚC THẮNG
DUONG PHUC THANG TRADING JOINT STOCK COMPANY
ĐỊA CHỈ / ADDRESS: Tầng 16, Tòa OSI Tower, Khu tây Hồ Tây, Phường Xuân Đỉnh, Thành phố Hà Nội, Việt Nam.
Hotline : 0243 2077 272

TƯ VẤN KIẾN TRÚC CHÍNH / MAIN ARCHITECTURAL CONSULTANT:
CÔNG TY TNHH KIẾN TRÚC DP VIỆT NAM
DP ARCHITECTS VIETNAM CO.,LTD.
ĐỊA CHỈ / ADDRESS: Tầng 4, số 82 Võ Văn Tần, Phường Xuân Hòa, TP.Hồ Chí Minh
Hotline : 0283 5357 507
Fax: 0283 5357 517
Email : dparchitects@dpa.com.sg

TƯ VẤN THIẾT KẾ / CONSULTANT:
CÔNG TY CỔ PHẦN INNO
INNO.,JSC
ĐỊA CHỈ / ADDRESS:
HN: 39 Thượng Thụy, Phú Thượng, Hà Nội
HCM: 37 Nguyễn Văn Hưởng, An Khánh, TP. HCM
Hotline: 0243 212 1776 Email : ad@innojsc.com

TỔNG GIÁM ĐỐC / GENERAL DIRECTOR: **ĐOÀN VĂN ĐỘNG**
CHỦ NHIỆM THIẾT KẾ / PROJECT MANAGER: **LƯU GIANG NAM**
CHỦ TRÌ THIẾT KẾ / DESIGN MANAGER: **NGÔ NGỌC BÌNH**
KIỂM / CHECKED BY: **VŨ TUẤN ANH**
THIẾT KẾ / DESIGNER: **LÊ THỊ THANH**, **NGUYỄN XUÂN HIỆN**, **PHƯƠNG THỊ ÁNH TUYẾT**, **VŨ TIẾN DƯƠNG**

TÊN DỰ ÁN / PROJECT NAME:
XÂY DỰNG NHÀ Ở TẠI LÔ ĐẤT NO-02

ĐỊA ĐIỂM XÂY DỰNG / PROJECT ADDRESS:
LÔ ĐẤT NO-22, PHƯỜNG BỒ ĐỀ, HÀ NỘI

HẠNG MỤC / ITEM: KIẾN TRÚC

HOÀN THÀNH / FINISHED DATE:	MÃ SỐ DỰ ÁN / PROJECT No:
TKCS	2501
HOÀN THÀNH / FINISHED DATE: 2026	PHIÊN BẢN / REVISION: 2

TÊN BẢN VẼ / SHEET NAME: **MẶT BẰNG TẦNG HẦM B2**

SỐ HIỆU BẢN VẼ / SHEET NUMBER: **A0-01.102**

© 2025 - INNO.,jsc

MẶT BẰNG: THÁP 1

© 2025 - INNO Jsc

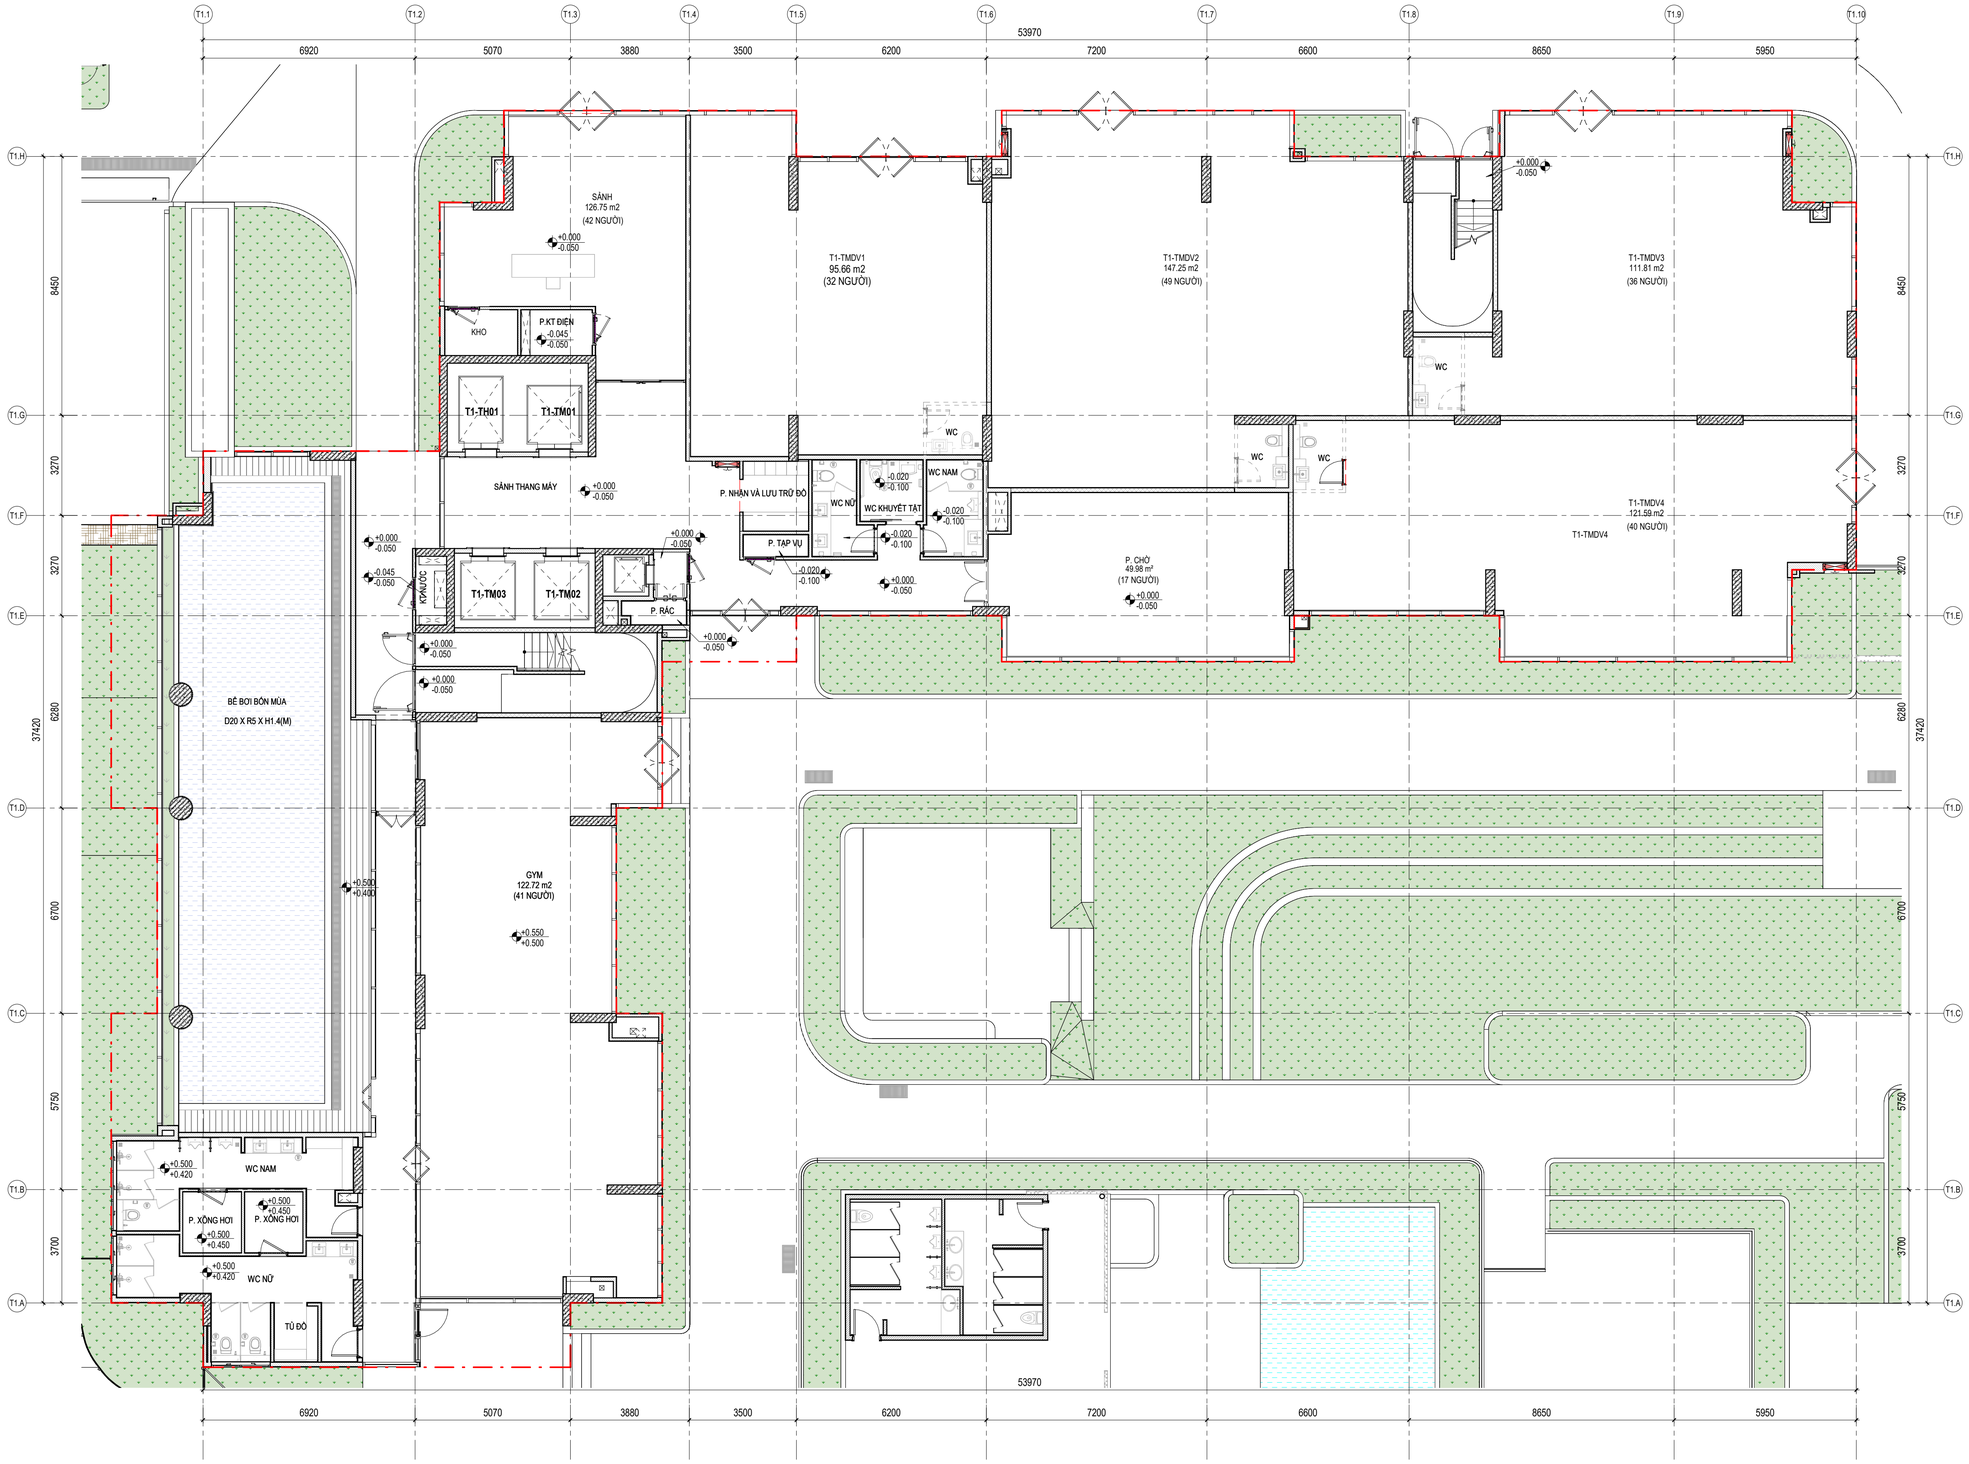

THỐNG KÊ DIỆN TÍCH TMDV TẦNG 1				
STT	TMDV	IFA(m²)	GFA(m²)	NSA(m²)
1	T1-TMDV1	100.84 m²	101.75 m²	95.66 m²
2	T1-TMDV2	153.72 m²	155.02 m²	147.25 m²
3	T1-TMDV3	117.28 m²	119.47 m²	111.81 m²
4	T1-TMDV4	127.76 m²	130.15 m²	121.59 m²
TỔNG		499.59 m²	506.40 m²	476.32 m²

MẶT BẰNG TẦNG 1

TL: 1 : 100

DIỆN TÍCH SÀN XÂY DỰNG (CFA) :1222.65 M2

PHIÊN BẢN	NỘI DUNG ĐIỀU CHỈNH	NGÀY NỘP

GHI CHÚ:

- CỐT +0.000 LẤY TẠI SÀN HOÀN THIỆN TẦNG 1 CÔNG TRÌNH TƯƠNG ĐƯƠNG COTE TUYỆT ĐỐI +7.900 (HỆ TỌA ĐỘ VN-2000)

- TÒA 1 CHIỀU CAO CÔNG TRÌNH TÍNH TỪ:
  + COTE HOÀN THIỆN +0.000: 43M
  + COTE NỀN TỰ NHIÊN THẤP NHẤT -1.000: 44M
- TÒA 2 CHIỀU CAO CÔNG TRÌNH TÍNH TỪ:
  + COTE HOÀN THIỆN +0.000: 50M
  + COTE NỀN TỰ NHIÊN THẤP NHẤT -1.000: 51M
- TÒA 3 CHIỀU CAO CÔNG TRÌNH TÍNH TỪ:
  + COTE HOÀN THIỆN +0.000: 59M
  + COTE NỀN TỰ NHIÊN THẤP NHẤT -1.000: 60M

- KHU VỰC TMDV BÀN GIAO THÔ, VỆ SINH KHÔNG XÂY, CHỈ BỐ TRÍ LAYOUT ĐỊNH HƯỚNG ĐẶT CÁC ĐẦU CHỜ.

- TỶ LỆ SỬ DỤNG VẬT LIỆU XANH KHÔNG NUNG ĐÁP ỨNG TỚI 90% KHỐI LƯỢNG GẠCH TRONG CÔNG TRÌNH

- TRONG PHÒNG RÁC KHÔNG BỐ TRÍ CÁC CHẤT, VẬT LIỆU CÓ KHẢ NĂNG GÂY CHÁY NỔ

- TƯỜNG NGĂN CHÁY, VÁCH NGĂN CHÁY TRONG CÁC GIAN PHÒNG ĐƯỢC NGĂN CHIA ĐẾN TRẦN BÊ TÔNG.

- VẬT LIỆU HOÀN THIỆN TRẦN, TƯỜNG, SÀN TRÊN CÁC ĐƯỜNG THOÁT NẠN, TRONG SẢNH THANG MÁY, SẢNH CHUNG, TẦNG KỸ THUẬT LÀ VẬT LIỆU KHÔNG CHÁY ĐẠT CV0

- TRONG CÁC KHÔNG GIAN TRẦN TREO KHÔNG BỐ TRÍ CÁC KÊNH, ĐƯỜNG ỐNG DẪN VẬN CHUYỂN CÁC CHẤT CHÁY DẠNG KHÍ, HỖN HỢP KHÍ, CHẤT LỎNG VÀ VẬT LIỆU CHÁY.

- TRONG CÔNG TRÌNH KHÔNG BỐ TRÍ TRẦN TREO CHO CÁC GIAN PHÒNG HẠNG A VÀ HẠNG B

- KHÔNG CÓ KÊNH, GIẾNG, ĐƯỜNG ỐNG ĐI QUA TƯỜNG NGĂN CHÁY LOẠI 1

CHỦ ĐẦU TƯ / OWNER:
CÔNG TY CỔ PHẦN THƯƠNG MẠI DƯƠNG PHÚC THẮNG
DUONG PHUC THANG TRADING JOINT STOCK COMPANY
ĐỊA CHỈ / ADDRESS:
Tầng 16, Tòa OSI Tower, Khu tây Hồ Tây, Phường Xuân Đỉnh, Thành phố Hà Nội, Việt Nam.
Hotline : 0243 2077 272

TƯ VẤN KIẾN TRÚC CHÍNH / MAIN ARCHITECTURAL CONSULTANT:
CÔNG TY TNHH KIẾN TRÚC DP VIỆT NAM
DP ARCHITECTS VIETNAM CO.,LTD.
ĐỊA CHỈ / ADDRESS:
Tầng 4, số 82 Võ Văn Tần, Phường Xuân Hòa, TP.Hồ Chí Minh
Hotline : 0283 5357 507
Fax: 0283 5357 517
Email : dparchitects@dpa.com.sg

TƯ VẤN THIẾT KẾ / CONSULTANT:
CÔNG TY CỔ PHẦN INNO
INNO.,JSC
ĐỊA CHỈ / ADDRESS:
HN: 39 Thượng Thụy, Phú Thượng, Hà Nội
HCM: 37 Nguyễn Văn Hưởng, An Khánh, TP. HCM
Hotline: 0243 212 1776 Email : ad@innojsc.com

TỔNG GIÁM ĐỐC / GENERAL DIRECTOR:
ĐOÀN VĂN ĐỘNG
CHỦ NHIỆM THIẾT KẾ / PROJECT MANAGER:
LƯU GIANG NAM
CHỦ TRÌ THIẾT KẾ / DESIGN MANAGER:
NGÔ NGỌC BÌNH
KIỂM / CHECKED BY:
VŨ TUẤN ANH
THIẾT KẾ / DESIGNER
LÊ THỊ THANH **NGUYỄN XUÂN HIỆN**
PHƯƠNG THỊ ÁNH TUYẾT **VŨ TIẾN DƯƠNG**

TÊN DỰ ÁN / PROJECT NAME:
XÂY DỰNG NHÀ Ở TẠI LÔ ĐẤT NO-02

ĐỊA ĐIỂM XÂY DỰNG / PROJECT ADDRESS:
LÔ ĐẤT NO-22, PHƯỜNG BỒ ĐỀ, HÀ NỘI

HẠNG MỤC / ITEM:
KIẾN TRÚC

HOÀN THÀNH / FINISHED DATE:	MÃ SỐ DỰ ÁN / PROJECT No:
TKCS	2501
HOÀN THÀNH / FINISHED DATE: 2026	PHIÊN BẢN / REVISION: 2

TÊN BẢN VẼ / SHEET NAME:
MẶT BẰNG TẦNG 1

SỐ HIỆU BẢN VẼ / SHEET NUMBER:
A.1-01.101

© 2025 - INNO.,jsc

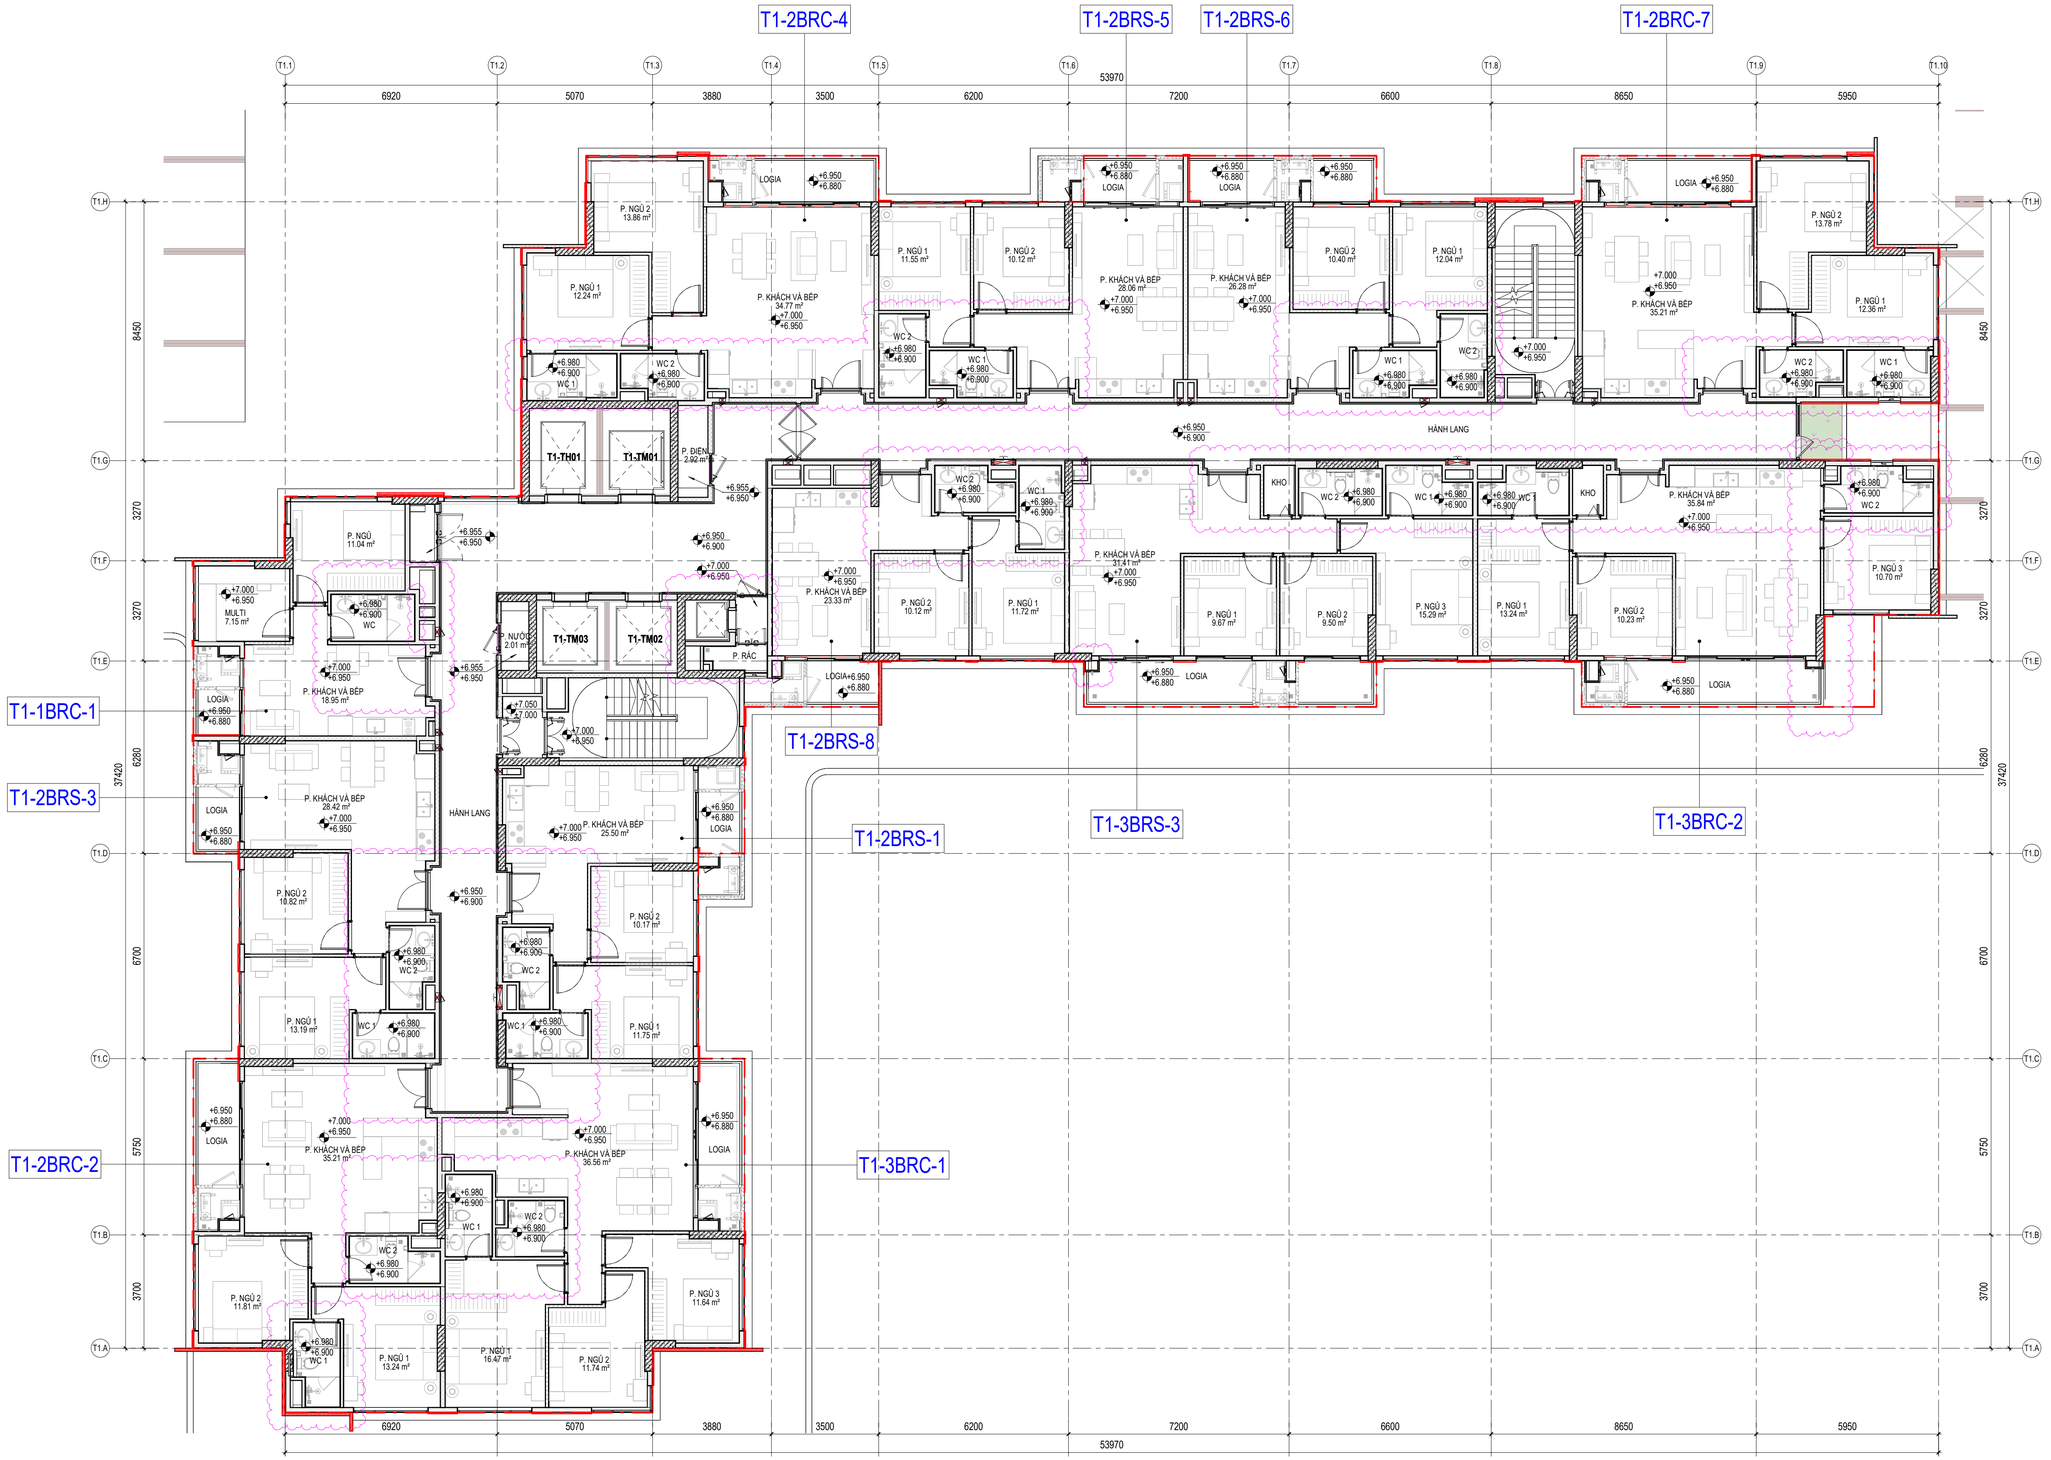

PHIÊN BẢN	NỘI DUNG ĐIỀU CHỈNH	NGÀY NỘP

GHI CHÚ:

- CỐT +0.000 LẤY TẠI SÀN HOÀN THIỆN TẦNG 1 CÔNG TRÌNH TƯƠNG ĐƯƠNG COTE TUYỆT ĐỐI +7.900 (HỆ TỌA ĐỘ VN-2000)

- TÒA 1 CHIỀU CAO CÔNG TRÌNH TÍNH TỪ:
  + COTE HOÀN THIỆN +0.000: 43M
  + COTE NỀN TỰ NHIÊN THẤP NHẤT -1.000: 44M
- TÒA 2 CHIỀU CAO CÔNG TRÌNH TÍNH TỪ:
  + COTE HOÀN THIỆN +0.000: 50M
  + COTE NỀN TỰ NHIÊN THẤP NHẤT -1.000: 51M
- TÒA 3 CHIỀU CAO CÔNG TRÌNH TÍNH TỪ:
  + COTE HOÀN THIỆN +0.000: 59M
  + COTE NỀN TỰ NHIÊN THẤP NHẤT -1.000: 60M

- KHU VỰC TMDV BÀN GIAO THÔ, VỆ SINH KHÔNG XÂY, CHỈ BỐ TRÍ LAYOUT ĐỊNH HƯỚNG ĐẶT CÁC ĐẦU CHỜ.

- TỶ LỆ SỬ DỤNG VẬT LIỆU XANH KHÔNG NUNG ĐÁP ỨNG TỐI 90% KHỐI LƯỢNG GẠCH TRONG CÔNG TRÌNH

- TRONG PHÒNG RÁC KHÔNG BỐ TRÍ CÁC CHẤT, VẬT LIỆU CÓ KHẢ NĂNG GÂY CHÁY NỔ

- TƯỜNG NGĂN CHÁY, VÁCH NGĂN CHÁY TRONG CÁC GIAN PHÒNG ĐƯỢC NGĂN CHIA ĐẾN TRẦN BÊ TÔNG.

- VẬT LIỆU HOÀN THIỆN TRẦN, TƯỜNG, SÀN TRÊN CÁC ĐƯỜNG THOÁT NẠN, TRONG SẢNH THANG MÁY, SẢNH CHUNG, TẦNG KỸ THUẬT LÀ VẬT LIỆU KHÔNG CHÁY ĐẠT CV0

- TRONG CÁC KHÔNG GIAN TRẦN TREO KHÔNG BỐ TRÍ CÁC KÊNH, ĐƯỜNG ỐNG DẪN VẬN CHUYỂN CÁC CHẤT CHÁY DẠNG KHÍ, HỖN HỢP KHÍ, CHẤT LỎNG VÀ VẬT LIỆU CHÁY.

- TRONG CÔNG TRÌNH KHÔNG BỐ TRÍ TRẦN TREO CHO CÁC GIAN PHÒNG HẠNG A VÀ HẠNG B

- KHÔNG CÓ KÊNH, GIẾNG, ĐƯỜNG ỐNG ĐI QUA TƯỜNG NGĂN CHÁY LOẠI 1

ỐP FACADE : LÀM VIỆC VỚI TƯ VẤN FACADE

THỐNG KÊ CHI TIẾT CĂN HỘ TĐH 01 (TẦNG 2-6)

STT	Tên căn hộ	Số lượng(căn)	Loại căn hộ(Phòng ngủ)	IFA(m²)	GFA(m²)	NSA(m²)	Số người
1	T1-1BRC-1	1	1PN	50.77 m²	51.93 m²	46.87 m²	2
2	T1-2BRS-1	1	2PN	66.35 m²	66.97 m²	61.31 m²	2
3	T1-2BRC-2	1	2PN	84.60 m²	85.88 m²	77.43 m²	3
4	T1-2BRS-3	1	2PN	72.53 m²	73.14 m²	66.61 m²	3
5	T1-2BRC-4	1	2PN	85.02 m²	86.28 m²	78.19 m²	3
6	T1-2BRS-5	1	2PN	69.29 m²	69.90 m²	64.75 m²	3
7	T1-2BRS-6	1	2PN	72.85 m²	73.27 m²	67.04 m²	3
8	T1-2BRC-7	1	3PN	85.08 m²	86.47 m²	79.21 m²	3
9	T1-2BRS-8	1	2PN	67.91 m²	65.76 m²	60.47 m²	2
10	T1-3BRC-1	1	3PN	101.77 m²	103.26 m²	95.26 m²	4
11	T1-3BRC-2	1	3PN	102.02 m²	103.34 m²	93.63 m²	4
12	T1-3BRS-3	1	3PN	99.38 m²	100.30 m²	91.52 m²	4
TỔNG		12		957.56 m²	966.51 m²	882.28 m²	36

MẶT BẰNG TẦNG 2

TL: 1 : 100

DIỆN TÍCH SÀN XÂY DỰNG (CFA) :1222.65 M2

CHỦ ĐẦU TƯ / OWNER:
CÔNG TY CỔ PHẦN THƯƠNG MẠI DƯƠNG PHÚC THẮNG
DUONG PHUC THANG TRADING JOINT STOCK COMPANY

ĐỊA CHỈ / ADDRESS:
Tầng 16, Tòa OSI Tower, Khu tây Hồ Tây, Phường Xuân Đỉnh, Thành phố Hà Nội, Việt Nam.
Hotline : 0243 2077 272

TƯ VẤN KIẾN TRÚC CHÍNH / MAIN ARCHITECTURAL CONSULTANT:
CÔNG TY TNHH KIẾN TRÚC DP VIỆT NAM
DP ARCHITECTS VIETNAM CO.,LTD.

ĐỊA CHỈ / ADDRESS:
Tầng 4, số 82 Võ Văn Tần, Phường Xuân Hòa, TP.Hồ Chí Minh
Hotline : 0283 5357 507
Fax: 0283 5357 517
Email : dparchitects@dpa.com.sg

TƯ VẤN THIẾT KẾ / CONSULTANT:
CÔNG TY CỔ PHẦN INNO
INNO.,JSC

ĐỊA CHỈ / ADDRESS:
HN: 39 Thượng Thụy, Phú Thượng, Hà Nội
HCM: 37 Nguyễn Văn Hưởng, An Khánh, TP. HCM
Hotline: 0243 212 1776 Email : ad@innojsc.com

TỔNG GIÁM ĐỐC / GENERAL DIRECTOR:
ĐOÀN VĂN ĐỘNG

CHỦ NHIỆM THIẾT KẾ / PROJECT MANAGER:
LƯU GIANG NAM

CHỦ TRÌ THIẾT KẾ / DESIGN MANAGER:
NGÔ NGỌC BÌNH

KIỂM / CHECKED BY:
VŨ TUẤN ANH

THIẾT KẾ / DESIGNER
LÊ THỊ THANH **NGUYỄN XUÂN HIỆN**
PHƯƠNG THỊ ÁNH TUYẾT **VŨ TIẾN DƯƠNG**

TÊN DỰ ÁN / PROJECT NAME:
XÂY DỰNG NHÀ Ở TẠI LÔ ĐẤT NO-02

ĐỊA ĐIỂM XÂY DỰNG / PROJECT ADDRESS:
LÔ ĐẤT NO-22, PHƯỜNG BỒ ĐỀ, HÀ NỘI

HẠNG MỤC / ITEM:
KIẾN TRÚC

HOÀN THÀNH / FINISHED DATE:	MÃ SỐ DỰ ÁN / PROJECT No:
TKCS	2501
HOÀN THÀNH / FINISHED DATE: 2026	PHIÊN BẢN / REVISION: 2

TÊN BẢN VẼ / SHEET NAME:
MẶT BẰNG TẦNG 2

SỐ HIỆU BẢN VẼ / SHEET NUMBER:
A.1-01.102

© 2025 - INNO.,jsc

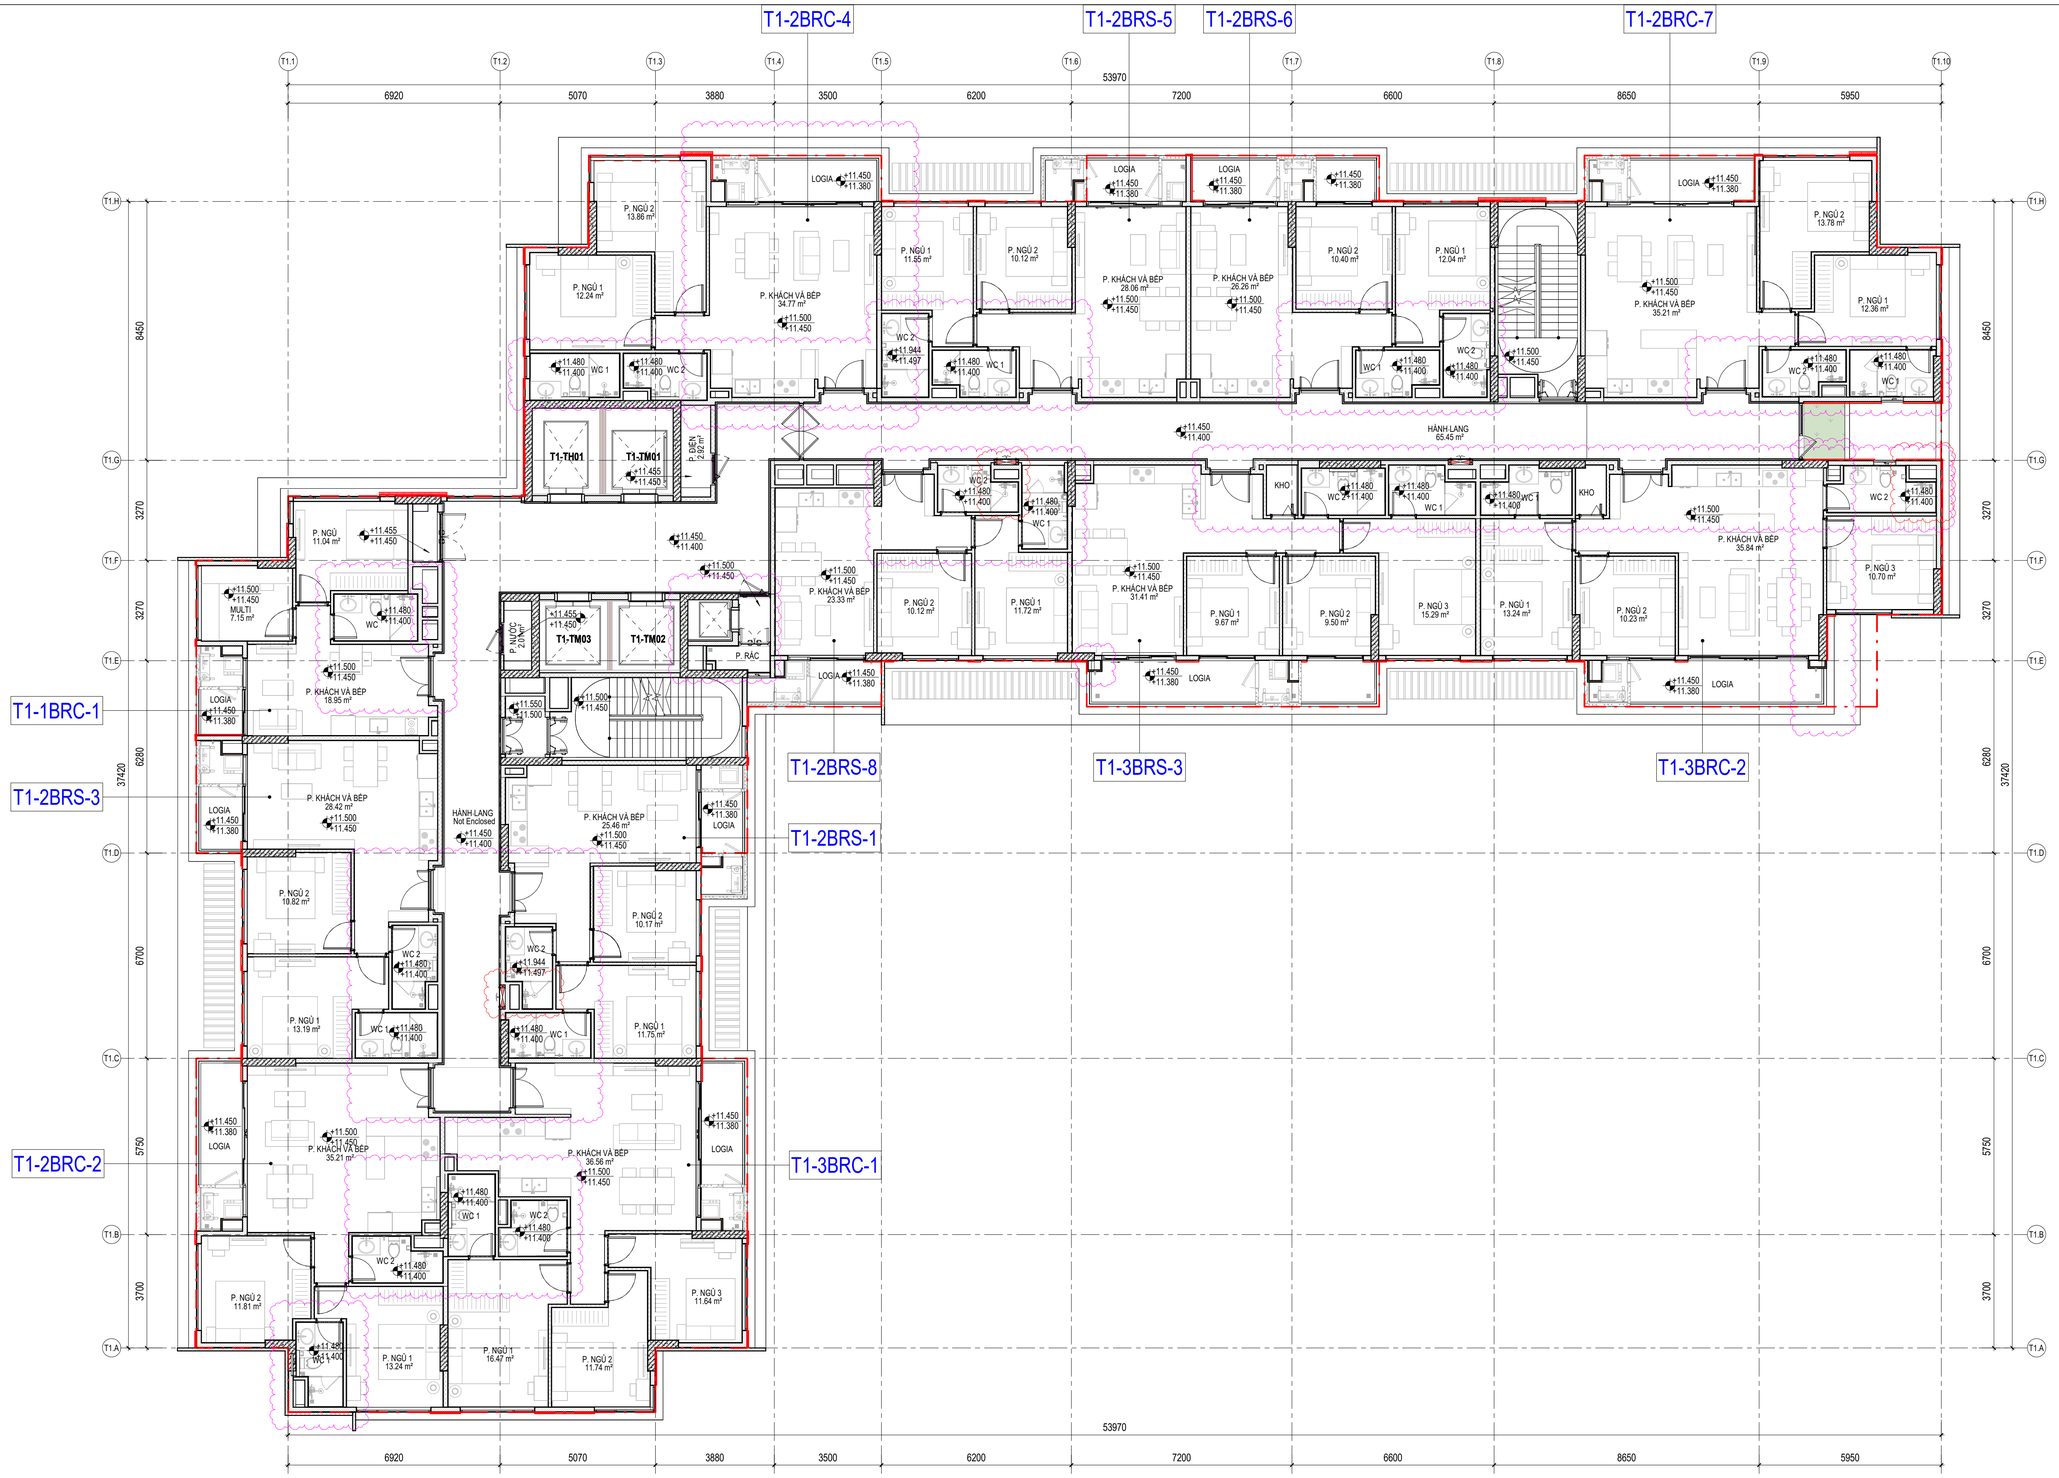

THỐNG KÊ CHI TIẾT CĂN HỘ TĐH 01 (TẦNG 2-6)							
STT	Tên căn hộ	Số lượng(căn)	Loại căn hộ(Phòng ngủ)	IFA(m²)	GFA(m²)	NSA(m²)	Số người
1	T1-1BRC-1	1	1PN	50.77 m²	51.93 m²	46.87 m²	2
2	T1-2BRS-1	1	2PN	66.35 m²	66.97 m²	61.31 m²	2
3	T1-2BRC-2	1	2PN	84.60 m²	85.88 m²	77.43 m²	3
4	T1-2BRS-3	1	2PN	72.53 m²	73.14 m²	66.61 m²	3
5	T1-2BRC-4	1	2PN	85.02 m²	86.28 m²	78.19 m²	3
6	T1-2BRS-5	1	2PN	69.29 m²	69.90 m²	64.75 m²	3
7	T1-2BRS-6	1	2PN	72.85 m²	73.27 m²	67.04 m²	3
8	T1-2BRC-7	1	3PN	85.08 m²	86.47 m²	79.21 m²	3
9	T1-2BRS-8	1	2PN	67.91 m²	65.76 m²	60.47 m²	2
10	T1-3BRC-1	1	3PN	101.77 m²	103.26 m²	95.26 m²	4
11	T1-3BRC-2	1	3PN	102.02 m²	103.34 m²	93.63 m²	4
12	T1-3BRS-3	1	3PN	99.38 m²	100.30 m²	91.52 m²	4
TỔNG		12		957.56 m²	966.51 m²	882.28 m²	36

MẶT BẰNG TẦNG 3-5

TL: 1 : 100

DIỆN TÍCH SÀN XÂY DỰNG (CFA) :1217.78 M2

PHIÊN BẢN	NỘI DUNG ĐIỀU CHỈNH	NGÀY NỘP

GHI CHÚ:

- CỐT +0.000 LẤY TẠI SÀN HOÀN THIỆN TẦNG 1 CÔNG TRÌNH TƯƠNG ĐƯƠNG COTE TUYỆT ĐỐI +7.900 (HỆ TỌA ĐỘ VN-2000)

- TÒA 1 CHIỀU CAO CÔNG TRÌNH TÍNH TỪ:
  + COTE HOÀN THIỆN +0.000: 43M
  + COTE NỀN TỰ NHIÊN THẤP NHẤT -1.000: 44M
- TÒA 2 CHIỀU CAO CÔNG TRÌNH TÍNH TỪ:
  + COTE HOÀN THIỆN +0.000: 50M
  + COTE NỀN TỰ NHIÊN THẤP NHẤT -1.000: 51M
- TÒA 3 CHIỀU CAO CÔNG TRÌNH TÍNH TỪ:
  + COTE HOÀN THIỆN +0.000: 59M
  + COTE NỀN TỰ NHIÊN THẤP NHẤT -1.000: 60M

- KHU VỰC TMDV BÀN GIAO THÔ, VỆ SINH KHÔNG XÂY, CHỈ BỐ TRÍ LAYOUT ĐỊNH HƯỚNG ĐẶT CÁC ĐẦU CHỜ.

- TỶ LỆ SỬ DỤNG VẬT LIỆU XANH KHÔNG NUNG ĐÁP ỨNG TỚI 90% KHỐI LƯỢNG GẠCH TRONG CÔNG TRÌNH

- TRONG PHÒNG RÁC KHÔNG BỐ TRÍ CÁC CHẤT, VẬT LIỆU CÓ KHẢ NĂNG GÂY CHÁY NỔ

- TƯỜNG NGĂN CHÁY, VÁCH NGĂN CHÁY TRONG CÁC GIAN PHÒNG ĐƯỢC NGĂN CHIA ĐẾN TRẦN BÊ TÔNG.

- VẬT LIỆU HOÀN THIỆN TRẦN, TƯỜNG, SÀN TRÊN CÁC ĐƯỜNG THOÁT NẠN, TRONG SẢNH THANG MÁY, SẢNH CHUNG, TẦNG KỸ THUẬT LÀ VẬT LIỆU KHÔNG CHÁY ĐẠT CV0

- TRONG CÁC KHÔNG GIAN TRẦN TREO KHÔNG BỐ TRÍ CÁC KÊNH, ĐƯỜNG ỐNG DẪN VẬN CHUYỂN CÁC CHẤT CHÁY DẠNG KHÍ, HỖN HỢP KHÍ, CHẤT LỎNG VÀ VẬT LIỆU CHÁY.

- TRONG CÔNG TRÌNH KHÔNG BỐ TRÍ TRẦN TREO CHO CÁC GIAN PHÒNG HẠNG A VÀ HẠNG B

- KHÔNG CÓ KÊNH, GIẾNG, ĐƯỜNG ỐNG ĐI QUA TƯỜNG NGĂN CHÁY LOẠI 1

ỐP FACADE : LÀM VIỆC VỚI TƯ VẤN FACADE

CHỦ ĐẦU TƯ / OWNER:
CÔNG TY CỔ PHẦN THƯƠNG MẠI DƯƠNG PHÚC THẮNG
DUONG PHUC THANG TRADING JOINT STOCK COMPANY
ĐỊA CHỈ / ADDRESS: Tầng 16, Toà OSI Tower, Khu tây Hồ Tây, Phường Xuân Đỉnh, Thành phố Hà Nội, Việt Nam.
Hotline : 0243 2077 272

TƯ VẤN KIẾN TRÚC CHÍNH / MAIN ARCHITECTURAL CONSULTANT:
CÔNG TY TNHH KIẾN TRÚC DP VIỆT NAM
DP ARCHITECTS VIETNAM CO.,LTD.
ĐỊA CHỈ / ADDRESS: Tầng 4, số 82 Võ Văn Tần, Phường Xuân Hòa, TP.Hồ Chí Minh
Hotline : 0283 5357 507
Fax: 0283 5357 517
Email : dparchitects@dpa.com.sg

TƯ VẤN THIẾT KẾ / CONSULTANT:
CÔNG TY CỔ PHẦN INNO
INNO.,JSC
ĐỊA CHỈ / ADDRESS: HN: 39 Thượng Thụy, Phú Thượng, Hà Nội
HCM: 37 Nguyễn Văn Hưởng, An Khánh, TP. HCM
Hotline: 0243 212 1776 Email : ad@innojsc.com

TỔNG GIÁM ĐỐC / GENERAL DIRECTOR:
ĐOÀN VĂN ĐỘNG
CHỦ NHIỆM THIẾT KẾ / PROJECT MANAGER:
LƯU GIANG NAM
CHỦ TRÌ THIẾT KẾ / DESIGN MANAGER:
NGÔ NGỌC BÌNH
KIỂM / CHECKED BY:
VŨ TUẤN ANH
THIẾT KẾ / DESIGNER
LÊ THỊ THANH **NGUYỄN XUÂN HIỆN**
PHƯƠNG THỊ ÁNH TUYẾT **VŨ TIẾN DƯƠNG**

TÊN DỰ ÁN / PROJECT NAME:
XÂY DỰNG NHÀ Ở TẠI LÔ ĐẤT NO-02

ĐỊA ĐIỂM XÂY DỰNG / PROJECT ADDRESS:
LÔ ĐẤT NO-22, PHƯỜNG BỒ ĐỀ, HÀ NỘI

HẠNG MỤC / ITEM:
KIẾN TRÚC

HOÀN THÀNH / FINISHED DATE:	MÃ SỐ DỰ ÁN / PROJECT No:
TKCS	2501
HOÀN THÀNH / FINISHED DATE: 2026	PHIÊN BẢN / REVISION: 3

TÊN BẢN VẼ / SHEET NAME:
MẶT BẰNG TẦNG 3-5

SỐ HIỆU BẢN VẼ / SHEET NUMBER:
A.1-01.103

© 2025 - INNO.,jsc

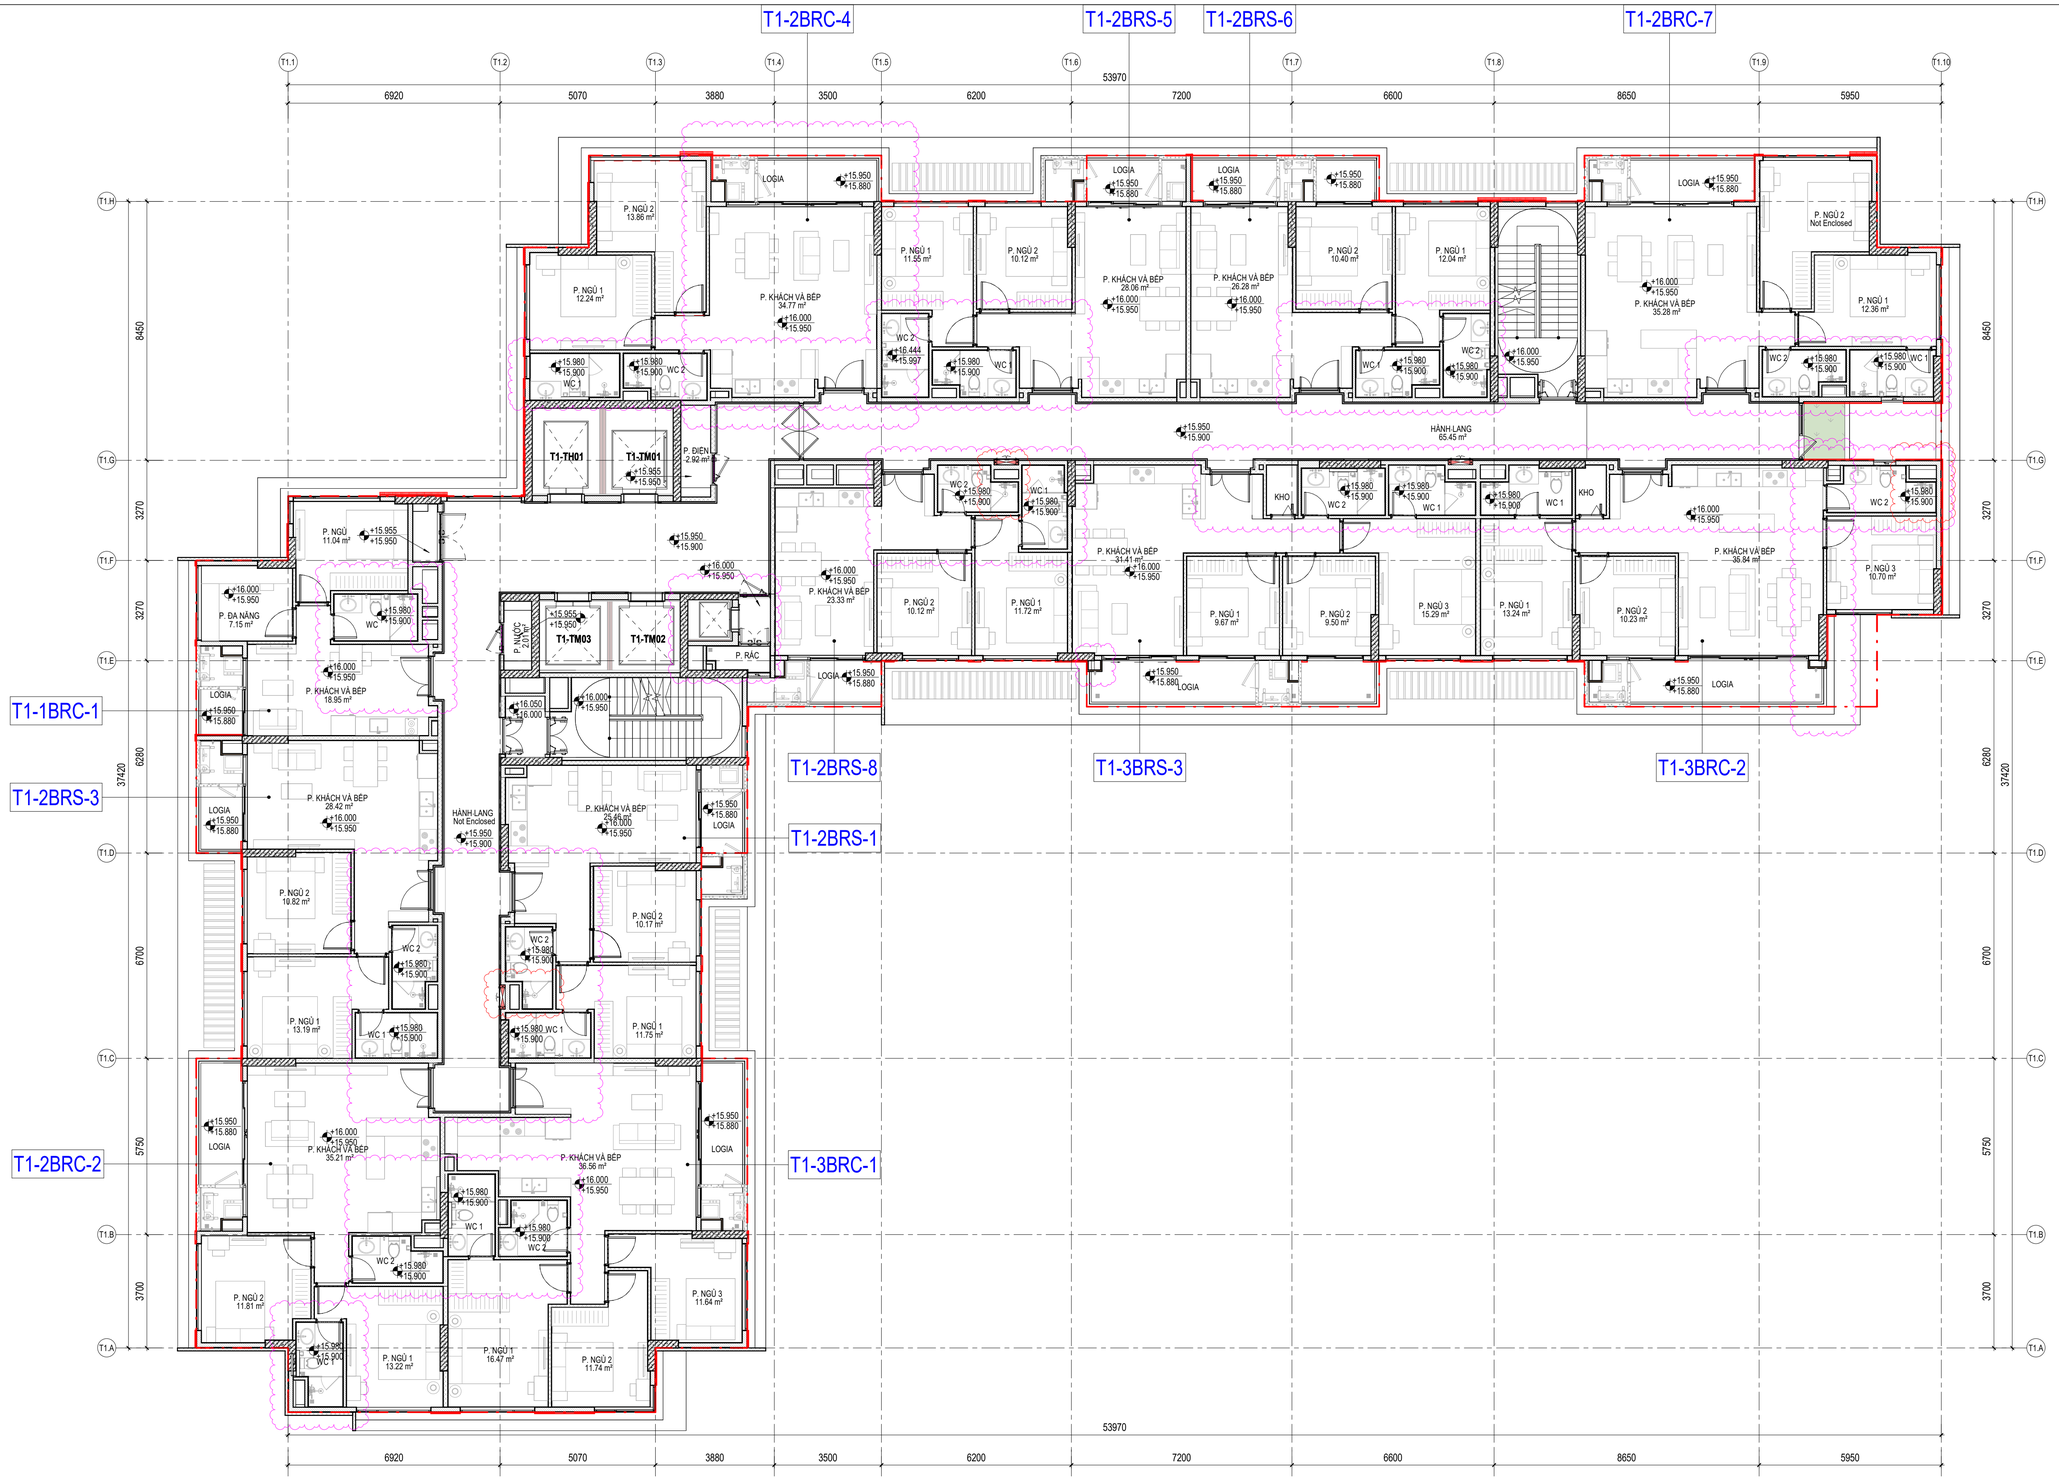

THỐNG KÊ CHI TIẾT CĂN HỘ TĐH 01 (TẦNG 2-6)							
STT	Tên căn hộ	Số lượng(căn)	Loại căn hộ(Phòng ngủ)	IFA(m²)	GFA(m²)	NSA(m²)	Số người
1	T1-1BRC-1	1	1PN	50.77 m²	51.93 m²	46.87 m²	2
2	T1-2BRS-1	1	2PN	66.35 m²	66.97 m²	61.31 m²	2
3	T1-2BRC-2	1	2PN	84.60 m²	85.88 m²	77.43 m²	3
4	T1-2BRS-3	1	2PN	72.53 m²	73.14 m²	66.61 m²	3
5	T1-2BRC-4	1	2PN	85.02 m²	86.28 m²	78.19 m²	3
6	T1-2BRS-5	1	2PN	69.29 m²	69.90 m²	64.75 m²	3
7	T1-2BRS-6	1	2PN	72.85 m²	73.27 m²	67.04 m²	3
8	T1-2BRC-7	1	3PN	85.08 m²	86.47 m²	79.21 m²	3
9	T1-2BRS-8	1	2PN	67.91 m²	65.76 m²	60.47 m²	2
10	T1-3BRC-1	1	3PN	101.77 m²	103.26 m²	95.26 m²	4
11	T1-3BRC-2	1	3PN	102.02 m²	103.34 m²	93.63 m²	4
12	T1-3BRS-3	1	3PN	99.38 m²	100.30 m²	91.52 m²	4
TỔNG		12		957.56 m²	966.51 m²	882.28 m²	36

MẶT BẰNG TẦNG 4-6

TL: 1 : 100

DIỆN TÍCH SÀN XÂY DỰNG (CFA) :1217.78 M2

PHIÊN BẢN	NỘI DUNG ĐIỀU CHỈNH	NGÀY NỘP

GHI CHÚ:

- CỐT +0.000 LẤY TẠI SÀN HOÀN THIỆN TẦNG 1 CÔNG TRÌNH TƯƠNG ĐƯƠNG COTE TUYỆT ĐỐI +7.900 (HỆ TỌA ĐỘ VN-2000)

- TÒA 1 CHIỀU CAO CÔNG TRÌNH TÍNH TỪ:
  + COTE HOÀN THIỆN +0.000: 43M
  + COTE NỀN TỰ NHIÊN THẤP NHẤT -1.000: 44M
- TÒA 2 CHIỀU CAO CÔNG TRÌNH TÍNH TỪ:
  + COTE HOÀN THIỆN +0.000: 50M
  + COTE NỀN TỰ NHIÊN THẤP NHẤT -1.000: 51M
- TÒA 3 CHIỀU CAO CÔNG TRÌNH TÍNH TỪ:
  + COTE HOÀN THIỆN +0.000: 59M
  + COTE NỀN TỰ NHIÊN THẤP NHẤT -1.000: 60M

- KHU VỰC TMDV BÀN GIAO THÔ, VỆ SINH KHÔNG XÂY, CHỈ BỐ TRÍ LAYOUT ĐỊNH HƯỚNG ĐẶT CÁC ĐẦU CHỜ.

- TỶ LỆ SỬ DỤNG VẬT LIỆU XANH KHÔNG NUNG ĐÁP ỨNG TỚI 90% KHỐI LƯỢNG GẠCH TRONG CÔNG TRÌNH

- TRONG PHÒNG RÁC KHÔNG BỐ TRÍ CÁC CHẤT, VẬT LIỆU CÓ KHẢ NĂNG GÂY CHÁY NỔ

- TƯỜNG NGĂN CHÁY, VÁCH NGĂN CHÁY TRONG CÁC GIAN PHÒNG ĐƯỢC NGĂN CHIA ĐẾN TRẦN BÊ TÔNG.

- VẬT LIỆU HOÀN THIỆN TRẦN, TƯỜNG, SÀN TRÊN CÁC ĐƯỜNG THOÁT NẠN, TRONG SẢNH THANG MÁY, SẢNH CHUNG, TẦNG KỸ THUẬT LÀ VẬT LIỆU KHÔNG CHÁY ĐẠT CV0

- TRONG CÁC KHÔNG GIAN TRẦN TREO KHÔNG BỐ TRÍ CÁC KÊNH, ĐƯỜNG ỐNG DẪN VẬN CHUYỂN CÁC CHẤT CHÁY DẠNG KHÍ, HỖN HỢP KHÍ, CHẤT LỎNG VÀ VẬT LIỆU CHÁY.

- TRONG CÔNG TRÌNH KHÔNG BỐ TRÍ TRẦN TREO CHO CÁC GIAN PHÒNG HẠNG A VÀ HẠNG B

- KHÔNG CÓ KÊNH, GIẾNG, ĐƯỜNG ỐNG ĐI QUA TƯỜNG NGĂN CHÁY LOẠI 1

ỐP FACADE : LÀM VIỆC VỚI TƯ VẤN FACADE

CHỦ ĐẦU TƯ / OWNER:
CÔNG TY CỔ PHẦN THƯƠNG MẠI DƯƠNG PHÚC THẮNG
DUONG PHUC THANG TRADING JOINT STOCK COMPANY

ĐỊA CHỈ / ADDRESS:
Tầng 16, Tòa OSI Tower, Khu tây Hồ Tây, Phường Xuân Đỉnh, Thành phố Hà Nội, Việt Nam.
Hotline : 0243 2077 272

TƯ VẤN KIẾN TRÚC CHÍNH / MAIN ARCHITECTURAL CONSULTANT:
CÔNG TY TNHH KIẾN TRÚC DP VIỆT NAM
DP ARCHITECTS VIETNAM CO.,LTD.

ĐỊA CHỈ / ADDRESS:
Tầng 4, số 82 Võ Văn Tần, Phường Xuân Hòa, TP.Hồ Chí Minh
Hotline : 0283 5357 507
Fax: 0283 5357 517
Email : dparchitects@dpa.com.sg

TƯ VẤN THIẾT KẾ / CONSULTANT:
CÔNG TY CỔ PHẦN INNO
INNO.,JSC

ĐỊA CHỈ / ADDRESS
HN: 39 Thượng Thụy, Phú Thượng, Hà Nội
HCM: 37 Nguyễn Văn Hưởng, An Khánh, TP. HCM
Hotline: 0243 212 1776 Email : ad@innojsc.com

TỔNG GIÁM ĐỐC / GENERAL DIRECTOR:
ĐOÀN VĂN ĐỘNG

CHỦ NHIỆM THIẾT KẾ / PROJECT MANAGER:
LƯU GIANG NAM

CHỦ TRÌ THIẾT KẾ / DESIGN MANAGER:
NGÔ NGỌC BÌNH

KIỂM / CHECKED BY:
VŨ TUẤN ANH

THIẾT KẾ / DESIGNER
LÊ THỊ THANH **NGUYỄN XUÂN HIỆN**
PHƯƠNG THỊ ÁNH TUYẾT **VŨ TIẾN DƯƠNG**

TÊN DỰ ÁN / PROJECT NAME:
XÂY DỰNG NHÀ Ở TẠI LÔ ĐẤT NO-02

ĐỊA ĐIỂM XÂY DỰNG / PROJECT ADDRESS:
LÔ ĐẤT NO-22, PHƯỜNG BỒ ĐỀ, HÀ NỘI

HẠNG MỤC / ITEM:
KIẾN TRÚC

HOÀN THÀNH / FINISHED DATE:	MÃ SỐ DỰ ÁN / PROJECT No:
TKCS	2501
HOÀN THÀNH / FINISHED DATE: 2026	PHIÊN BẢN / REVISION: 3

TÊN BẢN VẼ / SHEET NAME:
MẶT BẰNG TẦNG 4-6

SỐ HIỆU BẢN VẼ / SHEET NUMBER:
A.1-01.104

© 2025 - INNO.,JSC

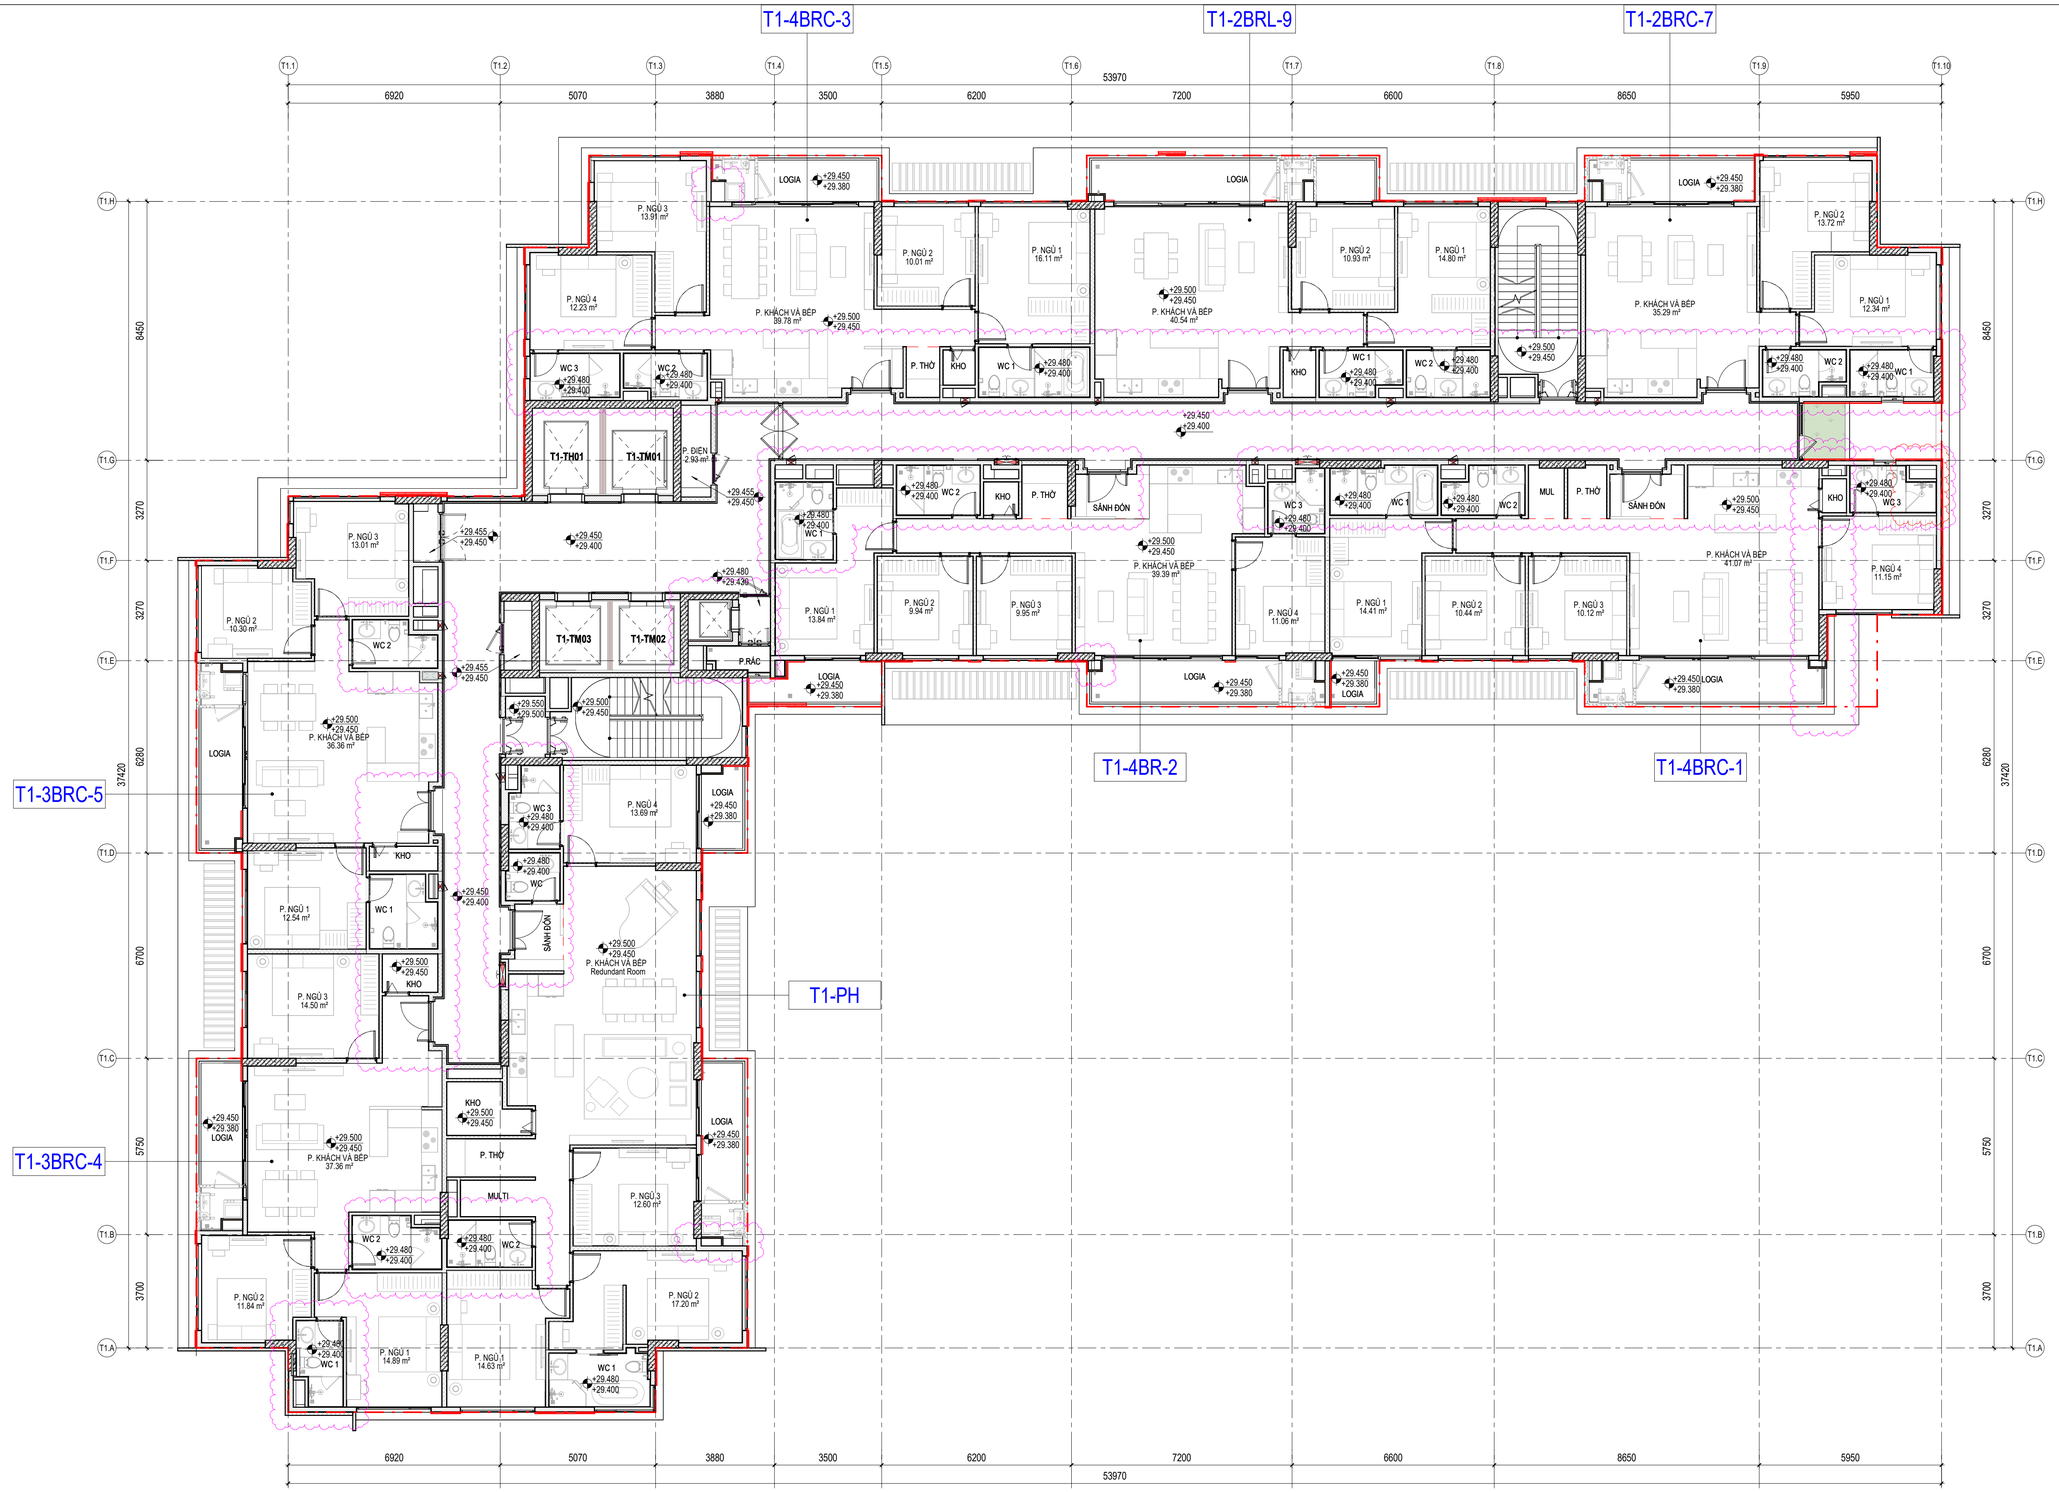

THỐNG KÊ CHI TIẾT CĂN HỘ TĐH 02 (TẦNG 7)							
STT	Tên căn hộ	Số lượng(căn)	Loại căn hộ(Phòng ngủ)	IFA(m²)	GFA(m²)	NSA(m²)	Số người
1	T1-2BRL-9	1	2PN	98.24 m²	98.57 m²	90.50 m²	3
2	T1-2BRC-7	1	2PN	85.06 m²	86.46 m²	79.11 m²	3
3	T1-3BRC-4	1	3PN	107.61 m²	109.25 m²	100.27 m²	4
4	T1-3BRC-5	1	3PN	100.93 m²	102.42 m²	93.38 m²	4
5	T1-4BRC-1	1	4PN	136.02 m²	137.66 m²	125.66 m²	5
6	T1-4BR-2	1	4PN	133.87 m²	134.52 m²	120.72 m²	5
7	T1-4BRC-3	1	4PN	129.50 m²	131.49 m²	120.27 m²	5
8	T1-PH	1	PH	170.90 m²	172.81 m²	159.49 m²	5
TỔNG		8		962.12 m²	973.16 m²	889.40 m²	34

MẶT BẰNG TẦNG 7

TL: 1 : 100

DIỆN TÍCH SÀN XÂY DỰNG (CFA) :1217.78 M2

PHIÊN BẢN	NỘI DUNG ĐIỀU CHỈNH	NGÀY NỘP

GHI CHÚ:

- CỐT +0.000 LẤY TẠI SÀN HOÀN THIỆN TẦNG 1 CÔNG TRÌNH TƯƠNG ĐƯƠNG COTE TUYỆT ĐỐI +7.900 (HỆ TỌA ĐỘ VN-2000)

- TÒA 1 CHIỀU CAO CÔNG TRÌNH TÍNH TỪ:
  + COTE HOÀN THIỆN +0.000: 43M
  + COTE NỀN TỰ NHIÊN THẤP NHẤT -1.000: 44M
- TÒA 2 CHIỀU CAO CÔNG TRÌNH TÍNH TỪ:
  + COTE HOÀN THIỆN +0.000: 50M
  + COTE NỀN TỰ NHIÊN THẤP NHẤT -1.000: 51M
- TÒA 3 CHIỀU CAO CÔNG TRÌNH TÍNH TỪ:
  + COTE HOÀN THIỆN +0.000: 59M
  + COTE NỀN TỰ NHIÊN THẤP NHẤT -1.000: 60M

- KHU VỰC TMDV BÀN GIAO THÔ, VỆ SINH KHÔNG XÂY, CHỈ BỐ TRÍ LAYOUT ĐỊNH HƯỚNG ĐẶT CÁC ĐẦU CHỜ.

- TỶ LỆ SỬ DỤNG VẬT LIỆU XANH KHÔNG NUNG ĐÁP ỨNG TỐI 90% KHỐI LƯỢNG GẠCH TRONG CÔNG TRÌNH

- TRONG PHÒNG RÁC KHÔNG BỐ TRÍ CÁC CHẤT, VẬT LIỆU CÓ KHẢ NĂNG GÂY CHÁY NỔ

- TƯỜNG NGĂN CHÁY, VÁCH NGĂN CHÁY TRONG CÁC GIAN PHÒNG ĐƯỢC NGĂN CHIA ĐẾN TRẦN BÊ TÔNG.

- VẬT LIỆU HOÀN THIỆN TRẦN, TƯỜNG, SÀN TRÊN CÁC ĐƯỜNG THOÁT NẠN, TRONG SẢNH THANG MÁY, SẢNH CHUNG, TẦNG KỸ THUẬT LÀ VẬT LIỆU KHÔNG CHÁY ĐẠT CV0

- TRONG CÁC KHÔNG GIAN TRẦN TREO KHÔNG BỐ TRÍ CÁC KÊNH, ĐƯỜNG ỐNG DẪN VẬN CHUYỂN CÁC CHẤT CHÁY DẠNG KHÍ, HỖN HỢP KHÍ, CHẤT LỎNG VÀ VẬT LIỆU CHÁY.

- TRONG CÔNG TRÌNH KHÔNG BỐ TRÍ TRẦN TREO CHO CÁC GIAN PHÒNG HẠNG A VÀ HẠNG B

- KHÔNG CÓ KÊNH, GIẾNG, ĐƯỜNG ỐNG ĐI QUA TƯỜNG NGĂN CHÁY LOẠI 1

ỐP FACADE : LÀM VIỆC VỚI TƯ VẤN FACADE

CHỦ ĐẦU TƯ / OWNER:
CÔNG TY CỔ PHẦN THƯƠNG MẠI DƯƠNG PHÚC THẮNG
DUONG PHUC THANG TRADING JOINT STOCK COMPANY
ĐỊA CHỈ / ADDRESS: Tầng 16, Toà OSI Tower, Khu tây Hồ Tây, Phường Xuân Đỉnh, Thành phố Hà Nội, Việt Nam.
Hotline : 0243 2077 272

TƯ VẤN KIẾN TRÚC CHÍNH / MAIN ARCHITECTURAL CONSULTANT:
CÔNG TY TNHH KIẾN TRÚC DP VIỆT NAM
DP ARCHITECTS VIETNAM CO.,LTD.
ĐỊA CHỈ / ADDRESS: Tầng 4, số 82 Võ Văn Tần, Phường Xuân Hòa, TP.Hồ Chí Minh
Hotline : 0283 5357 507
Fax: 0283 5357 517
Email : dparchitects@dpa.com.sg

TƯ VẤN THIẾT KẾ / CONSULTANT:
CÔNG TY CỔ PHẦN INNO
INNO.,JSC
ĐỊA CHỈ / ADDRESS: HN: 39 Thượng Thụy, Phú Thượng, Hà Nội
HCM: 37 Nguyễn Văn Hưởng, An Khánh, TP. HCM
Hotline: 0243 212 1776 Email : ad@innojsc.com

TỔNG GIÁM ĐỐC / GENERAL DIRECTOR: **ĐOÀN VĂN ĐỘNG**
CHỦ NHIỆM THIẾT KẾ / PROJECT MANAGER: **LƯU GIANG NAM**
CHỦ TRÌ THIẾT KẾ / DESIGN MANAGER: **NGÔ NGỌC BÌNH**
KIỂM / CHECKED BY: **VŨ TUẤN ANH**
THIẾT KẾ / DESIGNER: **LÊ THỊ THANH**, **NGUYỄN XUÂN HIỆN**, **PHƯƠNG THỊ ÁNH TUYẾT**, **VŨ TIẾN DƯƠNG**

TÊN DỰ ÁN / PROJECT NAME:
XÂY DỰNG NHÀ Ở TẠI LÔ ĐẤT NO-02

ĐỊA ĐIỂM XÂY DỰNG / PROJECT ADDRESS:
LÔ ĐẤT NO-22, PHƯỜNG BỒ ĐỀ, HÀ NỘI

HẠNG MỤC / ITEM: KIẾN TRÚC

HOÀN THÀNH / FINISHED DATE:	MÃ SỐ DỰ ÁN / PROJECT No:
TKCS	2501
HOÀN THÀNH / FINISHED DATE: 2026	PHIÊN BẢN / REVISION: 3

TÊN BẢN VẼ / SHEET NAME: **MẶT BẰNG TẦNG 7**

SỐ HIỆU BẢN VẼ / SHEET NUMBER: **A.1-01.105**

© 2025 - INNO.,jsc

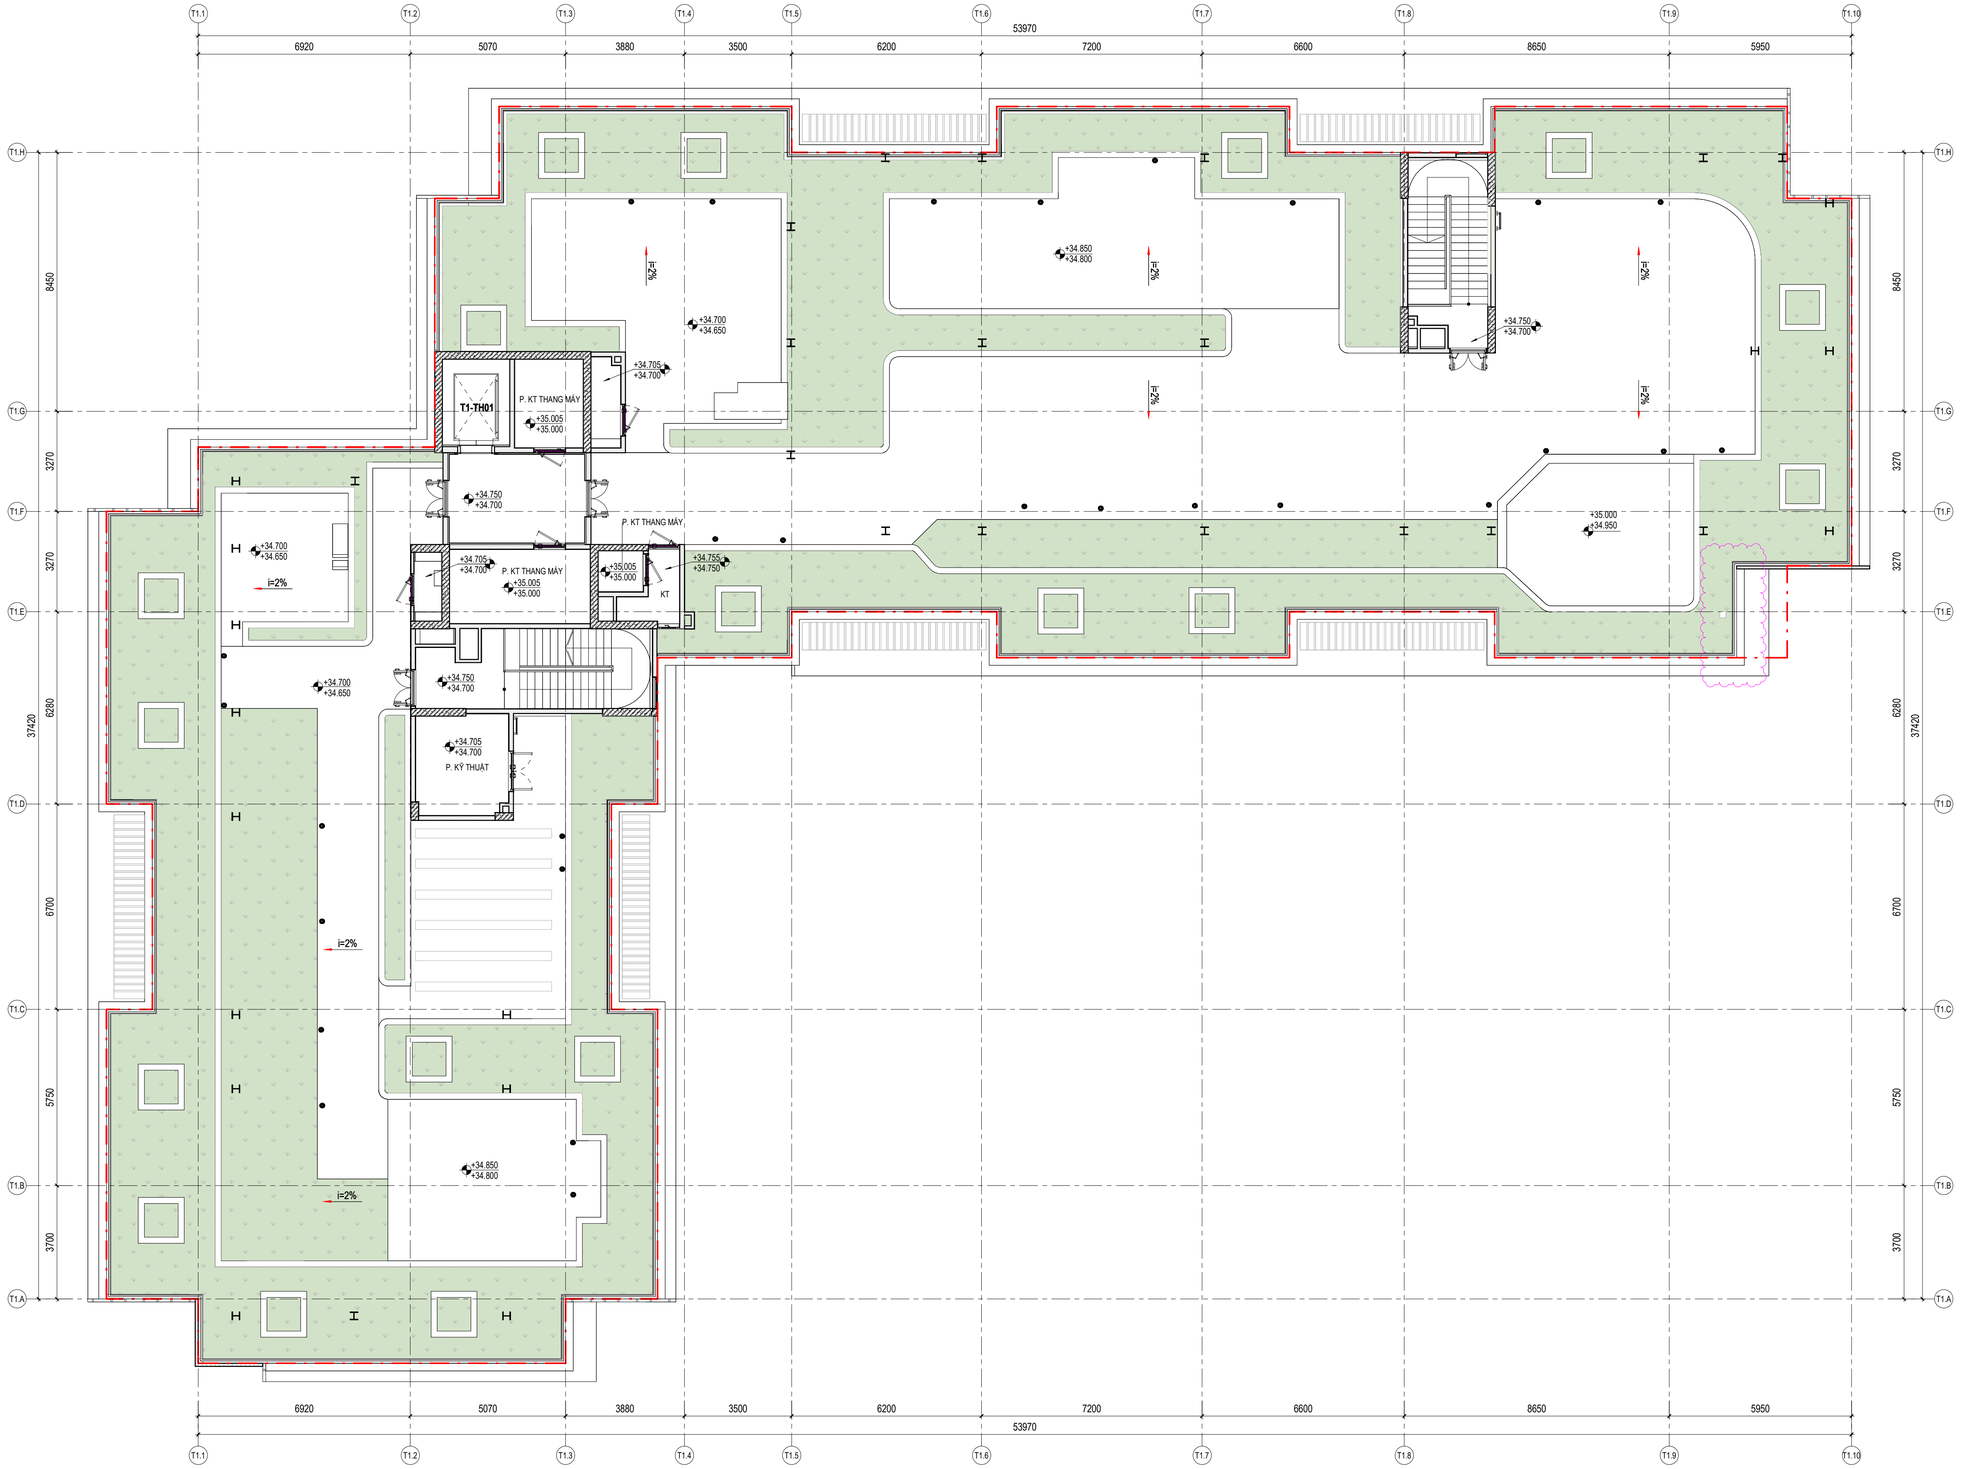

MẶT BẰNG TẦNG TUM
TL: 1 : 100

PHIÊN BẢN	NỘI DUNG ĐIỀU CHỈNH	NGÀY NỘP

GHI CHÚ:

- CỐT +0.000 LẤY TẠI SÀN HOÀN THIỆN TẦNG 1 CÔNG TRÌNH TƯƠNG ĐƯƠNG COTE TUYỆT ĐỐI +7.900 (HỆ TỌA ĐỘ VN-2000)

- TÒA 1 CHIỀU CAO CÔNG TRÌNH TÍNH TỪ:
  + COTE HOÀN THIỆN +0.000: 43M
  + COTE NỀN TỰ NHIÊN THẤP NHẤT -1.000: 44M
- TÒA 2 CHIỀU CAO CÔNG TRÌNH TÍNH TỪ:
  + COTE HOÀN THIỆN +0.000: 50M
  + COTE NỀN TỰ NHIÊN THẤP NHẤT -1.000: 51M
- TÒA 3 CHIỀU CAO CÔNG TRÌNH TÍNH TỪ:
  + COTE HOÀN THIỆN +0.000: 59M
  + COTE NỀN TỰ NHIÊN THẤP NHẤT -1.000: 60M

- KHU VỰC TMDV BÀN GIAO THÔ, VỆ SINH KHÔNG XÂY, CHỈ BỐ TRÍ LAYOUT ĐỊNH HƯỚNG ĐẶT CÁC ĐẦU CHỜ.

- TỶ LỆ SỬ DỤNG VẬT LIỆU XANH KHÔNG NUNG ĐÁP ỨNG TỚI 90% KHỐI LƯỢNG GẠCH TRONG CÔNG TRÌNH

- TRONG PHÒNG RÁC KHÔNG BỐ TRÍ CÁC CHẤT, VẬT LIỆU CÓ KHẢ NĂNG GÂY CHÁY NỔ

- TƯỜNG NGĂN CHÁY, VÁCH NGĂN CHÁY TRONG CÁC GIAN PHÒNG ĐƯỢC NGĂN CHIA ĐẾN TRẦN BÊ TÔNG.

- VẬT LIỆU HOÀN THIỆN TRẦN, TƯỜNG, SÀN TRÊN CÁC ĐƯỜNG THOÁT NẠN, TRONG SẢNH THANG MÁY, SẢNH CHUNG, TẦNG KỸ THUẬT LÀ VẬT LIỆU KHÔNG CHÁY ĐẠT CV0

- TRONG CÁC KHÔNG GIAN TRẦN TREO KHÔNG BỐ TRÍ CÁC KÊNH, ĐƯỜNG ỐNG DẪN VẬN CHUYỂN CÁC CHẤT CHÁY DẠNG KHÍ, HỖN HỢP KHÍ, CHẤT LỎNG VÀ VẬT LIỆU CHÁY.

- TRONG CÔNG TRÌNH KHÔNG BỐ TRÍ TRẦN TREO CHO CÁC GIAN PHÒNG HẠNG A VÀ HẠNG B

- KHÔNG CÓ KÊNH, GIẾNG, ĐƯỜNG ỐNG ĐI QUA TƯỜNG NGĂN CHÁY LOẠI 1

CHỦ ĐẦU TƯ / OWNER:
CÔNG TY CỔ PHẦN THƯƠNG MẠI DƯƠNG PHÚC THẮNG
DUONG PHUC THANG TRADING JOINT STOCK COMPANY

ĐỊA CHỈ / ADDRESS:
Tầng 16, Tòa OSI Tower, Khu tây Hồ Tây, Phường Xuân Đỉnh, Thành phố Hà Nội, Việt Nam.
Hotline : 0243 2077 272

TƯ VẤN KIẾN TRÚC CHÍNH / MAIN ARCHITECTURAL CONSULTANT:
CÔNG TY TNHH KIẾN TRÚC DP VIỆT NAM
DP ARCHITECTS VIETNAM CO.,LTD.

ĐỊA CHỈ / ADDRESS:
Tầng 4, số 82 Võ Văn Tần, Phường Xuân Hòa, TP.Hồ Chí Minh
Hotline : 0283 5357 507
Fax: 0283 5357 517
Email : dparchitects@dpa.com.sg

TƯ VẤN THIẾT KẾ / CONSULTANT:
CÔNG TY CỔ PHẦN INNO
INNO.,JSC

ĐỊA CHỈ / ADDRESS:
HN: 39 Thượng Thụy, Phú Thượng, Hà Nội
HCM: 37 Nguyễn Văn Hưởng, An Khánh, TP. HCM
Hotline: 0243 212 1776 Email : ad@innojsc.com

TỔNG GIÁM ĐỐC / GENERAL DIRECTOR:
ĐOÀN VĂN ĐỘNG

CHỦ NHIỆM THIẾT KẾ / PROJECT MANAGER:
LƯU GIANG NAM

CHỦ TRÌ THIẾT KẾ / DESIGN MANAGER:
NGÔ NGỌC BÌNH

KIỂM / CHECKED BY:
VŨ TUẤN ANH

THIẾT KẾ / DESIGNER
LÊ THỊ THANH
NGUYỄN XUÂN HIỆN
PHƯƠNG THỊ ÁNH TUYẾT
VŨ TIẾN DƯƠNG

TÊN DỰ ÁN / PROJECT NAME:
XÂY DỰNG NHÀ Ở TẠI LÔ ĐẤT NO-02

ĐỊA ĐIỂM XÂY DỰNG / PROJECT ADDRESS:
LÔ ĐẤT NO-22, PHƯỜNG BỒ ĐỀ, HÀ NỘI

HẠNG MỤC / ITEM:
KIẾN TRÚC

HOÀN THÀNH / FINISHED DATE:	MÃ SỐ DỰ ÁN / PROJECT No:
TKCS	2501
HOÀN THÀNH / FINISHED DATE: 2026	PHIÊN BẢN / REVISION: 1

TÊN BẢN VẼ / SHEET NAME:
MẶT BẰNG TẦNG TUM

SỐ HIỆU BẢN VẼ / SHEET NUMBER:
A.1-01.106

© 2025 - INNO.,jsc

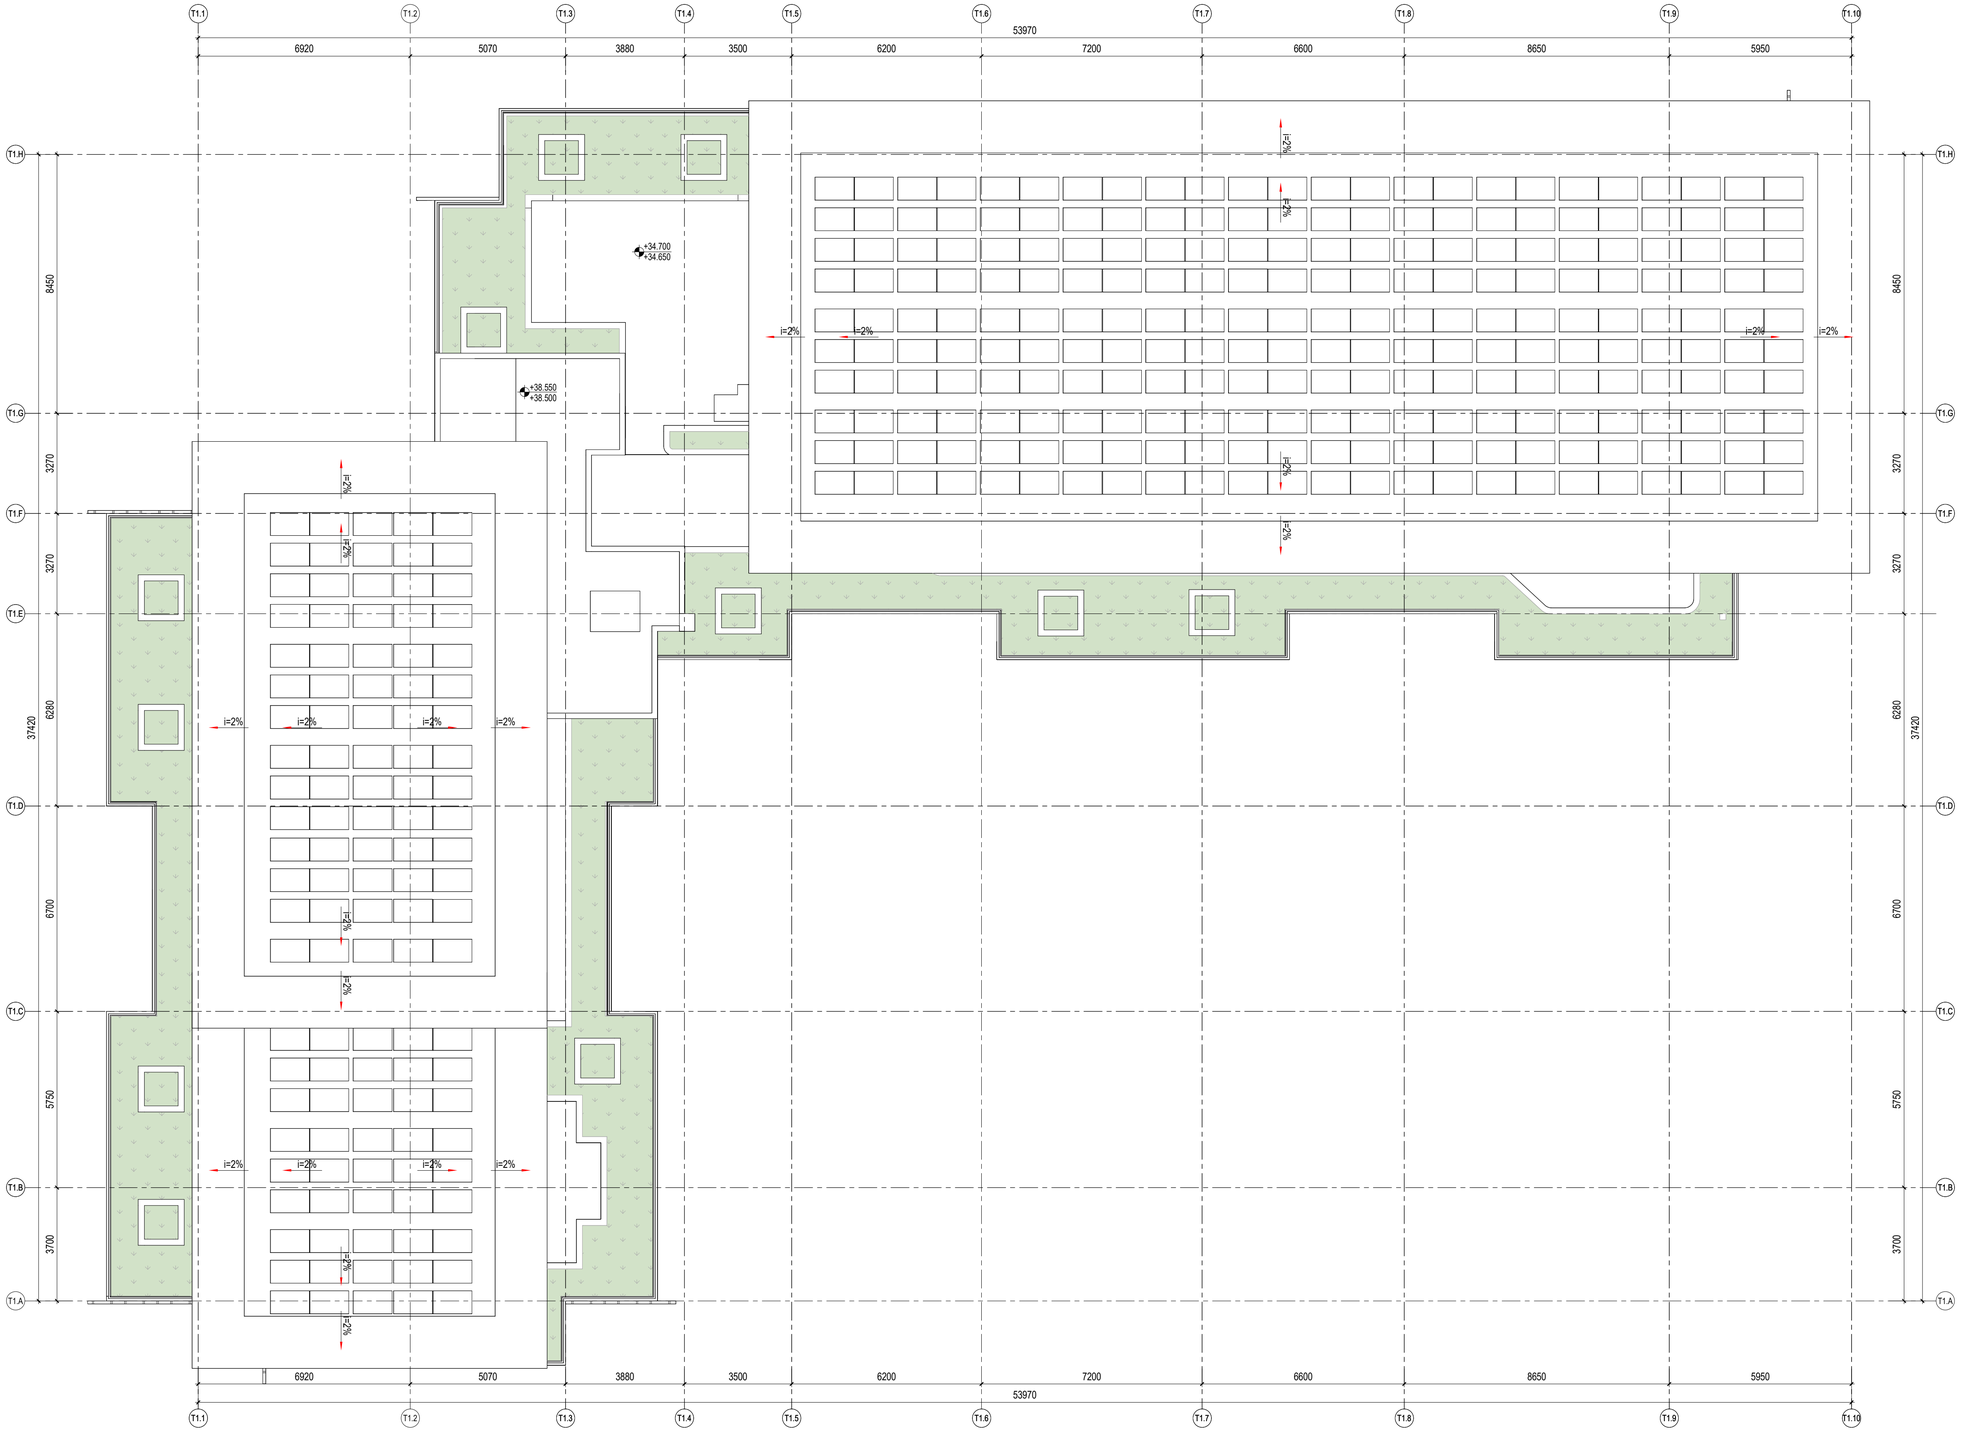

MẶT BẰNG MÁI
TL: 1 : 100

PHIÊN BẢN	NỘI DUNG ĐIỀU CHỈNH	NGÀY NỘP

GHI CHÚ:

- CỐT +0.000 LẤY TẠI SÀN HOÀN THIỆN TẦNG 1 CÔNG TRÌNH TƯƠNG ĐƯƠNG COTE TUYỆT ĐỐI +7.900 (HỆ TỌA ĐỘ VN-2000)

- TÒA 1 CHIỀU CAO CÔNG TRÌNH TÍNH TỪ:
  + COTE HOÀN THIỆN +0.000: 43M
  + COTE NỀN TỰ NHIÊN THẤP NHẤT -1.000: 44M
- TÒA 2 CHIỀU CAO CÔNG TRÌNH TÍNH TỪ:
  + COTE HOÀN THIỆN +0.000: 50M
  + COTE NỀN TỰ NHIÊN THẤP NHẤT -1.000: 51M
- TÒA 3 CHIỀU CAO CÔNG TRÌNH TÍNH TỪ:
  + COTE HOÀN THIỆN +0.000: 59M
  + COTE NỀN TỰ NHIÊN THẤP NHẤT -1.000: 60M

- KHU VỰC TMDV BÀN GIAO THÔ, VỆ SINH KHÔNG XÂY, CHỈ BỐ TRÍ LAYOUT ĐỊNH HƯỚNG ĐẶT CÁC ĐẦU CHỜ.

- TỶ LỆ SỬ DỤNG VẬT LIỆU XANH KHÔNG NUNG ĐÁP ỨNG TỚI 90% KHỐI LƯỢNG GẠCH TRONG CÔNG TRÌNH

- TRONG PHÒNG RÁC KHÔNG BỐ TRÍ CÁC CHẤT, VẬT LIỆU CÓ KHẢ NĂNG GÂY CHÁY NỔ

- TƯỜNG NGĂN CHÁY, VÁCH NGĂN CHÁY TRONG CÁC GIAN PHÒNG ĐƯỢC NGĂN CHIA ĐẾN TRẦN BÊ TÔNG.

- VẬT LIỆU HOÀN THIỆN TRẦN, TƯỜNG, SÀN TRÊN CÁC ĐƯỜNG THOÁT NẠN, TRONG SẢNH THANG MÁY, SẢNH CHUNG, TẦNG KỸ THUẬT LÀ VẬT LIỆU KHÔNG CHÁY ĐẠT CV0

- TRONG CÁC KHÔNG GIAN TRẦN TREO KHÔNG BỐ TRÍ CÁC KÊNH, ĐƯỜNG ỐNG DẪN VẬN CHUYỂN CÁC CHẤT CHÁY DẠNG KHÍ, HỖN HỢP KHÍ, CHẤT LỎNG VÀ VẬT LIỆU CHÁY.

- TRONG CÔNG TRÌNH KHÔNG BỐ TRÍ TRẦN TREO CHO CÁC GIAN PHÒNG HẠNG A VÀ HẠNG B

- KHÔNG CÓ KÊNH, GIẾNG, ĐƯỜNG ỐNG ĐI QUA TƯỜNG NGĂN CHÁY LOẠI 1

CHỦ ĐẦU TƯ / OWNER:
CÔNG TY CỔ PHẦN THƯƠNG MẠI DƯƠNG PHÚC THẮNG
DUONG PHUC THANG TRADING JOINT STOCK COMPANY
ĐỊA CHỈ / ADDRESS:
Tầng 16, Tòa OSI Tower, Khu tây Hồ Tây, Phường Xuân Đỉnh, Thành phố Hà Nội, Việt Nam.
Hotline : 0243 2077 272

TƯ VẤN KIẾN TRÚC CHÍNH / MAIN ARCHITECTURAL CONSULTANT:
CÔNG TY TNHH KIẾN TRÚC DP VIỆT NAM
DP ARCHITECTS VIETNAM CO.,LTD.
ĐỊA CHỈ / ADDRESS:
Tầng 4, số 82 Võ Văn Tần, Phường Xuân Hòa, TP.Hồ Chí Minh
Hotline : 0283 5357 507
Fax: 0283 5357 517
Email : dparchitects@dpa.com.sg

TƯ VẤN THIẾT KẾ / CONSULTANT:
CÔNG TY CỔ PHẦN INNO
INNO.,JSC
ĐỊA CHỈ / ADDRESS
HN: 39 Thượng Thụy, Phú Thượng, Hà Nội
HCM: 37 Nguyễn Văn Hưởng, An Khánh, TP. HCM
Hotline: 0243 212 1776 Email : ad@innojsc.com

TỔNG GIÁM ĐỐC / GENERAL DIRECTOR:
ĐOÀN VĂN ĐỘNG
CHỦ NHIỆM THIẾT KẾ / PROJECT MANAGER:
LƯU GIANG NAM
CHỦ TRÌ THIẾT KẾ / DESIGN MANAGER:
NGÔ NGỌC BÌNH
KIỂM / CHECKED BY:
VŨ TUẤN ANH
THIẾT KẾ / DESIGNER
LÊ THỊ THANH **NGUYỄN XUÂN HIỆN**
PHƯƠNG THỊ ÁNH TUYẾT **VŨ TIẾN DƯƠNG**

TÊN DỰ ÁN / PROJECT NAME:
XÂY DỰNG NHÀ Ở TẠI LÔ ĐẤT NO-02

ĐỊA ĐIỂM XÂY DỰNG / PROJECT ADDRESS:
LÔ ĐẤT NO-22, PHƯỜNG BỒ ĐỀ, HÀ NỘI

HẠNG MỤC / ITEM:
KIẾN TRÚC

HOÀN THÀNH / FINISHED DATE:	MÃ SỐ DỰ ÁN / PROJECT No:
TKCS	2501
HOÀN THÀNH / FINISHED DATE: 2026	PHIÊN BẢN / REVISION: 2

TÊN BẢN VẼ / SHEET NAME:
MẶT BẰNG MÁI

SỐ HIỆU BẢN VẼ / SHEET NUMBER:
A.1-01.107

© 2025 - INNO.,jsc

MẶT BẰNG: THÁP 2

© 2025 - INNO Jsc

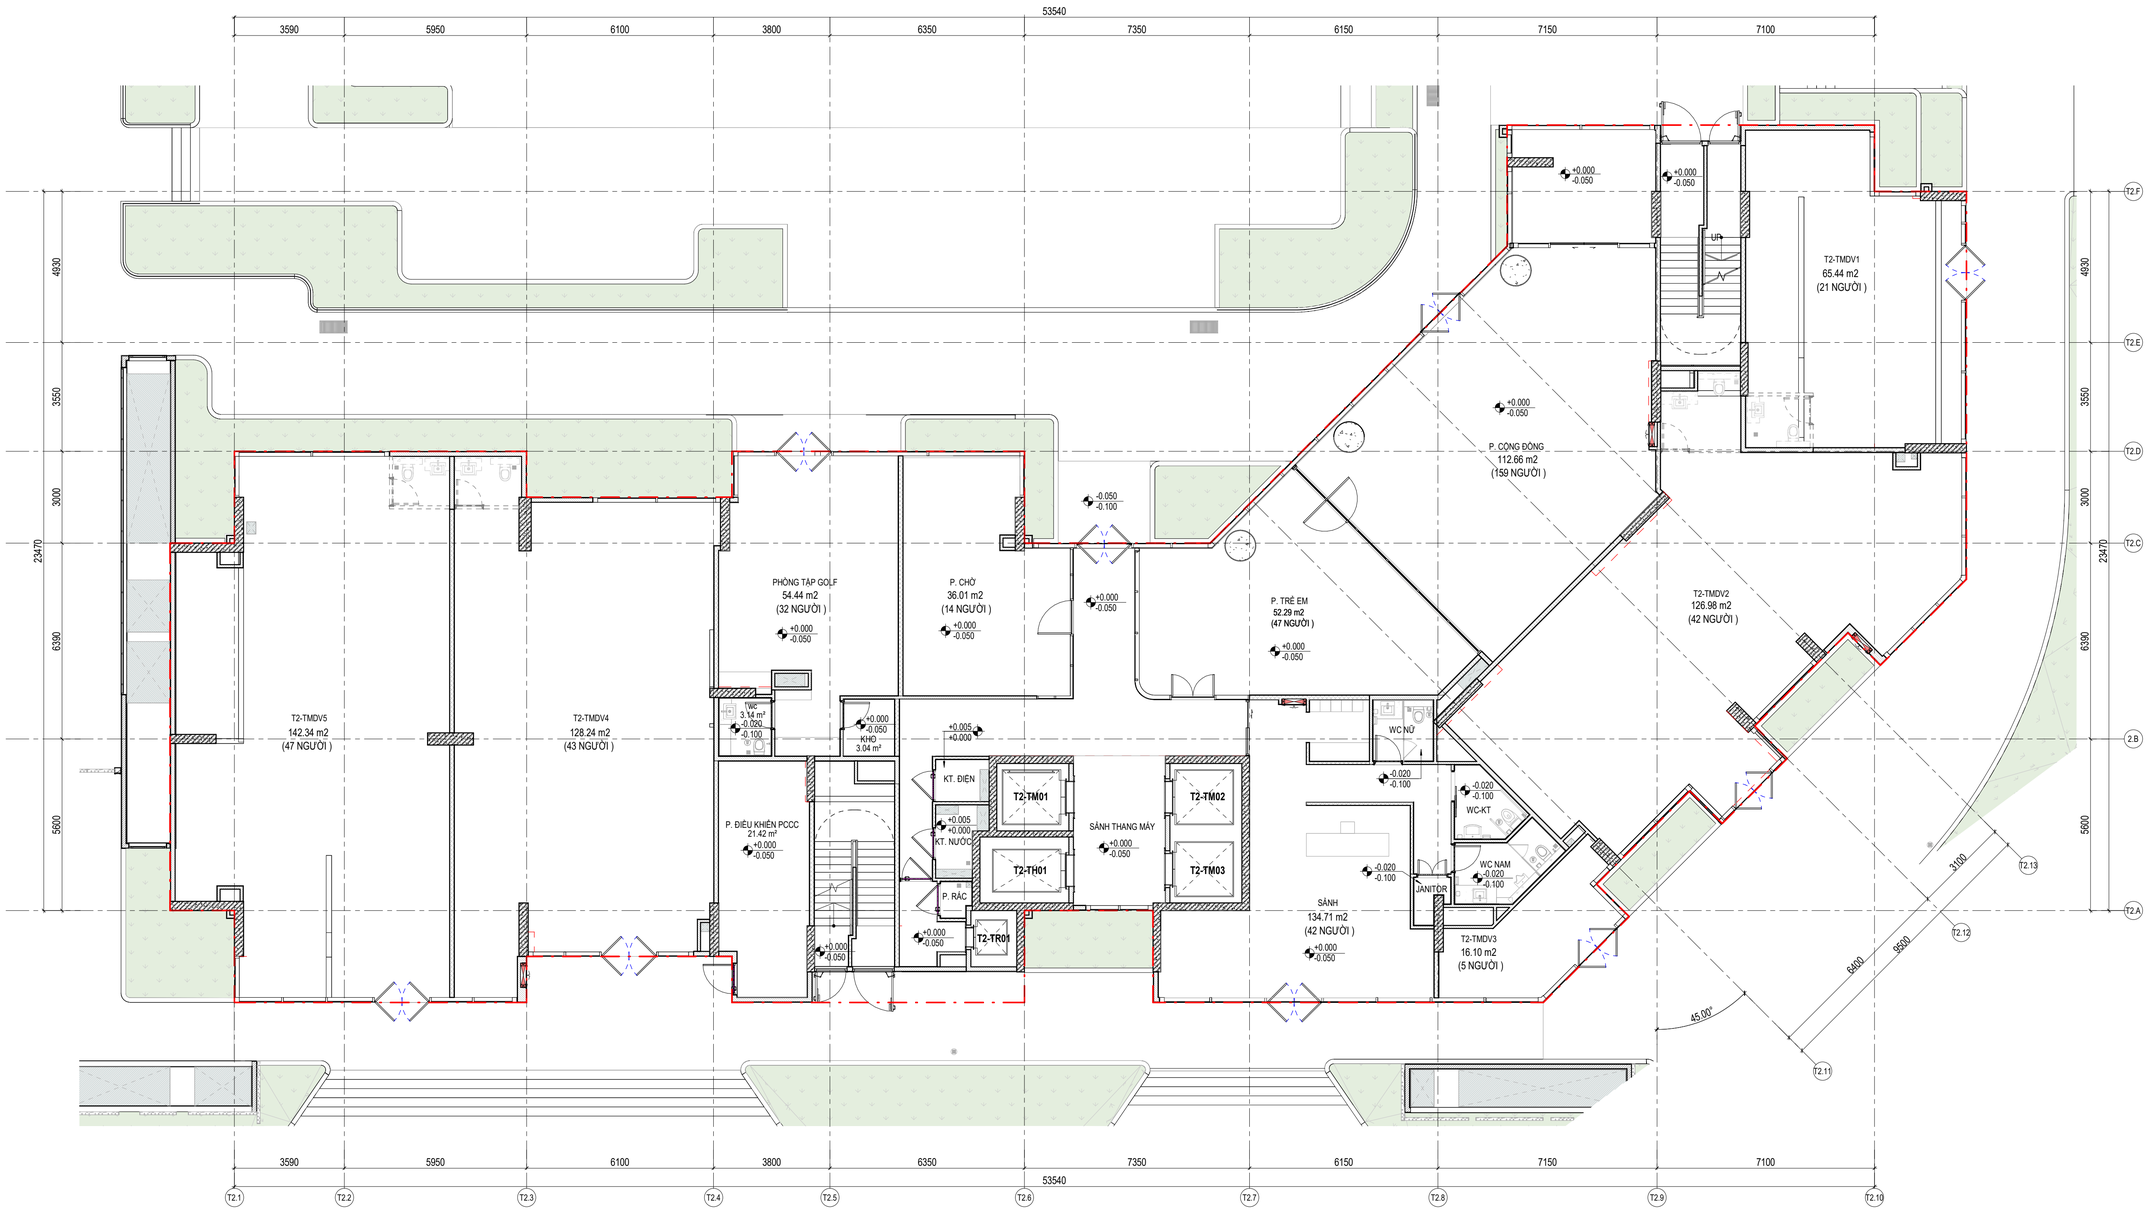

MẶT BẰNG TẦNG 1

TL: 1 : 100

DIỆN TÍCH SÀN XÂY DỰNG (GFA) :1054.29 M2

THỐNG KÊ DIỆN TÍCH TMDV T1

STT	TMDV	IFA(m²)	GFA(m²)	NSA(m²)
1	T2-TMDV1	68.89 m²	70.52 m²	65.44 m²
2	T2-TMDV2	135.18 m²	137.36 m²	126.98 m²
3	T2-TMDV3	17.81 m²	18.58 m²	16.10 m²
4	T2-TMDV4	135.14 m²	136.99 m²	128.24 m²
5	T2-TMDV5	149.23 m²	152.91 m²	142.34 m²
TỔNG: 5		506.26 m²	516.37 m²	479.10 m²

PHIÊN BẢN	NỘI DUNG ĐIỀU CHỈNH	NGÀY NỘP

GHI CHÚ:

- CỐT +0.000 LẤY TẠI SÀN HOÀN THIỆN TẦNG 1 CÔNG TRÌNH TƯƠNG ĐƯƠNG COTE TUYỆT ĐỐI +7.900 (HỆ TỌA ĐỘ VN-2000)

- TÒA 1 CHIỀU CAO CÔNG TRÌNH TÍNH TỪ:
  + COTE HOÀN THIỆN +0.000: 43M
  + COTE NỀN TỰ NHIÊN THẤP NHẤT -1.000: 44M
- TÒA 2 CHIỀU CAO CÔNG TRÌNH TÍNH TỪ:
  + COTE HOÀN THIỆN +0.000: 50M
  + COTE NỀN TỰ NHIÊN THẤP NHẤT -1.000: 51M
- TÒA 3 CHIỀU CAO CÔNG TRÌNH TÍNH TỪ:
  + COTE HOÀN THIỆN +0.000: 59M
  + COTE NỀN TỰ NHIÊN THẤP NHẤT -1.000: 60M

- KHU VỰC TMDV BÀN GIAO THÔ, VỆ SINH KHÔNG XÂY, CHỈ BỐ TRÍ LAYOUT ĐỊNH HƯỚNG ĐẶT CÁC ĐẦU CHỜ.

- TỶ LỆ SỬ DỤNG VẬT LIỆU XANH KHÔNG NUNG ĐÁP ỨNG TỚI 90% KHỐI LƯỢNG GẠCH TRONG CÔNG TRÌNH

- TRONG PHÒNG RÁC KHÔNG BỐ TRÍ CÁC CHẤT, VẬT LIỆU CÓ KHẢ NĂNG GÂY CHÁY NỔ

- TƯỜNG NGĂN CHÁY, VÁCH NGĂN CHÁY TRONG CÁC GIAN PHÒNG ĐƯỢC NGĂN CHIA ĐẾN TRẦN BÊ TÔNG.

- VẬT LIỆU HOÀN THIỆN TRẦN, TƯỜNG, SÀN TRÊN CÁC ĐƯỜNG THOÁT NẠN, TRONG SẢNH THANG MÁY, SẢNH CHUNG, TẦNG KỸ THUẬT LÀ VẬT LIỆU KHÔNG CHÁY ĐẠT CV0

- TRONG CÁC KHÔNG GIAN TRẦN TREO KHÔNG BỐ TRÍ CÁC KÊNH, ĐƯỜNG ỐNG DẪN VẬN CHUYỂN CÁC CHẤT CHÁY DẠNG KHÍ, HỖN HỢP KHÍ, CHẤT LỎNG VÀ VẬT LIỆU CHÁY.

- TRONG CÔNG TRÌNH KHÔNG BỐ TRÍ TRẦN TREO CHO CÁC GIAN PHÒNG HẠNG A VÀ HẠNG B

- KHÔNG CÓ KÊNH, GIẾNG, ĐƯỜNG ỐNG ĐI QUA TƯỜNG NGĂN CHÁY LOẠI 1

CHỦ ĐẦU TƯ / OWNER:
CÔNG TY CỔ PHẦN THƯƠNG MẠI DƯƠNG PHÚC THẮNG
DUONG PHUC THANG TRADING JOINT STOCK COMPANY
ĐỊA CHỈ / ADDRESS:
Tầng 16, Tòa OSI Tower, Khu tây Hồ Tây, Phường Xuân Đỉnh, Thành phố Hà Nội, Việt Nam.
Hotline : 0243 2077 272

TƯ VẤN KIẾN TRÚC CHÍNH / MAIN ARCHITECTURAL CONSULTANT:
CÔNG TY TNHH KIẾN TRÚC DP VIỆT NAM
DP ARCHITECTS VIETNAM CO.,LTD.
ĐỊA CHỈ / ADDRESS:
Tầng 4, số 82 Võ Văn Tần, Phường Xuân Hòa, TP.Hồ Chí Minh
Hotline : 0283 5357 507
Fax: 0283 5357 517
Email : dparchitects@dpa.com.sg

TƯ VẤN THIẾT KẾ / CONSULTANT:
CÔNG TY CỔ PHẦN INNO
INNO.,JSC
ĐỊA CHỈ / ADDRESS:
HN: 39 Thượng Thụy, Phú Thượng, Hà Nội
HCM: 37 Nguyễn Văn Hưởng, An Khánh, TP. HCM
Hotline: 0243 212 1776 Email : ad@innojsc.com

TỔNG GIÁM ĐỐC / GENERAL DIRECTOR:
ĐOÀN VĂN ĐỘNG
CHỦ NHIỆM THIẾT KẾ / PROJECT MANAGER:
LƯU GIANG NAM
CHỦ TRÌ THIẾT KẾ / DESIGN MANAGER:
NGÔ NGỌC BÌNH
KIỂM / CHECKED BY:
VŨ TUẤN ANH
THIẾT KẾ / DESIGNER:
LÊ THỊ THANH **NGUYỄN XUÂN HIỂN**
PHƯƠNG THỊ ÁNH TUYẾT **VŨ TIẾN DƯƠNG**

TÊN DỰ ÁN / PROJECT NAME:
XÂY DỰNG NHÀ Ở TẠI LÔ ĐẤT NO-02

ĐỊA ĐIỂM XÂY DỰNG / PROJECT ADDRESS:
LÔ ĐẤT NO-22, PHƯỜNG BỒ ĐỀ, HÀ NỘI

HẠNG MỤC / ITEM:
KIẾN TRÚC

HOÀN THÀNH / FINISHED DATE:	MÃ SỐ DỰ ÁN / PROJECT No:
TKCS	2501
HOÀN THÀNH / FINISHED DATE: 2026	PHIÊN BẢN / REVISION: 2

TÊN BẢN VẼ / SHEET NAME:
MẶT BẰNG TẦNG 1

SỐ HIỆU BẢN VẼ / SHEET NUMBER:
A.2-01.101

© 2025 - INNO.,jsc

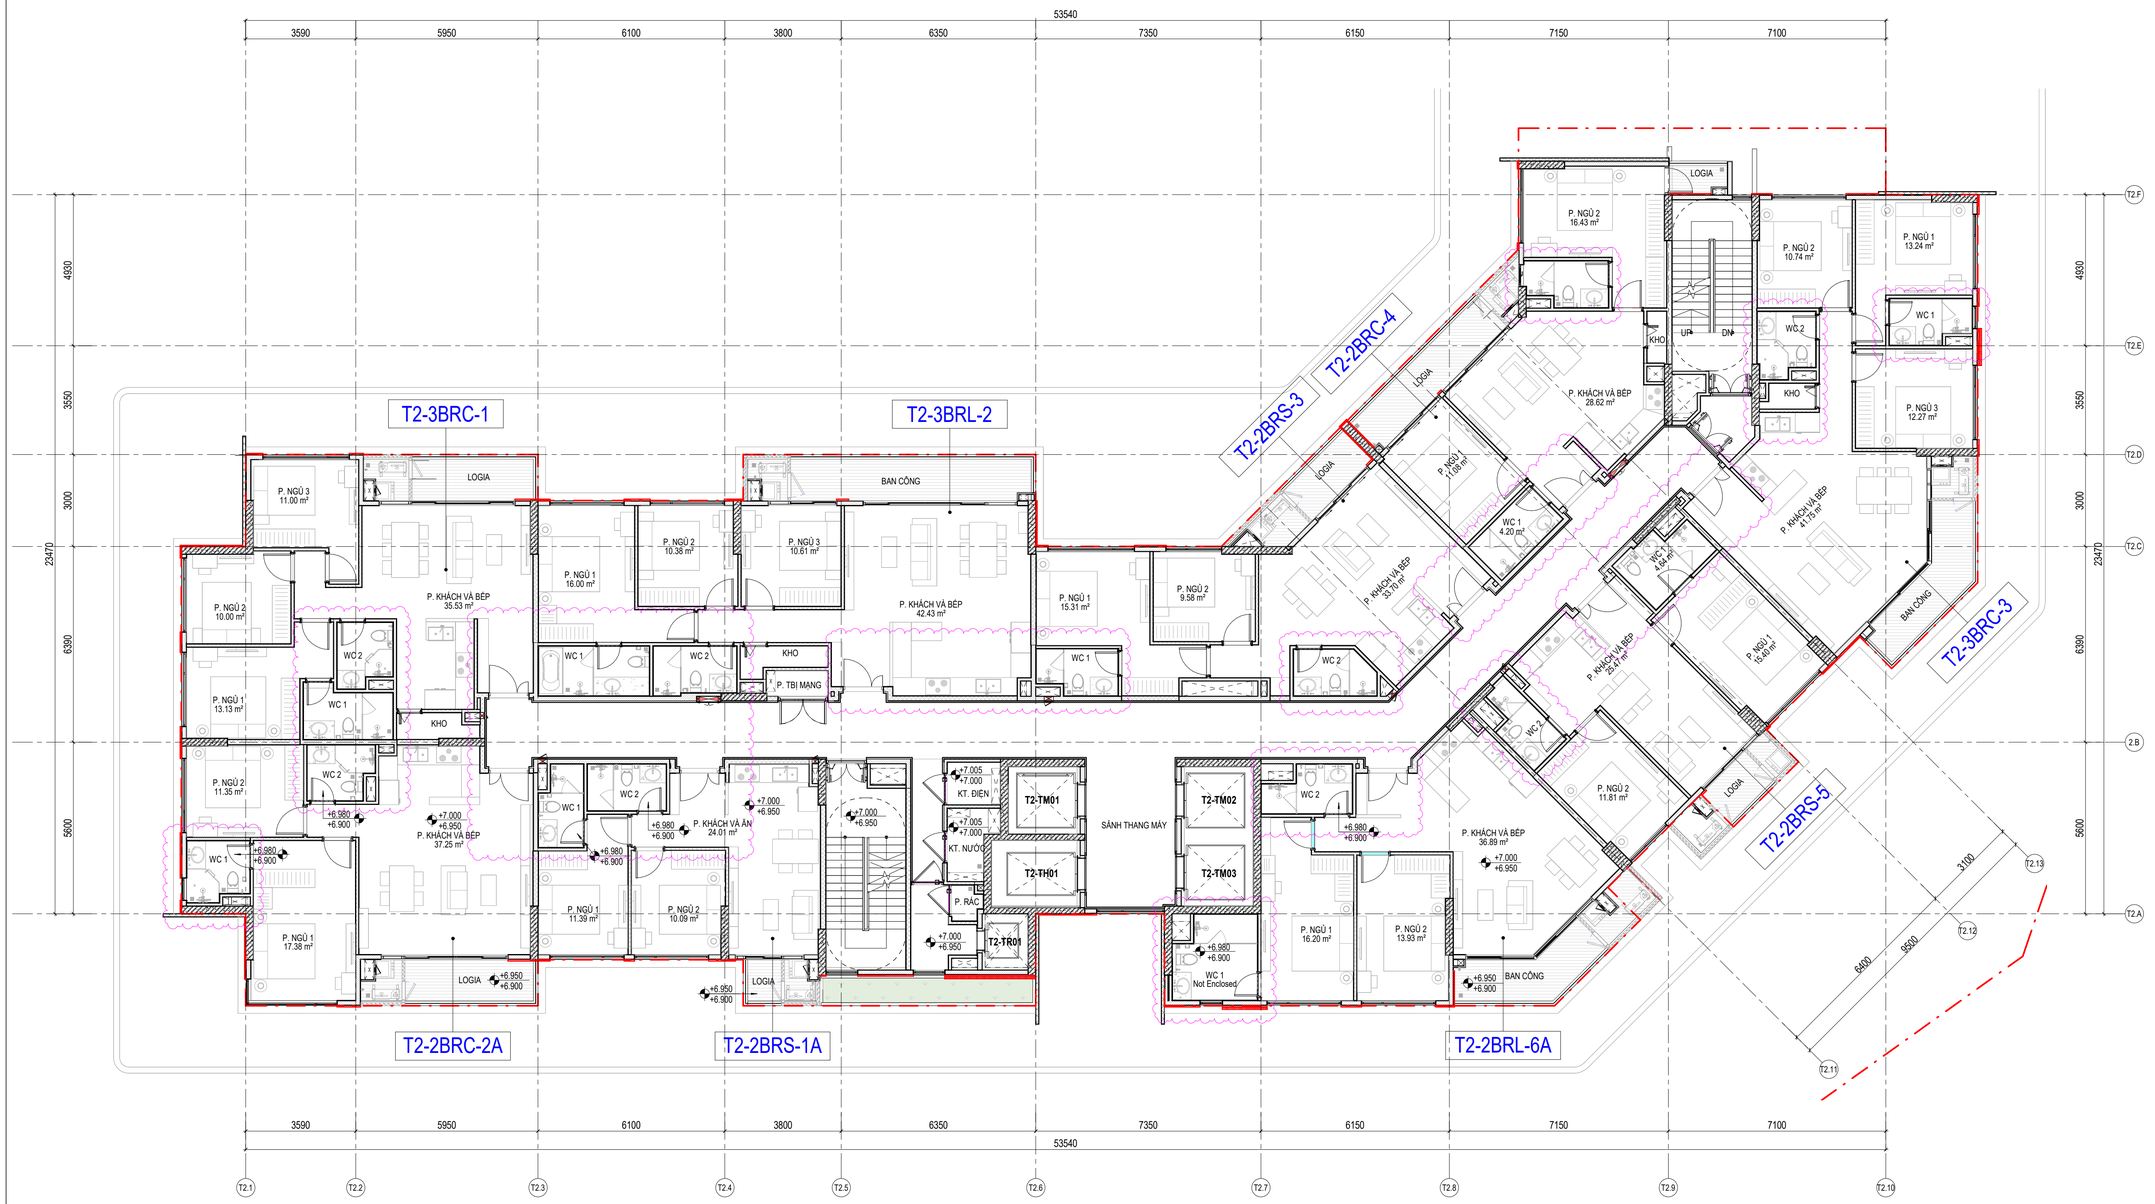

MẶT BẰNG TẦNG 2

TL: 1 : 100

DIỆN TÍCH SÀN XÂY DỰNG (GFA) :1054.29 M2

THỐNG KÊ DIỆN TÍCH TĐH 01 (TẦNG 2-5)

STT	Tên căn hộ	Số lượng(căn)	Loại căn hộ(Phòng ngủ)	IFA(m²)	GFA(m²)	NSA(m²)	Số người
1	T2-2BRS-1A	1	2PN	63.41 m²	64.03 m²	58.04 m²	2
2	T2-2BRC-2A	1	2PN	90.16 m²	91.58 m²	82.73 m²	3
3	T2-2BRS-3	1	2PN	82.88 m²	83.44 m²	74.97 m²	3
4	T2-2BRC-4	1	2PN	86.67 m²	87.52 m²	79.72 m²	3
5	T2-2BRS-5	1	2PN	73.73 m²	74.30 m²	67.61 m²	3
6	T2-2BRL-6A	1	2PN	98.07 m²	99.33 m²	89.88 m²	3
7	T2-3BRC-1	1	3PN	98.18 m²	99.67 m²	91.13 m²	4
8	T2-3BRL-2	1	3PN	116.06 m²	116.86 m²	107.38 m²	4
9	T2-3BRC-3	1	3PN	107.98 m²	109.55 m²	99.67 m²	4
TỔNG		9		817.15 m²	826.29 m²	751.14 m²	29

PHIÊN BẢN	NỘI DUNG ĐIỀU CHỈNH	NGÀY NỘP

GHI CHÚ:

- CỐT +0.000 LẤY TẠI SÀN HOÀN THIỆN TẦNG 1 CÔNG TRÌNH TƯƠNG ĐƯƠNG COTE TUYỆT ĐỐI +7.900 (HỆ TỌA ĐỘ VN-2000)

- TÒA 1 CHIỀU CAO CÔNG TRÌNH TÍNH TỪ:
  + COTE HOÀN THIỆN +0.000: 43M
  + COTE NỀN TỰ NHIÊN THẤP NHẤT -1.000: 44M
- TÒA 2 CHIỀU CAO CÔNG TRÌNH TÍNH TỪ:
  + COTE HOÀN THIỆN +0.000: 50M
  + COTE NỀN TỰ NHIÊN THẤP NHẤT -1.000: 51M
- TÒA 3 CHIỀU CAO CÔNG TRÌNH TÍNH TỪ:
  + COTE HOÀN THIỆN +0.000: 59M
  + COTE NỀN TỰ NHIÊN THẤP NHẤT -1.000: 60M

- KHU VỰC TMDV BÀN GIAO THÔ, VỆ SINH KHÔNG XÂY, CHỈ BỐ TRÍ LAYOUT ĐỊNH HƯỚNG ĐẶT CÁC ĐẦU CHỜ.

- TỶ LỆ SỬ DỤNG VẬT LIỆU XANH KHÔNG NUNG ĐÁP ỨNG TỚI 90% KHỐI LƯỢNG GẠCH TRONG CÔNG TRÌNH

- TRONG PHÒNG RÁC KHÔNG BỐ TRÍ CÁC CHẤT, VẬT LIỆU CÓ KHẢ NĂNG GÂY CHÁY NỔ

- TƯỜNG NGĂN CHÁY, VÁCH NGĂN CHÁY TRONG CÁC GIAN PHÒNG ĐƯỢC NGĂN CHIA ĐẾN TRẦN BÊ TÔNG.

- VẬT LIỆU HOÀN THIỆN TRẦN, TƯỜNG, SÀN TRÊN CÁC ĐƯỜNG THOÁT NẠN, TRONG SẢNH THANG MÁY, SẢNH CHUNG, TẦNG KỸ THUẬT LÀ VẬT LIỆU KHÔNG CHÁY ĐẠT CV0

- TRONG CÁC KHÔNG GIAN TRẦN TREO KHÔNG BỐ TRÍ CÁC KÊNH, ĐƯỜNG ỐNG DẪN VẬN CHUYỂN CÁC CHẤT CHÁY DẠNG KHÍ, HỖN HỢP KHÍ, CHẤT LỎNG VÀ VẬT LIỆU CHÁY.

- TRONG CÔNG TRÌNH KHÔNG BỐ TRÍ TRẦN TREO CHO CÁC GIAN PHÒNG HẠNG A VÀ HẠNG B

- KHÔNG CÓ KÊNH, GIẾNG, ĐƯỜNG ỐNG ĐI QUA TƯỜNG NGĂN CHÁY LOẠI 1

ỐP FACADE : LÀM VIỆC VỚI TƯ VẤN FACADE

CHỦ ĐẦU TƯ / OWNER:
CÔNG TY CỔ PHẦN THƯƠNG MẠI DƯƠNG PHÚC THẮNG
DUONG PHUC THANG TRADING JOINT STOCK COMPANY
ĐỊA CHỈ / ADDRESS: Tầng 16, Tòa OSI Tower, Khu tây Hồ Tây, Phường Xuân Đỉnh, Thành phố Hà Nội, Việt Nam. Hotline : 0243 2077 272

TƯ VẤN KIẾN TRÚC CHÍNH / MAIN ARCHITECTURAL CONSULTANT:
CÔNG TY TNHH KIẾN TRÚC DP VIỆT NAM
DP ARCHITECTS VIETNAM CO.,LTD.
ĐỊA CHỈ / ADDRESS: Tầng 4, số 82 Võ Văn Tần, Phường Xuân Hòa, TP.Hồ Chí Minh Hotline : 0283 5357 507 Fax: 0283 5357 517 Email : dparchitects@dpa.com.sg

TƯ VẤN THIẾT KẾ / CONSULTANT:
CÔNG TY CỔ PHẦN INNO
INNO.,JSC
ĐỊA CHỈ / ADDRESS: HN: 39 Thượng Thụy, Phú Thượng, Hà Nội HCM: 37 Nguyễn Văn Hưởng, An Khánh, TP. HCM Hotline: 0243 212 1776 Email : ad@innojsc.com

TỔNG GIÁM ĐỐC / GENERAL DIRECTOR:
ĐOÀN VĂN ĐỘNG
CHỦ NHIỆM THIẾT KẾ / PROJECT MANAGER:
LƯU GIANG NAM
CHỦ TRÌ THIẾT KẾ / DESIGN MANAGER:
NGÔ NGỌC BÌNH
KIỂM / CHECKED BY:
VŨ TUẤN ANH
THIẾT KẾ / DESIGNER
LÊ THỊ THANH **NGUYỄN XUÂN HIỆN**
PHƯƠNG THỊ ÁNH TUYẾT **VŨ TIẾN DƯƠNG**

TÊN DỰ ÁN / PROJECT NAME:
XÂY DỰNG NHÀ Ở TẠI LÔ ĐẤT NO-02

ĐỊA ĐIỂM XÂY DỰNG / PROJECT ADDRESS:
LÔ ĐẤT NO-22, PHƯỜNG BỒ ĐỀ, HÀ NỘI

HẠNG MỤC / ITEM:
KIẾN TRÚC

HOÀN THÀNH / FINISHED DATE:	MÃ SỐ DỰ ÁN / PROJECT No:
TKCS	2501
HOÀN THÀNH / FINISHED DATE: 2026	PHIÊN BẢN / REVISION:

TÊN BẢN VẼ / SHEET NAME:
MẶT BẰNG TẦNG 2

SỐ HIỆU BẢN VẼ / SHEET NUMBER:
A.2-01.102

© 2025 - INNO.,jsc

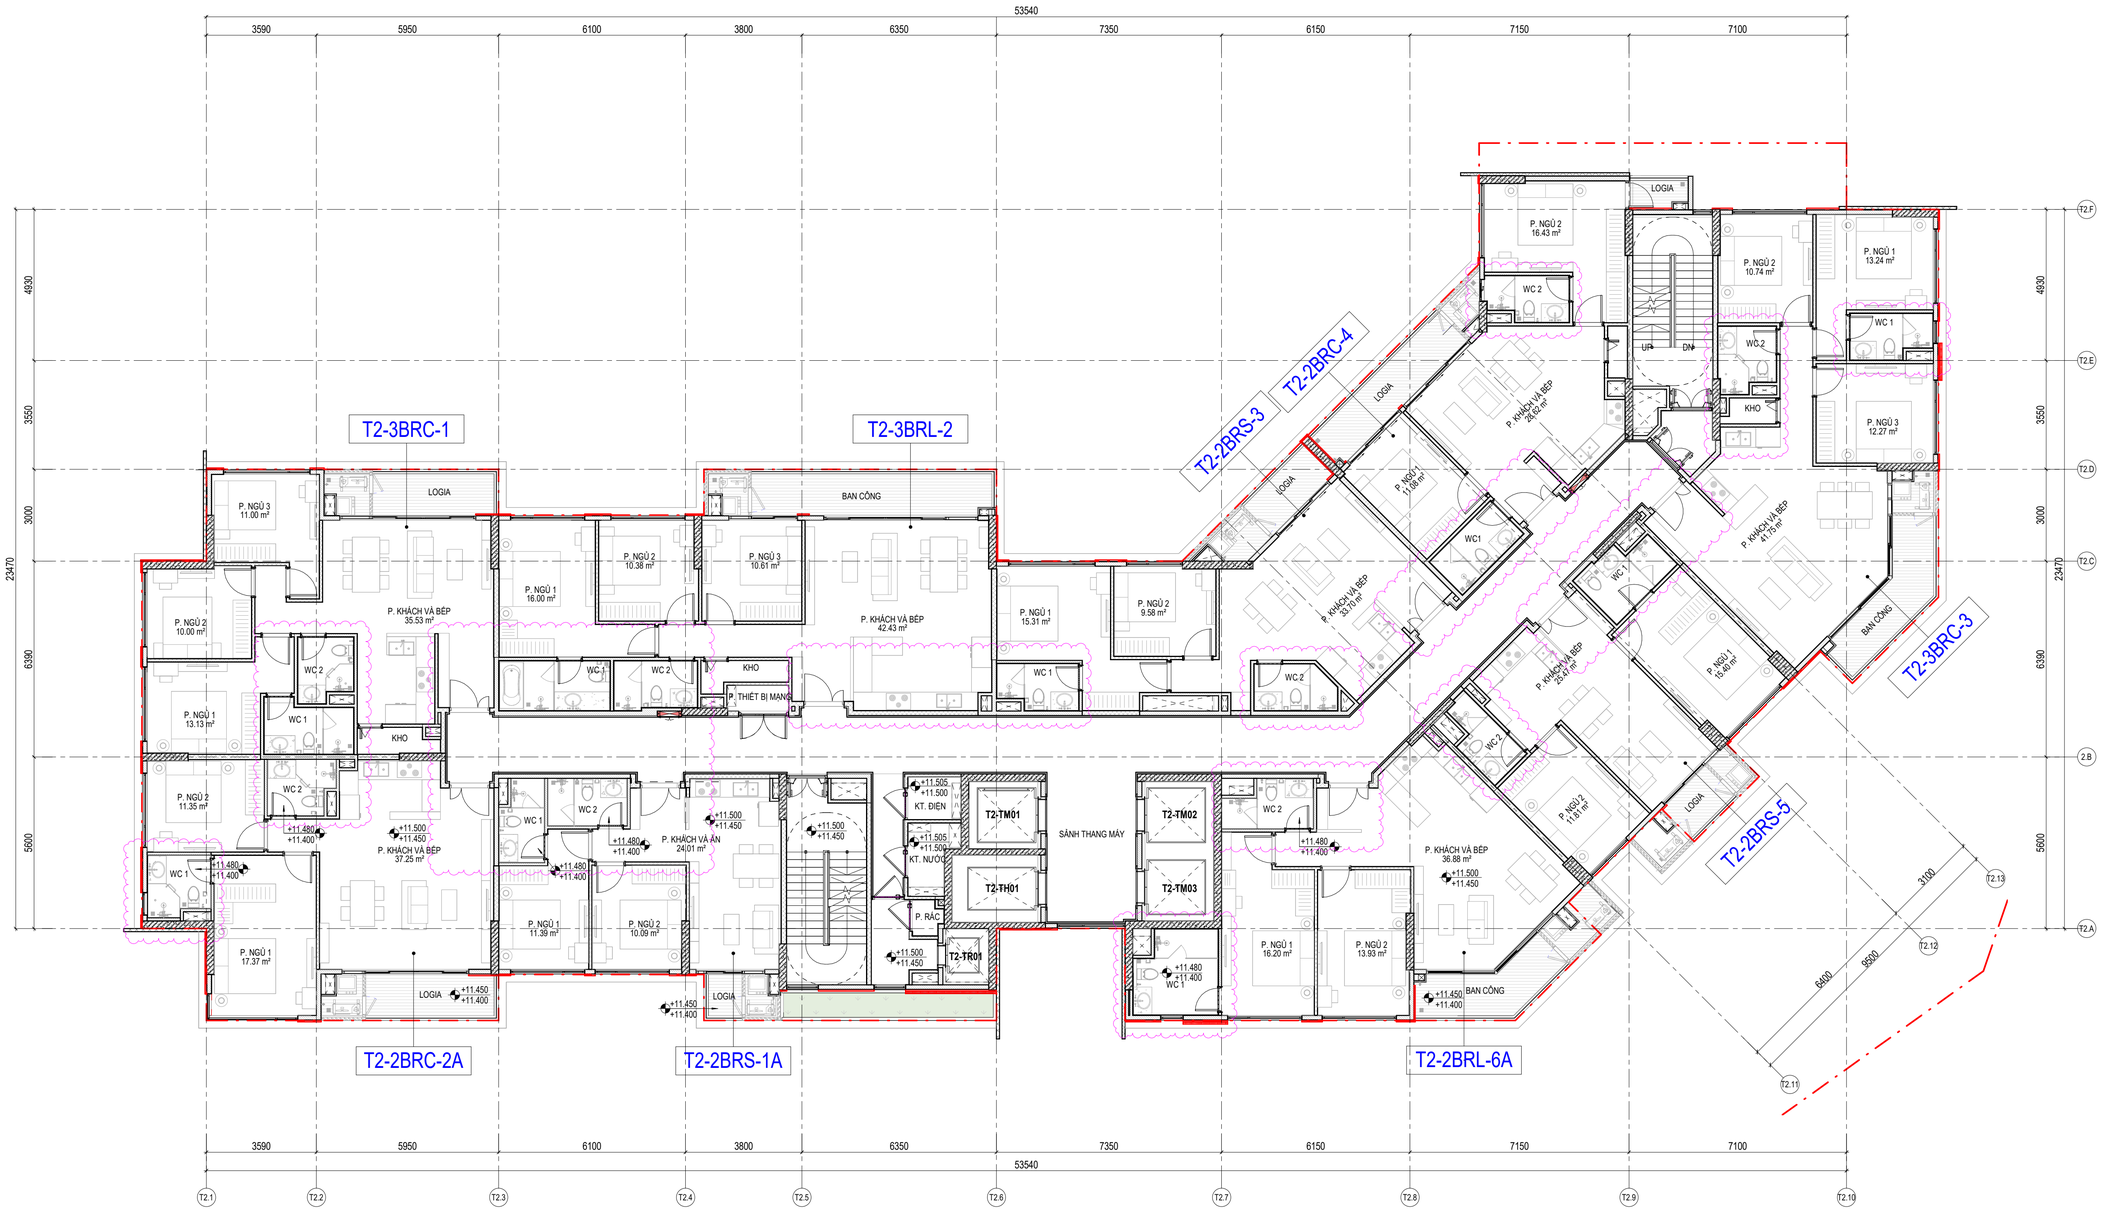

MẶT BẰNG TẦNG 3-5

TL: 1 : 100

DIỆN TÍCH SÀN XÂY DỰNG (GFA) :1036.00 M2

THỐNG KÊ DIỆN TÍCH TĐH 01 (TẦNG 2-5)

STT	Tên căn hộ	Số lượng(căn)	Loại căn hộ(Phòng ngủ)	IFA(m²)	GFA(m²)	NSA(m²)	Số người
1	T2-2BRS-1A	1	2PN	63.41 m²	64.03 m²	58.04 m²	2
2	T2-2BRC-2A	1	2PN	90.16 m²	91.58 m²	82.73 m²	3
3	T2-2BRS-3	1	2PN	82.88 m²	83.44 m²	74.97 m²	3
4	T2-2BRC-4	1	2PN	86.67 m²	87.52 m²	79.72 m²	3
5	T2-2BRS-5	1	2PN	73.73 m²	74.30 m²	67.61 m²	3
6	T2-2BRL-6A	1	2PN	98.07 m²	99.33 m²	89.88 m²	3
7	T2-3BRC-1	1	3PN	98.18 m²	99.67 m²	91.13 m²	4
8	T2-3BRL-2	1	3PN	116.06 m²	116.86 m²	107.38 m²	4
9	T2-3BRC-3	1	3PN	107.98 m²	109.55 m²	99.67 m²	4
TỔNG		9		817.15 m²	826.29 m²	751.14 m²	29

PHIÊN BẢN	NỘI DUNG ĐIỀU CHỈNH	NGÀY NỘP

GHI CHÚ:

- CỐT +0.000 LẤY TẠI SÀN HOÀN THIỆN TẦNG 1 CÔNG TRÌNH TƯƠNG ĐƯƠNG COTE TUYỆT ĐỐI +7.900 (HỆ TỌA ĐỘ VN-2000)

- TÒA 1 CHIỀU CAO CÔNG TRÌNH TÍNH TỪ:
  + COTE HOÀN THIỆN +0.000: 43M
  + COTE NỀN TỰ NHIÊN THẤP NHẤT -1.000: 44M
- TÒA 2 CHIỀU CAO CÔNG TRÌNH TÍNH TỪ:
  + COTE HOÀN THIỆN +0.000: 50M
  + COTE NỀN TỰ NHIÊN THẤP NHẤT -1.000: 51M
- TÒA 3 CHIỀU CAO CÔNG TRÌNH TÍNH TỪ:
  + COTE HOÀN THIỆN +0.000: 59M
  + COTE NỀN TỰ NHIÊN THẤP NHẤT -1.000: 60M

- KHU VỰC TMDV BÀN GIAO THÔ, VỆ SINH KHÔNG XÂY, CHỈ BỐ TRÍ LAYOUT ĐỊNH HƯỚNG ĐẶT CÁC ĐẦU CHỜ.

- TỶ LỆ SỬ DỤNG VẬT LIỆU XANH KHÔNG NUNG ĐÁP ỨNG TỚI 90% KHỐI LƯỢNG GẠCH TRONG CÔNG TRÌNH

- TRONG PHÒNG RÁC KHÔNG BỐ TRÍ CÁC CHẤT, VẬT LIỆU CÓ KHẢ NĂNG GÂY CHÁY NỔ

- TƯỜNG NGĂN CHÁY, VÁCH NGĂN CHÁY TRONG CÁC GIAN PHÒNG ĐƯỢC NGĂN CHIA ĐẾN TRẦN BÊ TÔNG.

- VẬT LIỆU HOÀN THIỆN TRẦN, TƯỜNG, SÀN TRÊN CÁC ĐƯỜNG THOÁT NẠN, TRONG SẢNH THANG MÁY, SẢNH CHUNG, TẦNG KỸ THUẬT LÀ VẬT LIỆU KHÔNG CHÁY ĐẠT CV0

- TRONG CÁC KHÔNG GIAN TRẦN TREO KHÔNG BỐ TRÍ CÁC KÊNH, ĐƯỜNG ỐNG DẪN VẬN CHUYỂN CÁC CHẤT CHÁY DẠNG KHÍ, HỖN HỢP KHÍ, CHẤT LỎNG VÀ VẬT LIỆU CHÁY.

- TRONG CÔNG TRÌNH KHÔNG BỐ TRÍ TRẦN TREO CHO CÁC GIAN PHÒNG HẠNG A VÀ HẠNG B

- KHÔNG CÓ KÊNH, GIẾNG, ĐƯỜNG ỐNG ĐI QUA TƯỜNG NGĂN CHÁY LOẠI 1

ỐP FACADE : LÀM VIỆC VỚI TƯ VẤN FACADE

CHỦ ĐẦU TƯ / OWNER:
CÔNG TY CỔ PHẦN THƯƠNG MẠI DƯƠNG PHÚC THẮNG
DUONG PHUC THANG TRADING JOINT STOCK COMPANY
ĐỊA CHỈ / ADDRESS: Tầng 16, Tòa OSI Tower, Khu tây Hồ Tây, Phường Xuân Đỉnh, Thành phố Hà Nội, Việt Nam.
Hotline : 0243 2077 272

TƯ VẤN KIẾN TRÚC CHÍNH / MAIN ARCHITECTURAL CONSULTANT:
CÔNG TY TNHH KIẾN TRÚC DP VIỆT NAM
DP ARCHITECTS VIETNAM CO.,LTD.
ĐỊA CHỈ / ADDRESS: Tầng 4, số 82 Võ Văn Tần, Phường Xuân Hòa, TP.Hồ Chí Minh
Hotline : 0283 5357 507
Fax: 0283 5357 517
Email : dparchitects@dpa.com.sg

TƯ VẤN THIẾT KẾ / CONSULTANT:
CÔNG TY CỔ PHẦN INNO
INNO.,JSC
ĐỊA CHỈ / ADDRESS: HN: 39 Thượng Thụy, Phú Thượng, Hà Nội
HCM: 37 Nguyễn Văn Hưởng, An Khánh, TP. HCM
Hotline: 0243 212 1776 Email : ad@innojsc.com

TỔNG GIÁM ĐỐC / GENERAL DIRECTOR:
ĐOÀN VĂN ĐỘNG
CHỦ NHIỆM THIẾT KẾ / PROJECT MANAGER:
LƯU GIANG NAM
CHỦ TRÌ THIẾT KẾ / DESIGN MANAGER:
NGÔ NGỌC BÌNH
KIỂM / CHECKED BY:
VŨ TUẤN ANH
THIẾT KẾ / DESIGNER:
LÊ THỊ THANH **NGUYỄN XUÂN HIỆN**
PHƯƠNG THỊ ÁNH TUYẾT **VŨ TIẾN DƯƠNG**

TÊN DỰ ÁN / PROJECT NAME:
XÂY DỰNG NHÀ Ở TẠI LÔ ĐẤT NO-02

ĐỊA ĐIỂM XÂY DỰNG / PROJECT ADDRESS:
LÔ ĐẤT NO-22, PHƯỜNG BỒ ĐỀ, HÀ NỘI

HẠNG MỤC / ITEM:
KIẾN TRÚC

HOÀN THÀNH / FINISHED DATE:	MÃ SỐ DỰ ÁN / PROJECT No:
TKCS	2501
HOÀN THÀNH / FINISHED DATE: 2026	PHIÊN BẢN / REVISION: 1

TÊN BẢN VẼ / SHEET NAME:
MẶT BẰNG TẦNG 3-5

SỐ HIỆU BẢN VẼ / SHEET NUMBER:
A.2-01.103

© 2025 - INNO.,jsc

MẶT BẰNG TẦNG 4

TL: 1 : 100

DIỆN TÍCH SÀN XÂY DỰNG (GFA) :1036.00 M2

THỐNG KÊ DIỆN TÍCH TĐH 01 (TẦNG 2-5)

STT	Tên căn hộ	Số lượng(căn)	Loại căn hộ(Phòng ngủ)	IFA(m²)	GFA(m²)	NSA(m²)	Số người
1	T2-2BRS-1A	1	2PN	63.41 m²	64.03 m²	58.04 m²	2
2	T2-2BRC-2A	1	2PN	90.16 m²	91.58 m²	82.73 m²	3
3	T2-2BRS-3	1	2PN	82.88 m²	83.44 m²	74.97 m²	3
4	T2-2BRC-4	1	2PN	86.67 m²	87.52 m²	79.72 m²	3
5	T2-2BRS-5	1	2PN	73.73 m²	74.30 m²	67.61 m²	3
6	T2-2BRL-6A	1	2PN	98.07 m²	99.33 m²	89.88 m²	3
7	T2-3BRC-1	1	3PN	98.18 m²	99.67 m²	91.13 m²	4
8	T2-3BRL-2	1	3PN	116.06 m²	116.86 m²	107.38 m²	4
9	T2-3BRC-3	1	3PN	107.98 m²	109.55 m²	99.67 m²	4
TỔNG		9		817.15 m²	826.29 m²	751.14 m²	29

PHIÊN BẢN	NỘI DUNG ĐIỀU CHỈNH	NGÀY NỘP

GHI CHÚ:

- CỐT +0.000 LẤY TẠI SÀN HOÀN THIỆN TẦNG 1 CÔNG TRÌNH TƯƠNG ĐƯƠNG COTE TUYỆT ĐỐI +7.900 (HỆ TỌA ĐỘ VN-2000)

- TÒA 1 CHIỀU CAO CÔNG TRÌNH TÍNH TỪ:
  + COTE HOÀN THIỆN +0.000: 43M
  + COTE NỀN TỰ NHIÊN THẤP NHẤT -1.000: 44M
- TÒA 2 CHIỀU CAO CÔNG TRÌNH TÍNH TỪ:
  + COTE HOÀN THIỆN +0.000: 50M
  + COTE NỀN TỰ NHIÊN THẤP NHẤT -1.000: 51M
- TÒA 3 CHIỀU CAO CÔNG TRÌNH TÍNH TỪ:
  + COTE HOÀN THIỆN +0.000: 59M
  + COTE NỀN TỰ NHIÊN THẤP NHẤT -1.000: 60M

- KHU VỰC TMDV BÀN GIAO THÔ, VỆ SINH KHÔNG XÂY, CHỈ BỐ TRÍ LAYOUT ĐỊNH HƯỚNG ĐẶT CÁC ĐẦU CHỜ.

- TỶ LỆ SỬ DỤNG VẬT LIỆU XANH KHÔNG NUNG ĐÁP ỨNG TỐI 90% KHỐI LƯỢNG GẠCH TRONG CÔNG TRÌNH

- TRONG PHÒNG RÁC KHÔNG BỐ TRÍ CÁC CHẤT, VẬT LIỆU CÓ KHẢ NĂNG GÂY CHÁY NỔ

- TƯỜNG NGĂN CHÁY, VÁCH NGĂN CHÁY TRONG CÁC GIAN PHÒNG ĐƯỢC NGĂN CHIA ĐẾN TRẦN BÊ TÔNG.

- VẬT LIỆU HOÀN THIỆN TRẦN, TƯỜNG, SÀN TRÊN CÁC ĐƯỜNG THOÁT NẠN, TRONG SẢNH THANG MÁY, SẢNH CHUNG, TẦNG KỸ THUẬT LÀ VẬT LIỆU KHÔNG CHÁY ĐẠT CV0

- TRONG CÁC KHÔNG GIAN TRẦN TREO KHÔNG BỐ TRÍ CÁC KÊNH, ĐƯỜNG ỐNG DẪN VẬN CHUYỂN CÁC CHẤT CHÁY DẠNG KHÍ, HỖN HỢP KHÍ, CHẤT LỎNG VÀ VẬT LIỆU CHÁY.

- TRONG CÔNG TRÌNH KHÔNG BỐ TRÍ TRẦN TREO CHO CÁC GIAN PHÒNG HẠNG A VÀ HẠNG B

- KHÔNG CÓ KÊNH, GIẾNG, ĐƯỜNG ỐNG ĐI QUA TƯỜNG NGĂN CHÁY LOẠI 1

ỐP FACADE : LÀM VIỆC VỚI TƯ VẤN FACADE

CHỦ ĐẦU TƯ / OWNER:
CÔNG TY CỔ PHẦN THƯƠNG MẠI DƯƠNG PHÚC THẮNG
DUONG PHUC THANG TRADING JOINT STOCK COMPANY
ĐỊA CHỈ / ADDRESS:
Tầng 16, Tòa OSI Tower, Khu tây Hồ Tây, Phường Xuân Đỉnh, Thành phố Hà Nội, Việt Nam.
Hotline : 0243 2077 272

TƯ VẤN KIẾN TRÚC CHÍNH / MAIN ARCHITECTURAL CONSULTANT:
CÔNG TY TNHH KIẾN TRÚC DP VIỆT NAM
DP ARCHITECTS VIETNAM CO.,LTD.
ĐỊA CHỈ / ADDRESS:
Tầng 4, số 82 Võ Văn Tần, Phường Xuân Hòa, TP.Hồ Chí Minh
Hotline : 0283 5357 507
Fax: 0283 5357 517
Email : dparchitects@dpa.com.sg

TƯ VẤN THIẾT KẾ / CONSULTANT:
CÔNG TY CỔ PHẦN INNO
INNO.,JSC
ĐỊA CHỈ / ADDRESS:
HN: 39 Thượng Thụy, Phú Thượng, Hà Nội
HCM: 37 Nguyễn Văn Hưởng, An Khánh, TP. HCM
Hotline: 0243 212 1776 Email : ad@innojsc.com

TỔNG GIÁM ĐỐC / GENERAL DIRECTOR:
ĐOÀN VĂN ĐỘNG
CHỦ NHIỆM THIẾT KẾ / PROJECT MANAGER:
LƯU GIANG NAM
CHỦ TRÌ THIẾT KẾ / DESIGN MANAGER:
NGÔ NGỌC BÌNH
KIỂM / CHECKED BY:
VŨ TUẤN ANH
THIẾT KẾ / DESIGNER:
LÊ THỊ THANH **NGUYỄN XUÂN HIỆN**
PHƯƠNG THỊ ÁNH TUYẾT **VŨ TIẾN DƯƠNG**

TÊN DỰ ÁN / PROJECT NAME:
XÂY DỰNG NHÀ Ở TẠI LÔ ĐẤT NO-02

ĐỊA ĐIỂM XÂY DỰNG / PROJECT ADDRESS:
LÔ ĐẤT NO-22, PHƯỜNG BỒ ĐỀ, HÀ NỘI

HẠNG MỤC / ITEM:
KIẾN TRÚC

HOÀN THÀNH / FINISHED DATE:	MÃ SỐ DỰ ÁN / PROJECT No:
TKCS	2501
HOÀN THÀNH / FINISHED DATE: 2026	PHIÊN BẢN / REVISION: 2

TÊN BẢN VẼ / SHEET NAME:
MẶT BẰNG TẦNG 4

SỐ HIỆU BẢN VẼ / SHEET NUMBER:
A.2-01.104

© 2025 - INNO.,jsc

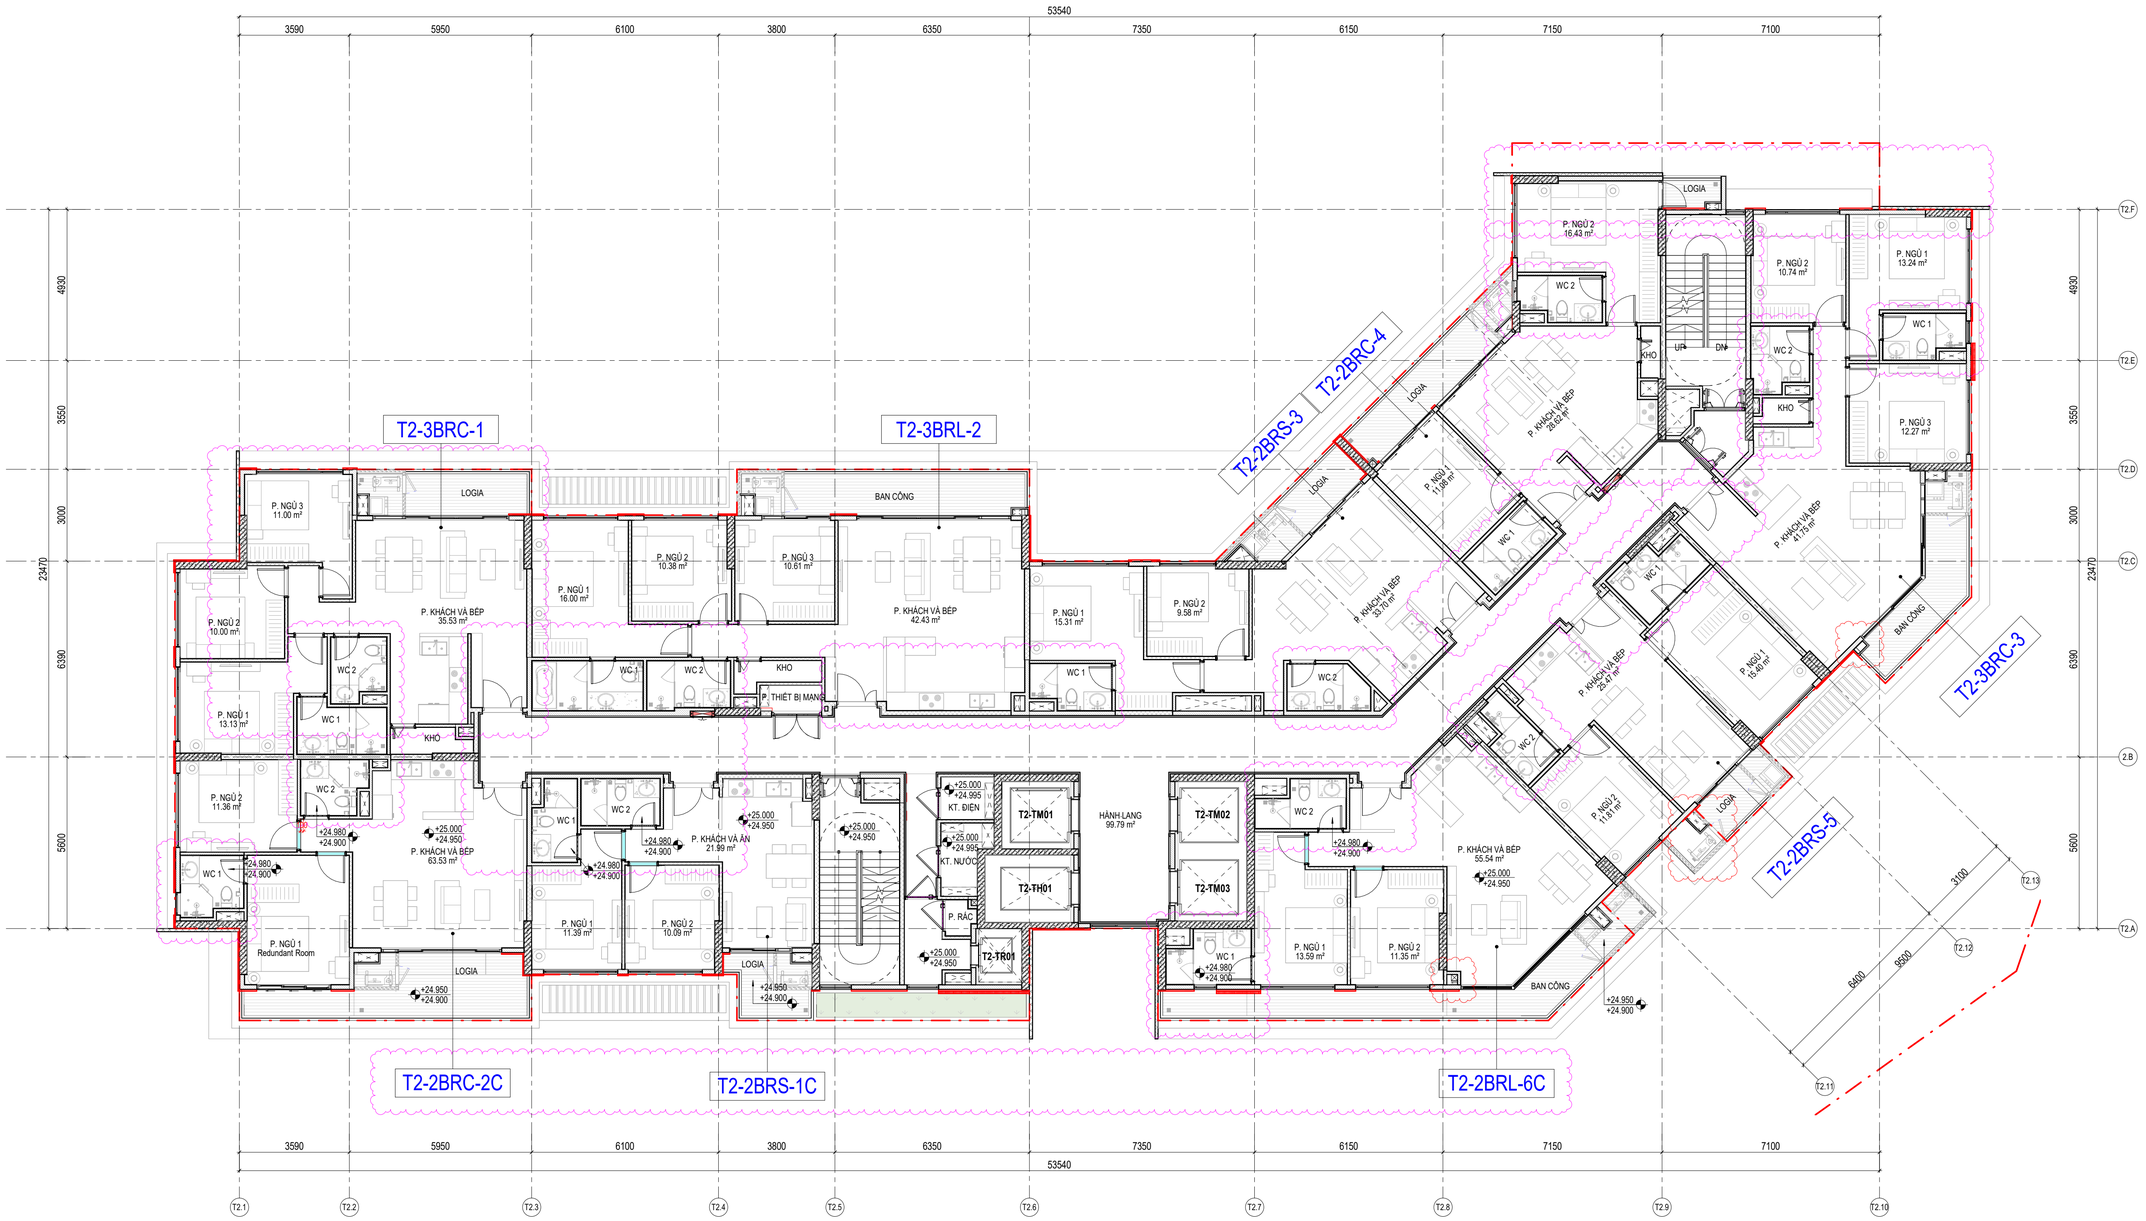

MẶT BẰNG TẦNG 6

TL: 1 : 100

DIỆN TÍCH SÀN XÂY DỰNG (GFA) :1036.00 M2

THỐNG KÊ DIỆN TÍCH TĐH 02 (TẦNG 6)

STT	Tên căn hộ	Số lượng(Căn)	Loại căn hộ(Phòng ngủ)	IFA(m²)	GFA(m²)	NSA(m²)	Số người
1	T2-2BRS-1C	1	2PN	63.46 m²	64.03 m²	57.95 m²	2
2	T2-2BRC-2C	1	2PN	90.58 m²	91.58 m²	82.33 m²	3
3	T2-2BRS-3	1	2PN	82.88 m²	83.44 m²	74.97 m²	3
4	T2-2BRC-4	1	2PN	86.67 m²	87.52 m²	79.71 m²	3
5	T2-2BRS-5	1	2PN	73.73 m²	74.30 m²	67.61 m²	3
6	T2-2BRL-6C	1	2PN	98.98 m²	99.33 m²	87.87 m²	3
7	T2-3BRC-1	1	3PN	98.18 m²	99.69 m²	91.13 m²	4
8	T2-3BRL-2	1	3PN	116.06 m²	116.85 m²	107.38 m²	4
9	T2-3BRC-3	1	3PN	107.98 m²	109.55 m²	99.67 m²	4
TỔNG		9		818.52 m²	826.29 m²	748.64 m²	29

PHIÊN BẢN	NỘI DUNG ĐIỀU CHỈNH	NGÀY NỘP

GHI CHÚ:

- CỐT +0.000 LẤY TẠI SÀN HOÀN THIỆN TẦNG 1 CÔNG TRÌNH TƯƠNG ĐƯƠNG COTE TUYỆT ĐỐI +7.900 (HỆ TỌA ĐỘ VN-2000)

- TÒA 1 CHIỀU CAO CÔNG TRÌNH TÍNH TỪ:
  + COTE HOÀN THIỆN +0.000: 43M
  + COTE NỀN TỰ NHIÊN THẤP NHẤT -1.000: 44M
- TÒA 2 CHIỀU CAO CÔNG TRÌNH TÍNH TỪ:
  + COTE HOÀN THIỆN +0.000: 50M
  + COTE NỀN TỰ NHIÊN THẤP NHẤT -1.000: 51M
- TÒA 3 CHIỀU CAO CÔNG TRÌNH TÍNH TỪ:
  + COTE HOÀN THIỆN +0.000: 59M
  + COTE NỀN TỰ NHIÊN THẤP NHẤT -1.000: 60M

- KHU VỰC TMDV BÀN GIAO THÔ, VỆ SINH KHÔNG XÂY, CHỈ BỐ TRÍ LAYOUT ĐỊNH HƯỚNG ĐẶT CÁC ĐẦU CHỜ.

- TỶ LỆ SỬ DỤNG VẬT LIỆU XANH KHÔNG NUNG ĐÁP ỨNG TỐI 90% KHỐI LƯỢNG GẠCH TRONG CÔNG TRÌNH

- TRONG PHÒNG RÁC KHÔNG BỐ TRÍ CÁC CHẤT, VẬT LIỆU CÓ KHẢ NĂNG GÂY CHÁY NỔ

- TƯỜNG NGĂN CHÁY, VÁCH NGĂN CHÁY TRONG CÁC GIAN PHÒNG ĐƯỢC NGĂN CHIA ĐẾN TRẦN BÊ TÔNG.

- VẬT LIỆU HOÀN THIỆN TRẦN, TƯỜNG, SÀN TRÊN CÁC ĐƯỜNG THOÁT NẠN, TRONG SẢNH THANG MÁY, SẢNH CHUNG, TẦNG KỸ THUẬT LÀ VẬT LIỆU KHÔNG CHÁY ĐẠT CV0

- TRONG CÁC KHÔNG GIAN TRẦN TREO KHÔNG BỐ TRÍ CÁC KÊNH, ĐƯỜNG ỐNG DẪN VẬN CHUYỂN CÁC CHẤT CHÁY DẠNG KHÍ, HỖN HỢP KHÍ, CHẤT LỎNG VÀ VẬT LIỆU CHÁY.

- TRONG CÔNG TRÌNH KHÔNG BỐ TRÍ TRẦN TREO CHO CÁC GIAN PHÒNG HẠNG A VÀ HẠNG B

- KHÔNG CÓ KÊNH, GIẾNG, ĐƯỜNG ỐNG ĐI QUA TƯỜNG NGĂN CHÁY LOẠI 1

ỐP FACADE : LÀM VIỆC VỚI TƯ VẤN FACADE

CHỦ ĐẦU TƯ / OWNER:
CÔNG TY CỔ PHẦN THƯƠNG MẠI DƯƠNG PHÚC THẮNG
DUONG PHUC THANG TRADING JOINT STOCK COMPANY
ĐỊA CHỈ / ADDRESS: Tầng 16, Tòa OSI Tower, Khu tây Hồ Tây, Phường Xuân Đỉnh, Thành phố Hà Nội, Việt Nam.
Hotline : 0243 2077 272

TƯ VẤN KIẾN TRÚC CHÍNH / MAIN ARCHITECTURAL CONSULTANT:
CÔNG TY TNHH KIẾN TRÚC DP VIỆT NAM
DP ARCHITECTS VIETNAM CO.,LTD.
ĐỊA CHỈ / ADDRESS: Tầng 4, số 82 Võ Văn Tần, Phường Xuân Hòa, TP.Hồ Chí Minh
Hotline : 0283 5357 507
Fax: 0283 5357 517
Email : dparchitects@dpa.com.sg

TƯ VẤN THIẾT KẾ / CONSULTANT:
CÔNG TY CỔ PHẦN INNO
INNO.,JSC
ĐỊA CHỈ / ADDRESS: HN: 39 Thượng Thụy, Phú Thượng, Hà Nội
HCM: 37 Nguyễn Văn Hưởng, An Khánh, TP. HCM
Hotline: 0243 212 1776 Email : ad@innojsc.com

TỔNG GIÁM ĐỐC / GENERAL DIRECTOR:
ĐOÀN VĂN ĐỘNG
CHỦ NHIỆM THIẾT KẾ / PROJECT MANAGER:
LƯU GIANG NAM
CHỦ TRÌ THIẾT KẾ / DESIGN MANAGER:
NGÔ NGỌC BÌNH
KIỂM / CHECKED BY:
VŨ TUẤN ANH
THIẾT KẾ / DESIGNER:
LÊ THỊ THANH **NGUYỄN XUÂN HIỆN**
PHƯƠNG THỊ ÁNH TUYẾT **VŨ TIẾN DƯƠNG**

TÊN DỰ ÁN / PROJECT NAME:
XÂY DỰNG NHÀ Ở TẠI LÔ ĐẤT NO-02

ĐỊA ĐIỂM XÂY DỰNG / PROJECT ADDRESS:
LÔ ĐẤT NO-22, PHƯỜNG BỒ ĐỀ, HÀ NỘI

HẠNG MỤC / ITEM:
KIẾN TRÚC

HOÀN THÀNH / FINISHED DATE:	MÃ SỐ DỰ ÁN / PROJECT No:
TKCS	2501
HOÀN THÀNH / FINISHED DATE: 2026	PHIÊN BẢN / REVISION: 3

TÊN BẢN VẼ / SHEET NAME:
MẶT BẰNG TẦNG 6

SỐ HIỆU BẢN VẼ / SHEET NUMBER:
A.2-01.105

© 2025 - INNO.,jsc

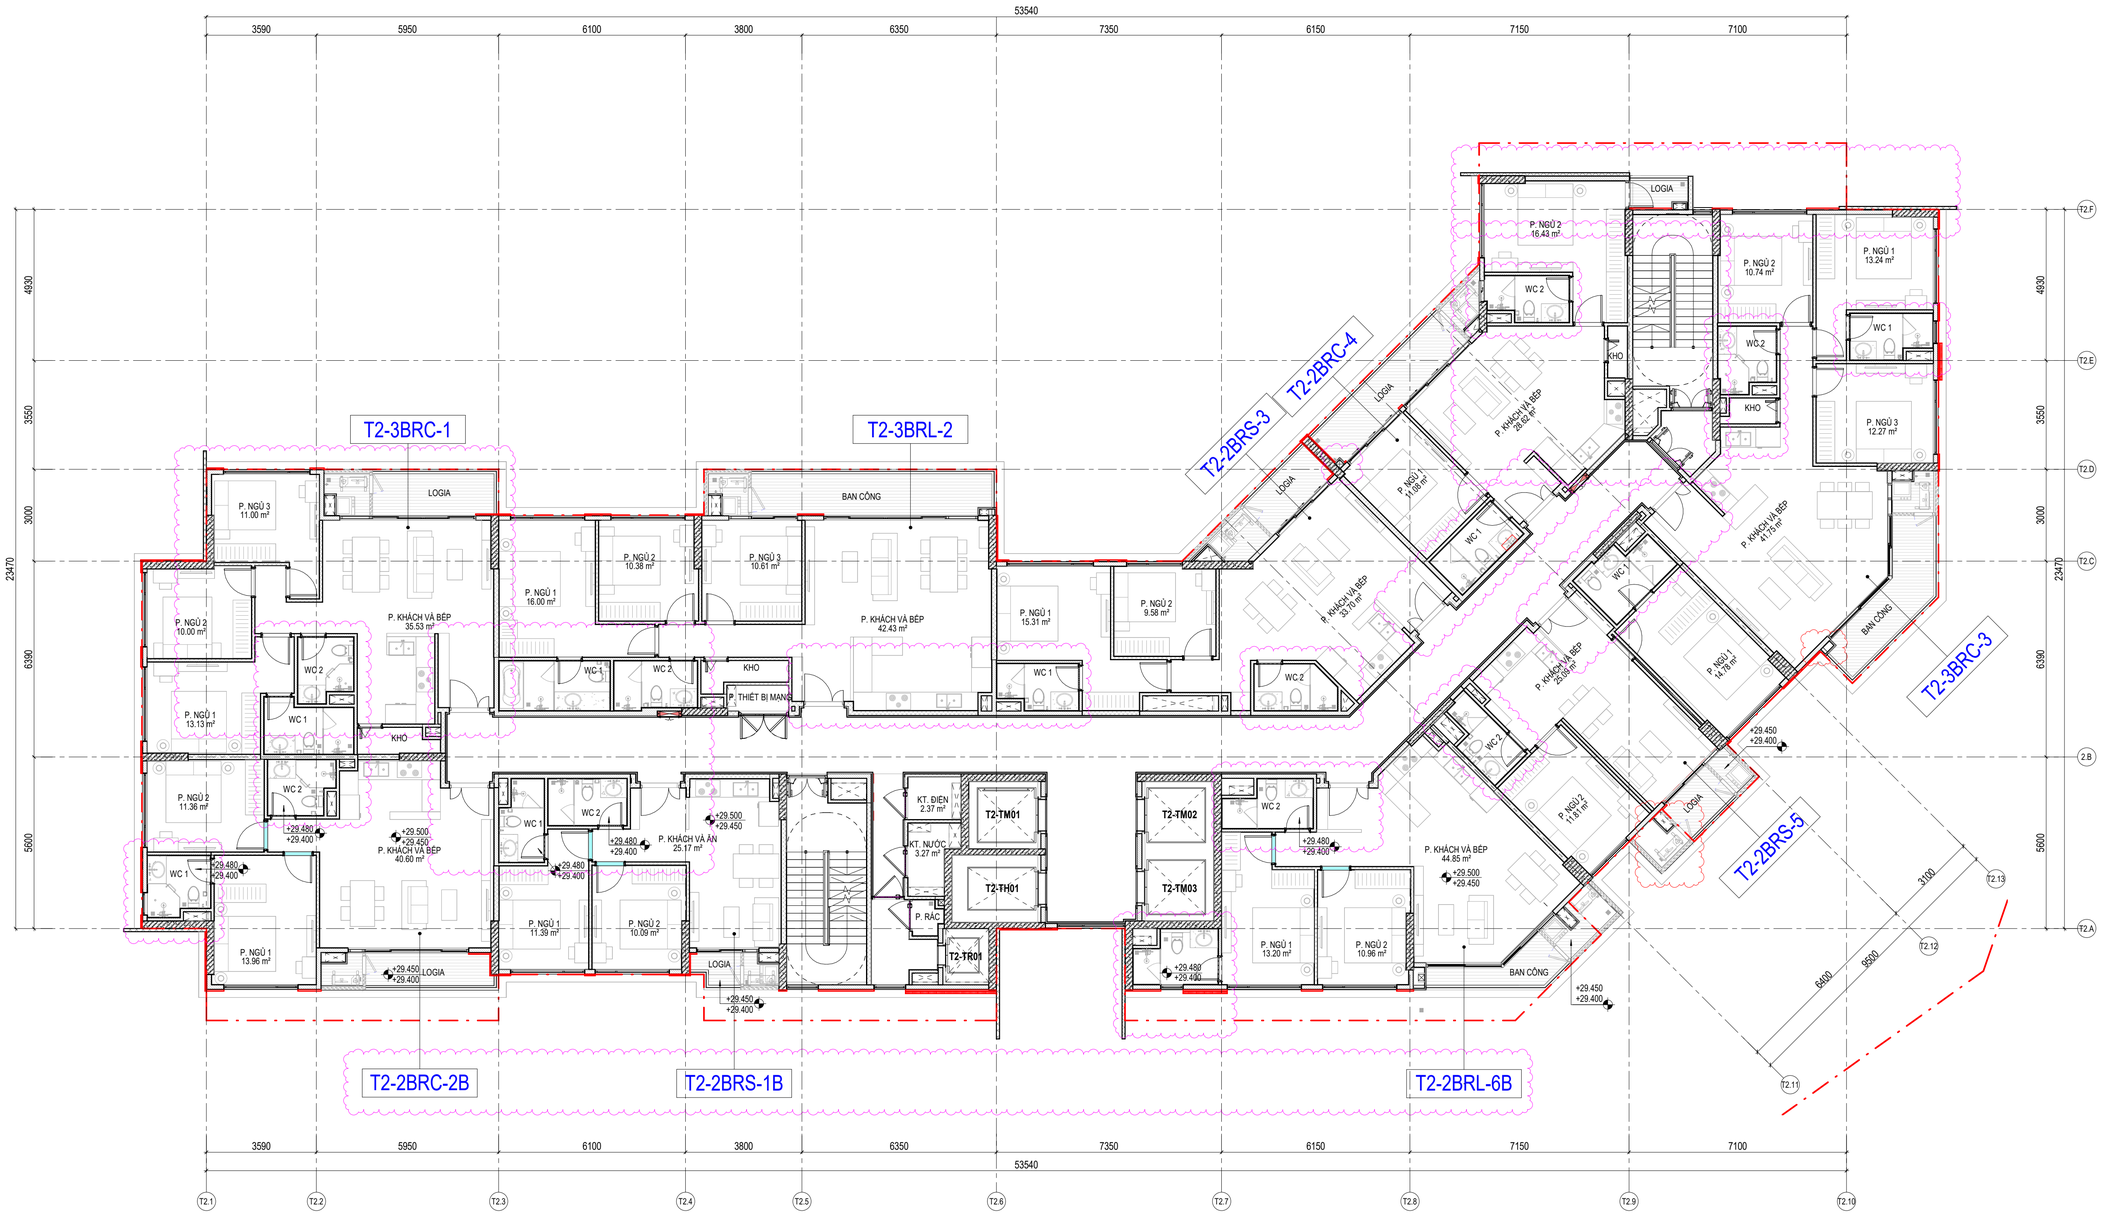

MẶT BẰNG TẦNG 7-8

TL: 1 : 100

DIỆN TÍCH SÀN XÂY DỰNG (GFA) :1003.63 M2

THỐNG KÊ DIỆN TÍCH TĐH 03 (TẦNG 7-8)

STT	Tên căn hộ	Số lượng(Căn)	Loại căn hộ(Phòng ngủ)	IFA(m²)	GFA(m²)	NSA(m²)	Số người
1	T2-2BRS-1B	1	2PN	60.96 m²	61.53 m²	55.74 m²	2
2	T2-2BRC-2B	1	2PN	80.71 m²	82.04 m²	73.71 m²	3
3	T2-2BRS-3	1	2PN	82.88 m²	83.44 m²	74.95 m²	3
4	T2-2BRC-4	1	2PN	86.67 m²	87.52 m²	79.77 m²	3
5	T2-2BRS-5	1	2PN	73.73 m²	74.30 m²	67.63 m²	3
6	T2-2BRL-6B	1	2PN	84.90 m²	86.09 m²	78.32 m²	3
7	T2-3BRC-1	1	3PN	98.18 m²	99.69 m²	91.13 m²	4
8	T2-3BRL-2	1	3PN	116.06 m²	116.85 m²	107.38 m²	4
9	T2-3BRC-3	1	3PN	107.98 m²	109.55 m²	99.67 m²	4
TỔNG		9		792.07 m²	801.01 m²	728.31 m²	29

PHIÊN BẢN	NỘI DUNG ĐIỀU CHỈNH	NGÀY NỘP

GHI CHÚ:

- CỐT +0.000 LẤY TẠI SÀN HOÀN THIỆN TẦNG 1 CÔNG TRÌNH TƯƠNG ĐƯƠNG COTE TUYỆT ĐỐI +7.900 (HỆ TỌA ĐỘ VN-2000)

- TÒA 1 CHIỀU CAO CÔNG TRÌNH TÍNH TỪ:
  + COTE HOÀN THIỆN +0.000: 43M
  + COTE NỀN TỰ NHIÊN THẤP NHẤT -1.000: 44M
- TÒA 2 CHIỀU CAO CÔNG TRÌNH TÍNH TỪ:
  + COTE HOÀN THIỆN +0.000: 50M
  + COTE NỀN TỰ NHIÊN THẤP NHẤT -1.000: 51M
- TÒA 3 CHIỀU CAO CÔNG TRÌNH TÍNH TỪ:
  + COTE HOÀN THIỆN +0.000: 59M
  + COTE NỀN TỰ NHIÊN THẤP NHẤT -1.000: 60M

- KHU VỰC TMDV BÀN GIAO THÔ, VỆ SINH KHÔNG XÂY, CHỈ BỐ TRÍ LAYOUT ĐỊNH HƯỚNG ĐẶT CÁC ĐẦU CHỜ.

- TỶ LỆ SỬ DỤNG VẬT LIỆU XANH KHÔNG NUNG ĐÁP ỨNG TỚI 90% KHỐI LƯỢNG GẠCH TRONG CÔNG TRÌNH

- TRONG PHÒNG RÁC KHÔNG BỐ TRÍ CÁC CHẤT, VẬT LIỆU CÓ KHẢ NĂNG GÂY CHÁY NỔ

- TƯỜNG NGĂN CHÁY, VÁCH NGĂN CHÁY TRONG CÁC GIAN PHÒNG ĐƯỢC NGĂN CHIA ĐẾN TRẦN BÊ TÔNG.

- VẬT LIỆU HOÀN THIỆN TRẦN, TƯỜNG, SÀN TRÊN CÁC ĐƯỜNG THOÁT NẠN, TRONG SẢNH THANG MÁY, SẢNH CHUNG, TẦNG KỸ THUẬT LÀ VẬT LIỆU KHÔNG CHÁY ĐẠT CV0

- TRONG CÁC KHÔNG GIAN TRẦN TREO KHÔNG BỐ TRÍ CÁC KÊNH, ĐƯỜNG ỐNG DẪN VẬN CHUYỂN CÁC CHẤT CHÁY DẠNG KHÍ, HỖN HỢP KHÍ, CHẤT LỎNG VÀ VẬT LIỆU CHÁY.

- TRONG CÔNG TRÌNH KHÔNG BỐ TRÍ TRẦN TREO CHO CÁC GIAN PHÒNG HẠNG A VÀ HẠNG B

- KHÔNG CÓ KÊNH, GIẾNG, ĐƯỜNG ỐNG ĐI QUA TƯỜNG NGĂN CHÁY LOẠI 1

ỐP FACADE : LÀM VIỆC VỚI TƯ VẤN FACADE

CHỦ ĐẦU TƯ / OWNER:
CÔNG TY CỔ PHẦN THƯƠNG MẠI DƯƠNG PHÚC THẮNG
DUONG PHUC THANG TRADING JOINT STOCK COMPANY
ĐỊA CHỈ / ADDRESS: Tầng 16, Tòa OSI Tower, Khu tây Hồ Tây, Phường Xuân Đỉnh, Thành phố Hà Nội, Việt Nam.
Hotline : 0243 2077 272

TƯ VẤN KIẾN TRÚC CHÍNH / MAIN ARCHITECTURAL CONSULTANT:
CÔNG TY TNHH KIẾN TRÚC DP VIỆT NAM
DP ARCHITECTS VIETNAM CO.,LTD.
ĐỊA CHỈ / ADDRESS: Tầng 4, số 82 Võ Văn Tần, Phường Xuân Hòa, TP.Hồ Chí Minh
Hotline : 0283 5357 507
Fax: 0283 5357 517
Email : dparchitects@dpa.com.sg

TƯ VẤN THIẾT KẾ / CONSULTANT:
CÔNG TY CỔ PHẦN INNO
INNO.,JSC
ĐỊA CHỈ / ADDRESS: HN: 39 Thượng Thụy, Phú Thượng, Hà Nội
HCM: 37 Nguyễn Văn Hưởng, An Khánh, TP. HCM
Hotline: 0243 212 1776 Email : ad@innojsc.com

TỔNG GIÁM ĐỐC / GENERAL DIRECTOR: **ĐOÀN VĂN ĐỘNG**
CHỦ NHIỆM THIẾT KẾ / PROJECT MANAGER: **LƯU GIANG NAM**
CHỦ TRÌ THIẾT KẾ / DESIGN MANAGER: **NGÔ NGỌC BÌNH**
KIỂM / CHECKED BY: **VŨ TUẤN ANH**
THIẾT KẾ / DESIGNER: **LÊ THỊ THANH**, **NGUYỄN XUÂN HIỆN**, **PHƯƠNG THỊ ÁNH TUYẾT**, **VŨ TIẾN DƯƠNG**

TÊN DỰ ÁN / PROJECT NAME:
XÂY DỰNG NHÀ Ở TẠI LÔ ĐẤT NO-02

ĐỊA ĐIỂM XÂY DỰNG / PROJECT ADDRESS:
LÔ ĐẤT NO-22, PHƯỜNG BỒ ĐỀ, HÀ NỘI

HẠNG MỤC / ITEM: KIẾN TRÚC

HOÀN THÀNH / FINISHED DATE:	MÃ SỐ DỰ ÁN / PROJECT No:
TKCS	2501
HOÀN THÀNH / FINISHED DATE: 2026	PHIÊN BẢN / REVISION: 3

TÊN BẢN VẼ / SHEET NAME: **MẶT BẰNG TẦNG 7-8**

SỐ HIỆU BẢN VẼ / SHEET NUMBER: **A.2-01.106**

© 2025 - INNO.,jsc

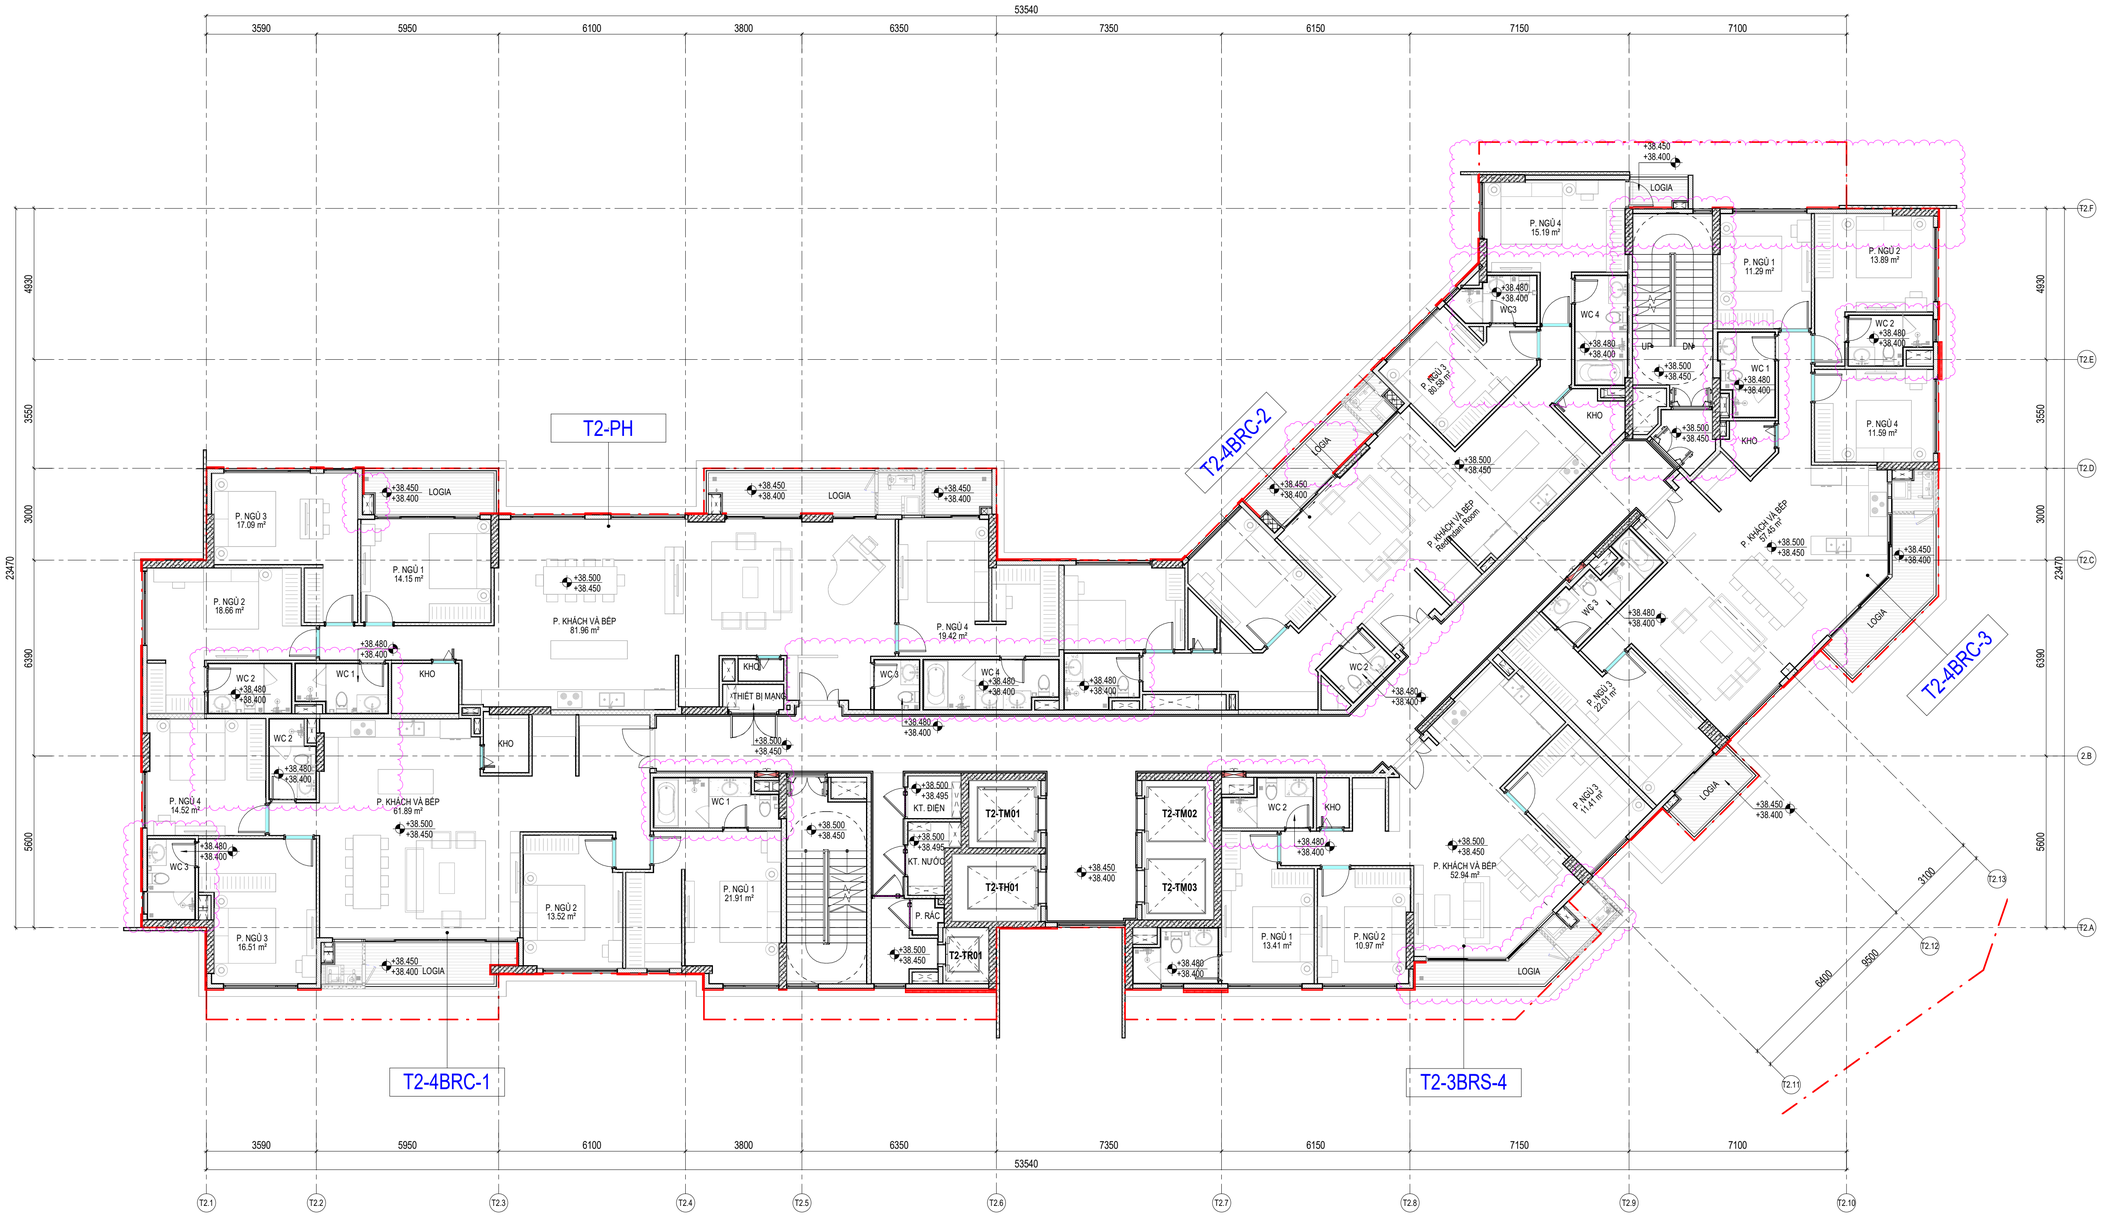

MẶT BẰNG TẦNG 9

TL: 1 : 100

DIỆN TÍCH SÀN XÂY DỰNG (GFA) :1003.63 M2

THỐNG KÊ DIỆN TÍCH TĐH04 (TẦNG 9)

STT	Tên căn hộ	Số lượng(căn)	Loại căn hộ(Phòng ngủ)	IFA(m²)	GFA(m²)	NSA(m²)	Số người
1	T2-3BRS-4	1	3PN	108.62 m²	109.83 m²	101.28 m²	4
2	T2-4BRC-1	1	4PN	168.81 m²	171.26 m²	158.96 m²	5
3	T2-4BRC-2	1	4PN	158.52 m²	160.49 m²	145.72 m²	5
4	T2-4BRC-3	1	4PN	158.43 m²	160.29 m²	146.51 m²	5
5	T2-PH	1	PH	212.38 m²	215.00 m²	198.50 m²	5
TỔNG		5		806.76 m²	816.87 m²	750.97 m²	24

PHIÊN BẢN	NỘI DUNG ĐIỀU CHỈNH	NGÀY NỘP

GHI CHÚ:

- CỐT +0.000 LẤY TẠI SÀN HOÀN THIỆN TẦNG 1 CÔNG TRÌNH TƯƠNG ĐƯƠNG COTE TUYỆT ĐỐI +7.900 (HỆ TỌA ĐỘ VN-2000)

- TÒA 1 CHIỀU CAO CÔNG TRÌNH TÍNH TỪ:
  + COTE HOÀN THIỆN +0.000: 43M
  + COTE NỀN TỰ NHIÊN THẤP NHẤT -1.000: 44M
- TÒA 2 CHIỀU CAO CÔNG TRÌNH TÍNH TỪ:
  + COTE HOÀN THIỆN +0.000: 50M
  + COTE NỀN TỰ NHIÊN THẤP NHẤT -1.000: 51M
- TÒA 3 CHIỀU CAO CÔNG TRÌNH TÍNH TỪ:
  + COTE HOÀN THIỆN +0.000: 59M
  + COTE NỀN TỰ NHIÊN THẤP NHẤT -1.000: 60M

- KHU VỰC TMDV BÀN GIAO THÔ, VỆ SINH KHÔNG XÂY, CHỈ BỐ TRÍ LAYOUT ĐỊNH HƯỚNG ĐẶT CÁC ĐẦU CHỜ.

- TỶ LỆ SỬ DỤNG VẬT LIỆU XANH KHÔNG NUNG ĐÁP ỨNG TỚI 90% KHỐI LƯỢNG GẠCH TRONG CÔNG TRÌNH

- TRONG PHÒNG RÁC KHÔNG BỐ TRÍ CÁC CHẤT, VẬT LIỆU CÓ KHẢ NĂNG GÂY CHÁY NỔ

- TƯỜNG NGĂN CHÁY, VÁCH NGĂN CHÁY TRONG CÁC GIAN PHÒNG ĐƯỢC NGĂN CHIA ĐẾN TRẦN BÊ TÔNG.

- VẬT LIỆU HOÀN THIỆN TRẦN, TƯỜNG, SÀN TRÊN CÁC ĐƯỜNG THOÁT NẠN, TRONG SẢNH THANG MÁY, SẢNH CHUNG, TẦNG KỸ THUẬT LÀ VẬT LIỆU KHÔNG CHÁY ĐẠT CV0

- TRONG CÁC KHÔNG GIAN TRẦN TREO KHÔNG BỐ TRÍ CÁC KÊNH, ĐƯỜNG ỐNG DẪN VẬN CHUYỂN CÁC CHẤT CHÁY DẠNG KHÍ, HỖN HỢP KHÍ, CHẤT LỎNG VÀ VẬT LIỆU CHÁY.

- TRONG CÔNG TRÌNH KHÔNG BỐ TRÍ TRẦN TREO CHO CÁC GIAN PHÒNG HẠNG A VÀ HẠNG B

- KHÔNG CÓ KÊNH, GIẾNG, ĐƯỜNG ỐNG ĐI QUA TƯỜNG NGĂN CHÁY LOẠI 1

ỐP FACADE : LÀM VIỆC VỚI TƯ VẤN FACADE

CHỦ ĐẦU TƯ / OWNER:
CÔNG TY CỔ PHẦN THƯƠNG MẠI DƯƠNG PHÚC THẮNG
DUONG PHUC THANG TRADING JOINT STOCK COMPANY
ĐỊA CHỈ / ADDRESS:
Tầng 16, Tòa OSI Tower, Khu tây Hồ Tây, Phường Xuân Đỉnh, Thành phố Hà Nội, Việt Nam.
Hotline : 0243 2077 272

TƯ VẤN KIẾN TRÚC CHÍNH / MAIN ARCHITECTURAL CONSULTANT:
CÔNG TY TNHH KIẾN TRÚC DP VIỆT NAM
DP ARCHITECTS VIETNAM CO.,LTD.
ĐỊA CHỈ / ADDRESS:
Tầng 4, số 82 Võ Văn Tần, Phường Xuân Hòa, TP.Hồ Chí Minh
Hotline : (0283 5357 507
Fax: (0283 5357 517
Email : dparchitects@dpa.com.sg

TƯ VẤN THIẾT KẾ / CONSULTANT:
CÔNG TY CỔ PHẦN INNO
INNO.,JSC
ĐỊA CHỈ / ADDRESS
HN: 39 Thượng Thụy, Phú Thượng, Hà Nội
HCM: 37 Nguyễn Văn Hưởng, An Khánh, TP. HCM
Hotline: 0243 212 1776 Email : ad@innojsc.com

TỔNG GIÁM ĐỐC / GENERAL DIRECTOR:
ĐOÀN VĂN ĐỘNG
CHỦ NHIỆM THIẾT KẾ / PROJECT MANAGER:
LƯU GIANG NAM
CHỦ TRÌ THIẾT KẾ / DESIGN MANAGER:
NGÔ NGỌC BÌNH
KIỂM / CHECKED BY:
VŨ TUẤN ANH
THIẾT KẾ / DESIGNER:
LÊ THỊ THANH **NGUYỄN XUÂN HIỆN**
PHƯƠNG THỊ ÁNH TUYẾT **VŨ TIẾN DƯƠNG**

TÊN DỰ ÁN / PROJECT NAME:
XÂY DỰNG NHÀ Ở TẠI LÔ ĐẤT NO-02

ĐỊA ĐIỂM XÂY DỰNG / PROJECT ADDRESS:
LÔ ĐẤT NO-22, PHƯỜNG BỒ ĐỀ, HÀ NỘI

HẠNG MỤC / ITEM:
KIẾN TRÚC

HOÀN THÀNH / FINISHED DATE:	MÃ SỐ DỰ ÁN / PROJECT No:
TKCS	2501
HOÀN THÀNH / FINISHED DATE: 2026	PHIÊN BẢN / REVISION: 2

TÊN BẢN VẼ / SHEET NAME:
MẶT BẰNG TẦNG 9

SỐ HIỆU BẢN VẼ / SHEET NUMBER:
A.2-01.107

© 2025 - INNO.,jsc

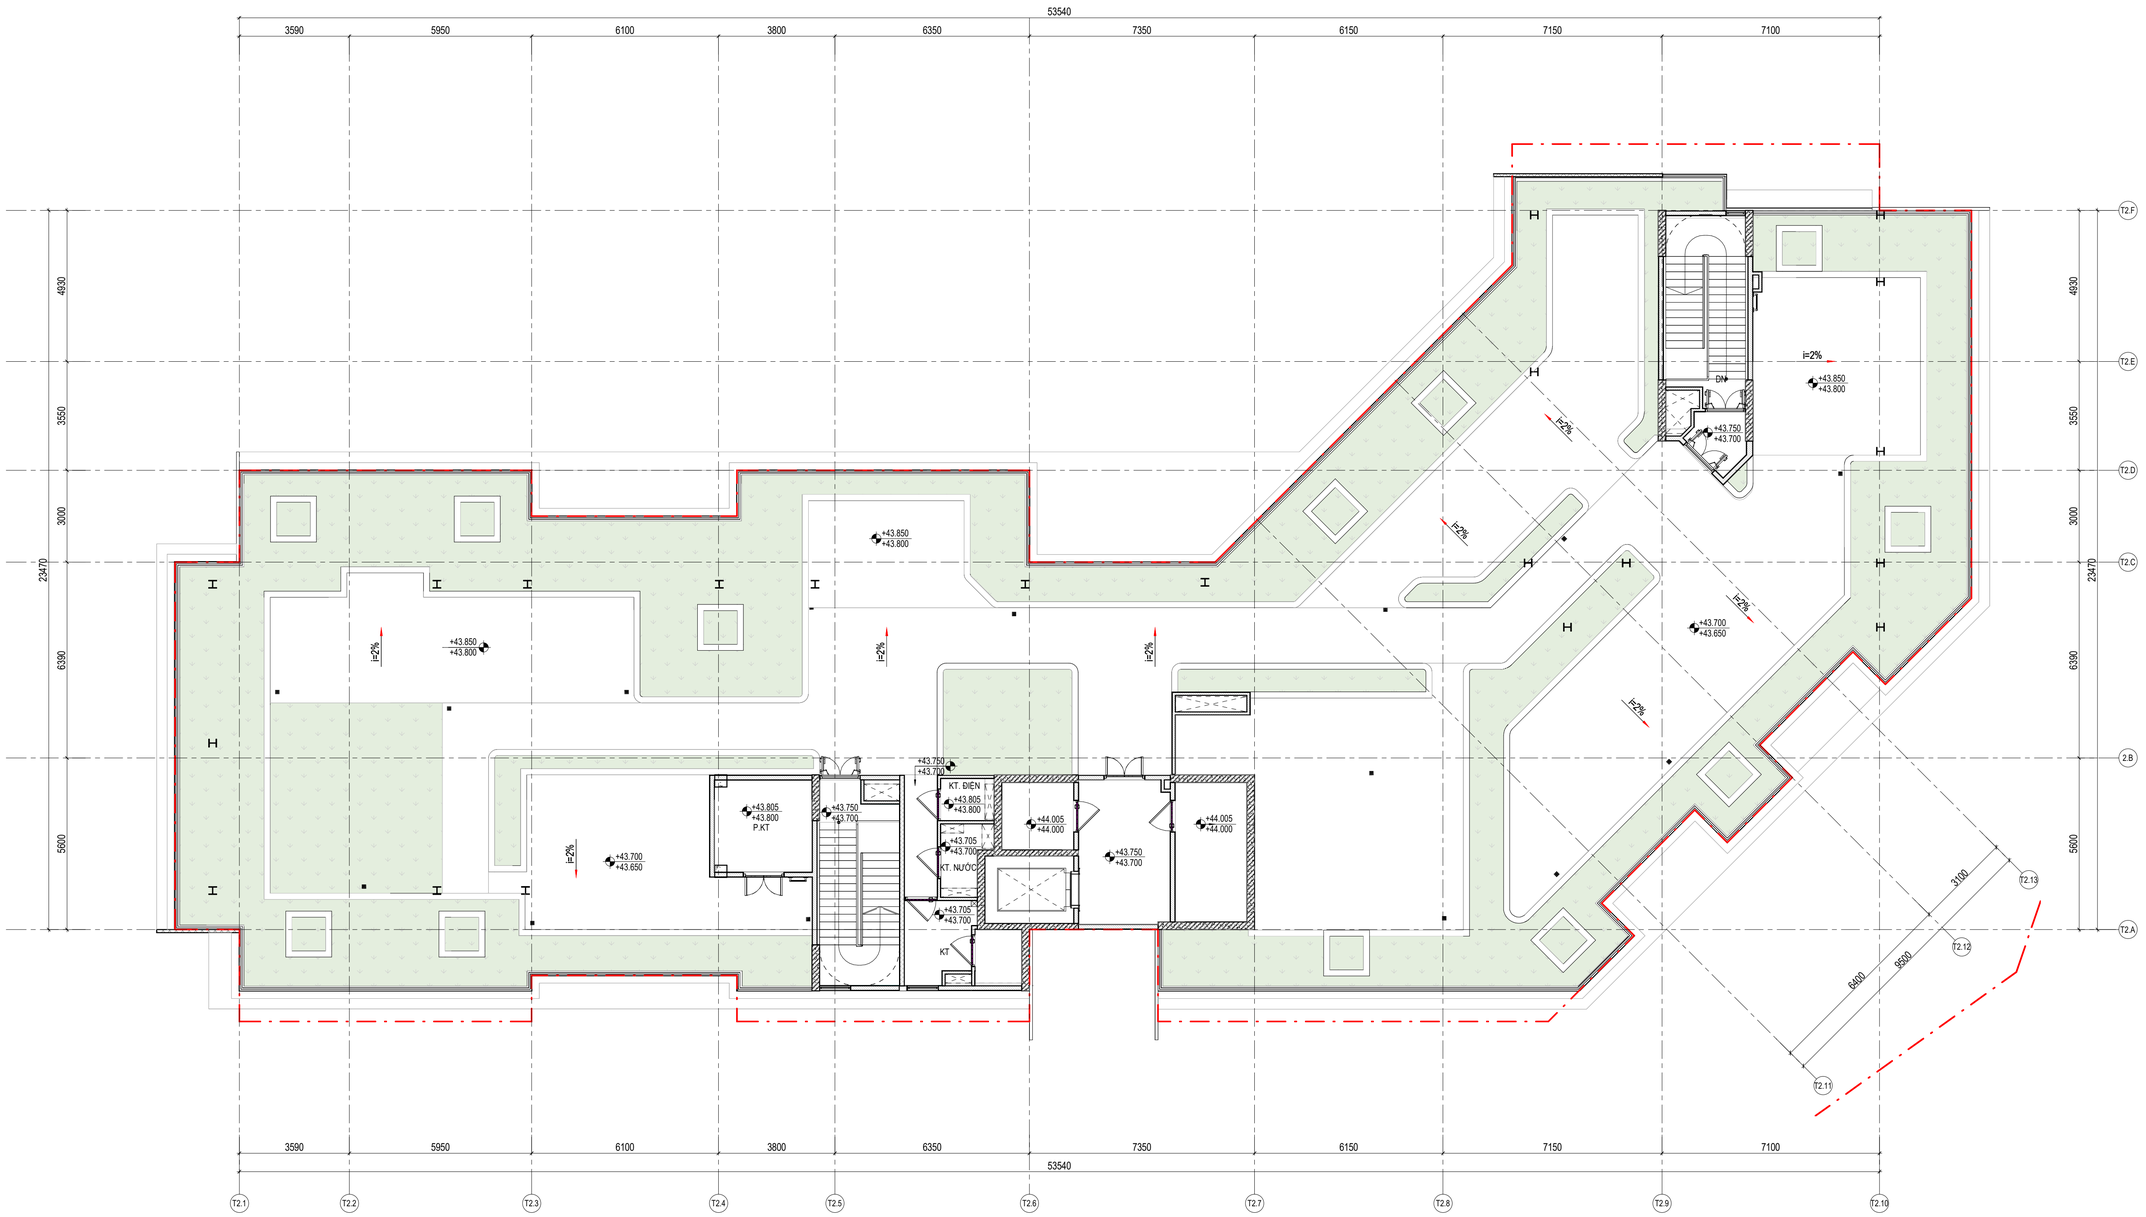

MẶT BẰNG TẦNG TUM

TL: 1 : 100

PHIÊN BẢN	NỘI DUNG ĐIỀU CHỈNH	NGÀY NỘP

GHI CHÚ:

- CỐT +0.000 LẤY TẠI SÀN HOÀN THIỆN TẦNG 1 CÔNG TRÌNH TƯƠNG ĐƯƠNG COTE TUYỆT ĐỐI +7.900 (HỆ TỌA ĐỘ VN-2000)

- TÒA 1 CHIỀU CAO CÔNG TRÌNH TÍNH TỪ:
  + COTE HOÀN THIỆN +0.000: 43M
  + COTE NỀN TỰ NHIÊN THẤP NHẤT -1.000: 44M
- TÒA 2 CHIỀU CAO CÔNG TRÌNH TÍNH TỪ:
  + COTE HOÀN THIỆN +0.000: 50M
  + COTE NỀN TỰ NHIÊN THẤP NHẤT -1.000: 51M
- TÒA 3 CHIỀU CAO CÔNG TRÌNH TÍNH TỪ:
  + COTE HOÀN THIỆN +0.000: 59M
  + COTE NỀN TỰ NHIÊN THẤP NHẤT -1.000: 60M

- KHU VỰC TMDV BÀN GIAO THÔ, VỆ SINH KHÔNG XÂY, CHỈ BỐ TRÍ LAYOUT ĐỊNH HƯỚNG ĐẶT CÁC ĐẦU CHỜ.

- TỶ LỆ SỬ DỤNG VẬT LIỆU XANH KHÔNG NUNG ĐÁP ỨNG TỚI 90% KHỐI LƯỢNG GẠCH TRONG CÔNG TRÌNH

- TRONG PHÒNG RÁC KHÔNG BỐ TRÍ CÁC CHẤT, VẬT LIỆU CÓ KHẢ NĂNG GÂY CHÁY NỔ

- TƯỜNG NGĂN CHÁY, VÁCH NGĂN CHÁY TRONG CÁC GIAN PHÒNG ĐƯỢC NGĂN CHIA ĐẾN TRẦN BÊ TÔNG.

- VẬT LIỆU HOÀN THIỆN TRẦN, TƯỜNG, SÀN TRÊN CÁC ĐƯỜNG THOÁT NẠN, TRONG SẢNH THANG MÁY, SẢNH CHUNG, TẦNG KỸ THUẬT LÀ VẬT LIỆU KHÔNG CHÁY ĐẠT CV0

- TRONG CÁC KHÔNG GIAN TRẦN TREO KHÔNG BỐ TRÍ CÁC KÊNH, ĐƯỜNG ỐNG DẪN VẬN CHUYỂN CÁC CHẤT CHÁY DẠNG KHÍ, HỖN HỢP KHÍ, CHẤT LỎNG VÀ VẬT LIỆU CHÁY.

- TRONG CÔNG TRÌNH KHÔNG BỐ TRÍ TRẦN TREO CHO CÁC GIAN PHÒNG HẠNG A VÀ HẠNG B

- KHÔNG CÓ KÊNH, GIẾNG, ĐƯỜNG ỐNG ĐI QUA TƯỜNG NGĂN CHÁY LOẠI 1

CHỦ ĐẦU TƯ / OWNER:
CÔNG TY CỔ PHẦN THƯƠNG MẠI DƯƠNG PHÚC THẮNG
DUONG PHUC THANG TRADING JOINT STOCK COMPANY

ĐỊA CHỈ / ADDRESS:
Tầng 16, Toà Citi Tower, Khu tây Hồ Tây, Phường Xuân Đỉnh, Thành phố Hà Nội, Việt Nam.
Hotline : 0243 2077 272

TƯ VẤN KIẾN TRÚC CHÍNH / MAIN ARCHITECTURAL CONSULTANT:
CÔNG TY TNHH KIẾN TRÚC DP VIỆT NAM
DP ARCHITECTS VIETNAM CO.,LTD.

ĐỊA CHỈ / ADDRESS:
Tầng 4, số 82 Võ Văn Tần, Phường Xuân Hòa, TP.Hồ Chí Minh
Hotline : 0283 5357 507
Fax: 0283 5357 517
Email : dparchitects@dpa.com.sg

TƯ VẤN THIẾT KẾ / CONSULTANT:
CÔNG TY CỔ PHẦN INNO
INNO.,JSC

ĐỊA CHỈ / ADDRESS
HN: 39 Thượng Thụy, Phú Thượng, Hà Nội
HCM: 37 Nguyễn Văn Hưởng, An Khánh, TP. HCM
Hotline: 0243 212 1776 Email : ad@innojsc.com

TỔNG GIÁM ĐỐC / GENERAL DIRECTOR:
ĐOÀN VĂN ĐỘNG

CHỦ NHIỆM THIẾT KẾ / PROJECT MANAGER:
LƯU GIANG NAM

CHỦ TRÌ THIẾT KẾ / DESIGN MANAGER:
NGÔ NGỌC BÌNH

KIỂM / CHECKED BY:
VŨ TUẤN ANH

THIẾT KẾ / DESIGNER
LÊ THỊ THANH **NGUYỄN XUÂN HIỆN**
PHƯƠNG THỊ ÁNH TUYẾT **VŨ TIẾN DƯƠNG**

TÊN DỰ ÁN / PROJECT NAME:
XÂY DỰNG NHÀ Ở TẠI LÔ ĐẤT NO-02

ĐỊA ĐIỂM XÂY DỰNG / PROJECT ADDRESS:
LÔ ĐẤT NO-22, PHƯỜNG BỒ ĐỀ, HÀ NỘI

HẠNG MỤC / ITEM:
KIẾN TRÚC

HOÀN THÀNH / FINISHED DATE:	MÃ SỐ DỰ ÁN / PROJECT No:
TKCS	2501
HOÀN THÀNH / FINISHED DATE: 2026	PHIÊN BẢN / REVISION: 2

TÊN BẢN VẼ / SHEET NAME:
MẶT BẰNG TẦNG TUM

SỐ HIỆU BẢN VẼ / SHEET NUMBER:
A.2-01.108

© 2025 - INNO.,jsc

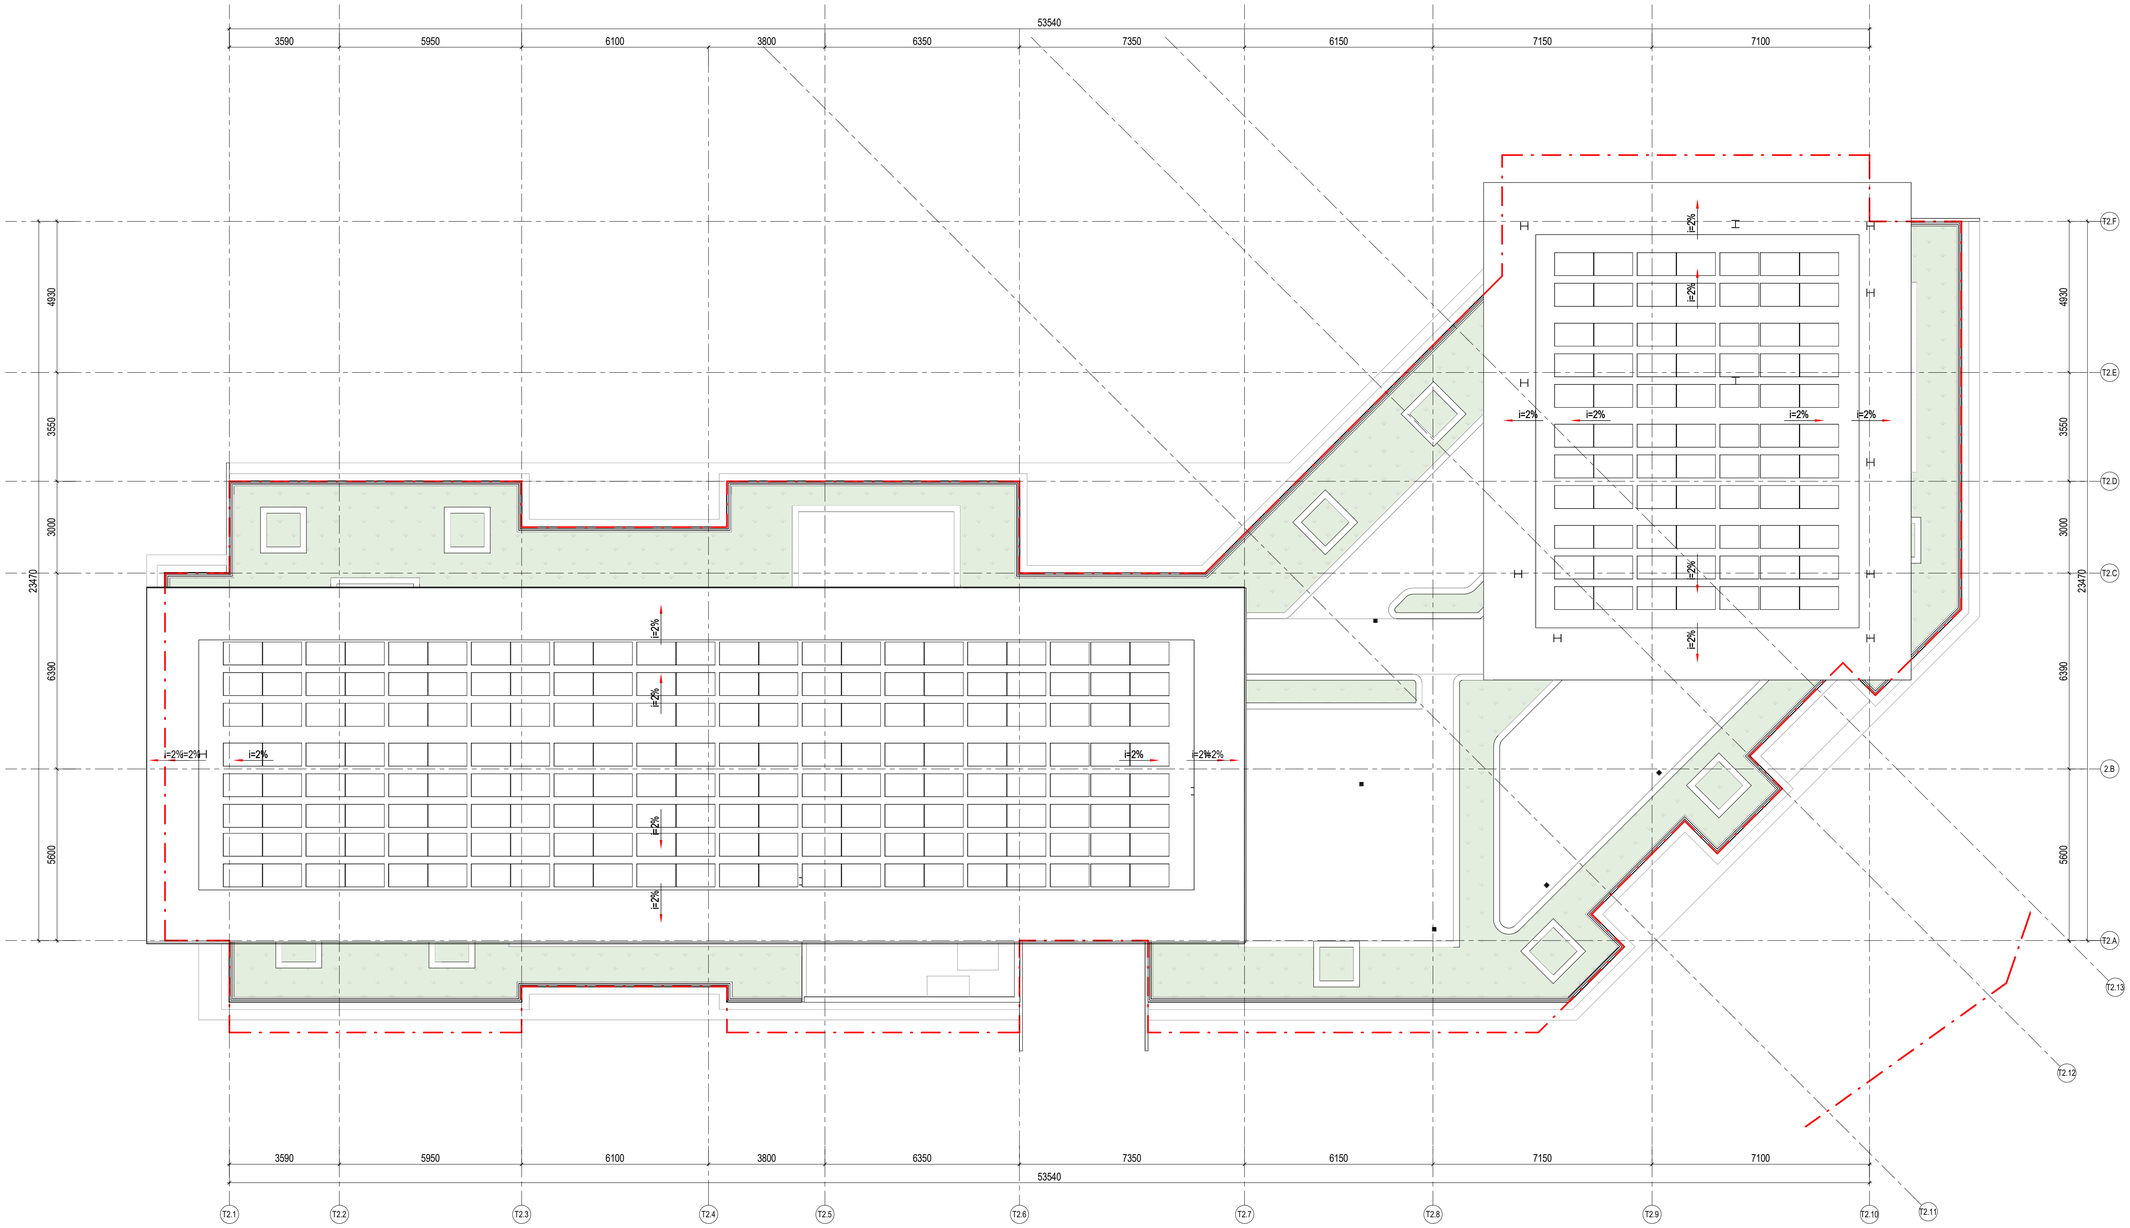

MẶT BẰNG ĐỈNH MÁI
TL: 1 : 100

PHIÊN BẢN	NỘI DUNG ĐIỀU CHỈNH	NGÀY NỘP

GHI CHÚ:

- CỐT +0.000 LẤY TẠI SÀN HOÀN THIỆN TẦNG 1 CÔNG TRÌNH TƯƠNG ĐƯƠNG COTE TUYỆT ĐỐI +7.900 (HỆ TỌA ĐỘ VN-2000)

- TÒA 1 CHIỀU CAO CÔNG TRÌNH TÍNH TỪ:
  + COTE HOÀN THIỆN +0.000: 43M
  + COTE NỀN TỰ NHIÊN THẤP NHẤT -1.000: 44M
- TÒA 2 CHIỀU CAO CÔNG TRÌNH TÍNH TỪ:
  + COTE HOÀN THIỆN +0.000: 50M
  + COTE NỀN TỰ NHIÊN THẤP NHẤT -1.000: 51M
- TÒA 3 CHIỀU CAO CÔNG TRÌNH TÍNH TỪ:
  + COTE HOÀN THIỆN +0.000: 59M
  + COTE NỀN TỰ NHIÊN THẤP NHẤT -1.000: 60M

- KHU VỰC TMDV BÀN GIAO THÔ, VỆ SINH KHÔNG XÂY, CHỈ BỐ TRÍ LAYOUT ĐỊNH HƯỚNG ĐẶT CÁC ĐẦU CHỜ.

- TỶ LỆ SỬ DỤNG VẬT LIỆU XANH KHÔNG NUNG ĐÁP ỨNG TỚI 90% KHỐI LƯỢNG GẠCH TRONG CÔNG TRÌNH

- TRONG PHÒNG RÁC KHÔNG BỐ TRÍ CÁC CHẤT, VẬT LIỆU CÓ KHẢ NĂNG GÂY CHÁY NỔ

- TƯỜNG NGĂN CHÁY, VÁCH NGĂN CHÁY TRONG CÁC GIAN PHÒNG ĐƯỢC NGĂN CHIA ĐẾN TRẦN BÊ TÔNG.

- VẬT LIỆU HOÀN THIỆN TRẦN, TƯỜNG, SÀN TRÊN CÁC ĐƯỜNG THOÁT NẠN, TRONG SẢNH THANG MÁY, SẢNH CHUNG, TẦNG KỸ THUẬT LÀ VẬT LIỆU KHÔNG CHÁY ĐẠT CV0

- TRONG CÁC KHÔNG GIAN TRẦN TREO KHÔNG BỐ TRÍ CÁC KÊNH, ĐƯỜNG ỐNG DẪN VẬN CHUYỂN CÁC CHẤT CHÁY DẠNG KHÍ, HỖN HỢP KHÍ, CHẤT LỎNG VÀ VẬT LIỆU CHÁY.

- TRONG CÔNG TRÌNH KHÔNG BỐ TRÍ TRẦN TREO CHO CÁC GIAN PHÒNG HẠNG A VÀ HẠNG B

- KHÔNG CÓ KÊNH, GIẾNG, ĐƯỜNG ỐNG ĐI QUA TƯỜNG NGĂN CHÁY LOẠI 1

CHỦ ĐẦU TƯ / OWNER:
CÔNG TY CỔ PHẦN THƯƠNG MẠI DƯƠNG PHÚC THẮNG
DUONG PHUC THANG TRADING JOINT STOCK COMPANY
ĐỊA CHỈ / ADDRESS:
Tầng 16, Tòa Oải Tower, Khu tây Hồ Tây, Phường Xuân Đỉnh, Thành phố Hà Nội, Việt Nam.
Hotline : 0243 2077 272

TƯ VẤN KIẾN TRÚC CHÍNH / MAIN ARCHITECTURAL CONSULTANT:
CÔNG TY TNHH KIẾN TRÚC DP VIỆT NAM
DP ARCHITECTS VIETNAM CO.,LTD.
ĐỊA CHỈ / ADDRESS:
Tầng 4, số 82 Võ Văn Tần, Phường Xuân Hòa, TP.Hồ Chí Minh
Hotline : 0283 5357 507
Fax: 0283 5357 517
Email : dparchitects@dpa.com.sg

TƯ VẤN THIẾT KẾ / CONSULTANT:
CÔNG TY CỔ PHẦN INNO
INNO.,JSC
ĐỊA CHỈ / ADDRESS
HN: 39 Thượng Thụy, Phú Thượng, Hà Nội
HCM: 37 Nguyễn Văn Hưởng, An Khánh, TP. HCM
Hotline: 0243 212 1776 Email : ad@innojsc.com

TỔNG GIÁM ĐỐC / GENERAL DIRECTOR:
ĐOÀN VĂN ĐỘNG
CHỦ NHIỆM THIẾT KẾ / PROJECT MANAGER:
LƯU GIANG NAM
CHỦ TRÌ THIẾT KẾ / DESIGN MANAGER:
NGÔ NGỌC BÌNH
KIỂM / CHECKED BY:
VŨ TUẤN ANH
THIẾT KẾ / DESIGNER
LÊ THỊ THANH **NGUYỄN XUÂN HIỂN**
PHƯƠNG THỊ ÁNH TUYẾT **VŨ TIẾN DƯƠNG**

TÊN DỰ ÁN / PROJECT NAME:
XÂY DỰNG NHÀ Ở TẠI LÔ ĐẤT NO-02

ĐỊA ĐIỂM XÂY DỰNG / PROJECT ADDRESS:
LÔ ĐẤT NO-22, PHƯỜNG BỒ ĐỀ, HÀ NỘI

HẠNG MỤC / ITEM:
KIẾN TRÚC

HOÀN THÀNH / FINISHED DATE:	MÃ SỐ DỰ ÁN / PROJECT No:
TKCS	2501
HOÀN THÀNH / FINISHED DATE: 2026	PHIÊN BẢN / REVISION: 2

TÊN BẢN VẼ / SHEET NAME:
MẶT BẰNG MÁI

SỐ HIỆU BẢN VẼ / SHEET NUMBER:
A.2-01.109

© 2025 - INNO.,JSC

MẶT BẰNG: THÁP 3

© 2025 - INNO Jsc

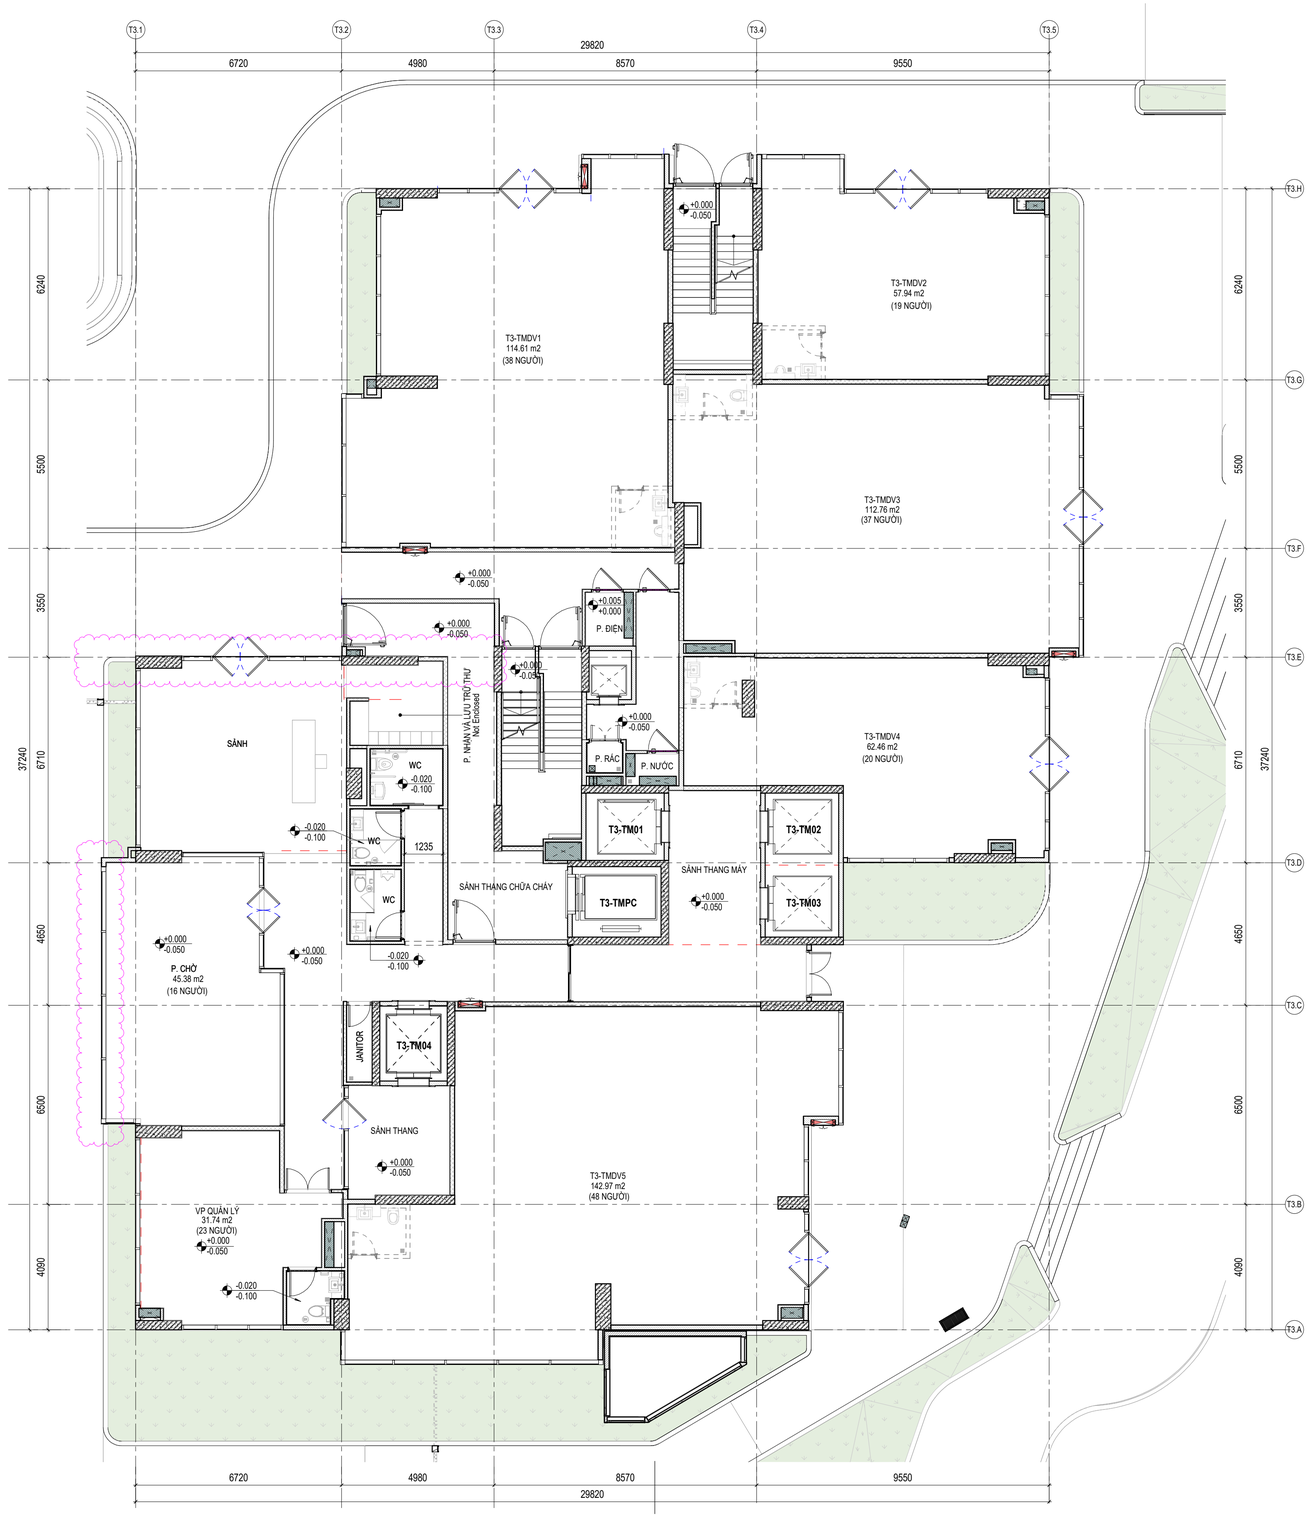

PHIÊN BẢN	NỘI DUNG ĐIỀU CHỈNH	NGÀY NỘP

GHI CHÚ:

- CỐT +0.000 LẤY TẠI SÀN HOÀN THIỆN TẦNG 1 CÔNG TRÌNH TƯƠNG ĐƯƠNG COTE TUYỆT ĐỐI +7.900 (HỆ TỌA ĐỘ VN-2000)

- TÒA 1 CHIỀU CAO CÔNG TRÌNH TÍNH TỪ:
  + COTE HOÀN THIỆN +0.000: 43M
  + COTE NỀN TỰ NHIÊN THẤP NHẤT -1.000: 44M
- TÒA 2 CHIỀU CAO CÔNG TRÌNH TÍNH TỪ:
  + COTE HOÀN THIỆN +0.000: 50M
  + COTE NỀN TỰ NHIÊN THẤP NHẤT -1.000: 51M
- TÒA 3 CHIỀU CAO CÔNG TRÌNH TÍNH TỪ:
  + COTE HOÀN THIỆN +0.000: 59M
  + COTE NỀN TỰ NHIÊN THẤP NHẤT -1.000: 60M

- KHU VỰC TMDV BÀN GIAO THÔ, VỆ SINH KHÔNG XÂY, CHỈ BỐ TRÍ LAYOUT ĐỊNH HƯỚNG ĐẶT CÁC ĐẦU CHỜ.

- TỶ LỆ SỬ DỤNG VẬT LIỆU XANH KHÔNG NUNG ĐÁP ỨNG TỚI 90% KHỐI LƯỢNG GẠCH TRONG CÔNG TRÌNH

- TRONG PHÒNG RÁC KHÔNG BỐ TRÍ CÁC CHẤT, VẬT LIỆU CÓ KHẢ NĂNG GÂY CHÁY NỔ

- TƯỜNG NGĂN CHÁY, VÁCH NGĂN CHÁY TRONG CÁC GIAN PHÒNG ĐƯỢC NGĂN CHIA ĐẾN TRẦN BÊ TÔNG.

- VẬT LIỆU HOÀN THIỆN TRẦN, TƯỜNG, SÀN TRÊN CÁC ĐƯỜNG THOÁT NẠN, TRONG SẢNH THANG MÁY, SẢNH CHUNG, TẦNG KỸ THUẬT LÀ VẬT LIỆU KHÔNG CHÁY ĐẠT CV0

- TRONG CÁC KHÔNG GIAN TRẦN TREO KHÔNG BỐ TRÍ CÁC KÊNH, ĐƯỜNG ỐNG DẪN VẬN CHUYỂN CÁC CHẤT CHÁY DẠNG KHÍ, HỖN HỢP KHÍ, CHẤT LỎNG VÀ VẬT LIỆU CHÁY.

- TRONG CÔNG TRÌNH KHÔNG BỐ TRÍ TRẦN TREO CHO CÁC GIAN PHÒNG HẠNG A VÀ HẠNG B

- KHÔNG CÓ KÊNH, GIẾNG, ĐƯỜNG ỐNG ĐI QUA TƯỜNG NGĂN CHÁY LOẠI 1

THỐNG KÊ DIỆN TÍCH TMDV TẦNG 1

STT	TMDV	IFA(m²)	GFA(m²)	NSA(m²)
1	T3-TMDV1	120.47 m²	123.61 m²	114.46 m²
2	T3-TMDV2	61.88 m²	63.30 m²	57.94 m²
3	T3-TMDV3	118.86 m²	119.79 m²	112.76 m²
4	T3-TMDV4	67.07 m²	68.52 m²	62.46 m²
5	T3-TMDV5	149.86 m²	152.54 m²	142.97 m²
TỔNG		518.15 m²	527.77 m²	490.59 m²

MẶT BẰNG TẦNG 1

TL: 1 : 100

DIỆN TÍCH SÀN XÂY DỰNG (CFA) :930.48 M2

CHỦ ĐẦU TƯ / OWNER:
CÔNG TY CỔ PHẦN THƯƠNG MẠI DƯƠNG PHÚC THẮNG
DUONG PHUC THANG TRADING JOINT STOCK COMPANY

ĐỊA CHỈ / ADDRESS:
Tầng 16, Tòa OSI Tower, Khu tây Hồ Tây, Phường Xuân Đỉnh, Thành phố Hà Nội, Việt Nam.
Hotline : 0243 2077 272

TƯ VẤN KIẾN TRÚC CHÍNH / MAIN ARCHITECTURAL CONSULTANT:
CÔNG TY TNHH KIẾN TRÚC DP VIỆT NAM
DP ARCHITECTS VIETNAM CO.,LTD.

ĐỊA CHỈ / ADDRESS:
Tầng 4, số 82 Võ Văn Tần, Phường Xuân Hòa, TP.Hồ Chí Minh
Hotline : 0283 5357 507
Fax: 0283 5357 517
Email : dparchitects@dpa.com.sg

TƯ VẤN THIẾT KẾ / CONSULTANT:
CÔNG TY CỔ PHẦN INNO
INNO.,JSC

ĐỊA CHỈ / ADDRESS
HN: 39 Thượng Thụy, Phú Thượng, Hà Nội
HCM: 37 Nguyễn Văn Hưởng, An Khánh, TP. HCM
Hotline: 0243 212 1776 Email : ad@innojsc.com

TỔNG GIÁM ĐỐC / GENERAL DIRECTOR:
ĐOÀN VĂN ĐỘNG

CHỦ NHIỆM THIẾT KẾ / PROJECT MANAGER:
LƯU GIANG NAM

CHỦ TRÌ THIẾT KẾ / DESIGN MANAGER:
NGÔ NGỌC BÌNH

KIỂM / CHECKED BY:
VŨ TUẤN ANH

THIẾT KẾ / DESIGNER
LÊ THỊ THANH **NGUYỄN XUÂN HIỆN**
PHƯƠNG THỊ ÁNH TUYẾT **VŨ TIẾN DƯƠNG**

TÊN DỰ ÁN / PROJECT NAME:
XÂY DỰNG NHÀ Ở TẠI LÔ ĐẤT NO-02

ĐỊA ĐIỂM XÂY DỰNG / PROJECT ADDRESS:
LÔ ĐẤT NO-22, PHƯỜNG BỒ ĐỀ, HÀ NỘI

HẠNG MỤC / ITEM:
KIẾN TRÚC

HOÀN THÀNH / FINISHED DATE:	MÃ SỐ DỰ ÁN / PROJECT No:
TKCS	2501
HOÀN THÀNH / FINISHED DATE: 2026	PHIÊN BẢN / REVISION: 2

TÊN BẢN VẼ / SHEET NAME:
MẶT BẰNG TẦNG 1

SỐ HIỆU BẢN VẼ / SHEET NUMBER:
A.3-01.101

© 2025 - INNO.,JSC

THỐNG KÊ DIỆN TÍCH CĂN HỘ TĐH01							
STT	Tên căn hộ	Số lượng	Loại căn hộ(Phòng ngủ)	IFA(m²)	GFA(m²)	NSA(m²)	Số người
1	T3-2BRC-1	1	2PN	97.16 m²	97.87 m²	89.50 m²	3
2	T3-3BRC-1	1	3PN	114.38 m²	116.09 m²	107.30 m²	4
3	T3-3BRC-2	1	3PN	116.78 m²	119.80 m²	110.33 m²	4
4	T3-4BRC-1	1	4PN	159.53 m²	160.90 m²	149.28 m²	5
5	T3-DUP-1	1	DUP	127.21 m²	128.92 m²	117.73 m²	5
6	T3-DUP-2	1	DUP	135.30 m²	136.37 m²	126.84 m²	5
TỔNG		6		750.35 m²	759.96 m²	700.97 m²	26

MẶT BẰNG TẦNG 2

TL: 1 : 100

DIỆN TÍCH SÀN XÂY DỰNG (CFA) :930.48 M2

PHIÊN BẢN	NỘI DUNG ĐIỀU CHỈNH	NGÀY NỘP

GHI CHÚ:

- CỐT +0.000 LẤY TẠI SÀN HOÀN THIỆN TẦNG 1 CÔNG TRÌNH TƯƠNG ĐƯƠNG COTE TUYỆT ĐỐI +7.900 (HỆ TỌA ĐỘ VN-2000)

- TÒA 1 CHIỀU CAO CÔNG TRÌNH TÍNH TỪ:
  + COTE HOÀN THIỆN +0.000: 43M
  + COTE NỀN TỰ NHIÊN THẤP NHẤT -1.000: 44M
- TÒA 2 CHIỀU CAO CÔNG TRÌNH TÍNH TỪ:
  + COTE HOÀN THIỆN +0.000: 50M
  + COTE NỀN TỰ NHIÊN THẤP NHẤT -1.000: 51M
- TÒA 3 CHIỀU CAO CÔNG TRÌNH TÍNH TỪ:
  + COTE HOÀN THIỆN +0.000: 59M
  + COTE NỀN TỰ NHIÊN THẤP NHẤT -1.000: 60M

- KHU VỰC TMDV BÀN GIAO THÔ, VỆ SINH KHÔNG XÂY, CHỈ BỐ TRÍ LAYOUT ĐỊNH HƯỚNG ĐẶT CÁC ĐẦU CHỜ.

- TỶ LỆ SỬ DỤNG VẬT LIỆU XANH KHÔNG NUNG ĐÁP ỨNG TỐI 90% KHỐI LƯỢNG GẠCH TRONG CÔNG TRÌNH

- TRONG PHÒNG RÁC KHÔNG BỐ TRÍ CÁC CHẤT, VẬT LIỆU CÓ KHẢ NĂNG GÂY CHÁY NỔ

- TƯỜNG NGĂN CHÁY, VÁCH NGĂN CHÁY TRONG CÁC GIAN PHÒNG ĐƯỢC NGĂN CHIA ĐẾN TRẦN BÊ TÔNG.

- VẬT LIỆU HOÀN THIỆN TRẦN, TƯỜNG, SÀN TRÊN CÁC ĐƯỜNG THOÁT NẠN, TRONG SẢNH THANG MÁY, SẢNH CHUNG, TẦNG KỸ THUẬT LÀ VẬT LIỆU KHÔNG CHÁY ĐẠT CV0

- TRONG CÁC KHÔNG GIAN TRẦN TREO KHÔNG BỐ TRÍ CÁC KÊNH, ĐƯỜNG ỐNG DẪN VẬN CHUYỂN CÁC CHẤT CHÁY DẠNG KHÍ, HỖN HỢP KHÍ, CHẤT LỎNG VÀ VẬT LIỆU CHÁY.

- TRONG CÔNG TRÌNH KHÔNG BỐ TRÍ TRẦN TREO CHO CÁC GIAN PHÒNG HẠNG A VÀ HẠNG B

- KHÔNG CÓ KÊNH, GIẾNG, ĐƯỜNG ỐNG ĐI QUA TƯỜNG NGĂN CHÁY LOẠI 1

ỐP FACADE : LÀM VIỆC VỚI TƯ VẤN FACADE

CHỦ ĐẦU TƯ / OWNER:
CÔNG TY CỔ PHẦN THƯƠNG MẠI DƯƠNG PHÚC THẮNG
DUONG PHUC THANG TRADING JOINT STOCK COMPANY
ĐỊA CHỈ / ADDRESS: Tầng 16, Tòa OSI Tower, Khu tây Hồ Tây, Phường Xuân Đỉnh, Thành phố Hà Nội, Việt Nam.
Hotline : 0243 2077 272

TƯ VẤN KIẾN TRÚC CHÍNH / MAIN ARCHITECTURAL CONSULTANT:
CÔNG TY TNHH KIẾN TRÚC DP VIỆT NAM
DP ARCHITECTS VIETNAM CO.,LTD.
ĐỊA CHỈ / ADDRESS: Tầng 4, số 82 Võ Văn Tần, Phường Xuân Hòa, TP.Hồ Chí Minh
Hotline : 0283 5357 507
Fax: 0283 5357 517
Email : dparchitects@dpa.com.sg

TƯ VẤN THIẾT KẾ / CONSULTANT:
CÔNG TY CỔ PHẦN INNO
INNO.,JSC
ĐỊA CHỈ / ADDRESS
HN: 39 Thượng Thụy, Phú Thượng, Hà Nội
HCM: 37 Nguyễn Văn Hưởng, An Khánh, TP. HCM
Hotline: 0243 212 1776 Email : ad@innojsc.com

TỔNG GIÁM ĐỐC / GENERAL DIRECTOR:
ĐOÀN VĂN ĐỘNG
CHỦ NHIỆM THIẾT KẾ / PROJECT MANAGER:
LƯU GIANG NAM
CHỦ TRÌ THIẾT KẾ / DESIGN MANAGER:
NGÔ NGỌC BÌNH
KIỂM / CHECKED BY:
VŨ TUẤN ANH
THIẾT KẾ / DESIGNER:
LÊ THỊ THANH
NGUYỄN XUÂN HIỆN
PHƯƠNG THỊ ÁNH TUYẾT
VŨ TIẾN DƯƠNG

TÊN DỰ ÁN / PROJECT NAME:
XÂY DỰNG NHÀ Ở TẠI LÔ ĐẤT NO-02

ĐỊA ĐIỂM XÂY DỰNG / PROJECT ADDRESS:
LÔ ĐẤT NO-22, PHƯỜNG BỒ ĐỀ, HÀ NỘI

HẠNG MỤC / ITEM:
KIẾN TRÚC

HOÀN THÀNH / FINISHED DATE:	MÃ SỐ DỰ ÁN / PROJECT No:
TKCS	2501
HOÀN THÀNH / FINISHED DATE: 2026	PHIÊN BẢN / REVISION: 2

TÊN BẢN VẼ / SHEET NAME:
MẶT BẰNG TẦNG 2

SỐ HIỆU BẢN VẼ / SHEET NUMBER:
A.3-01.102

© 2025 - INNO.,jsc

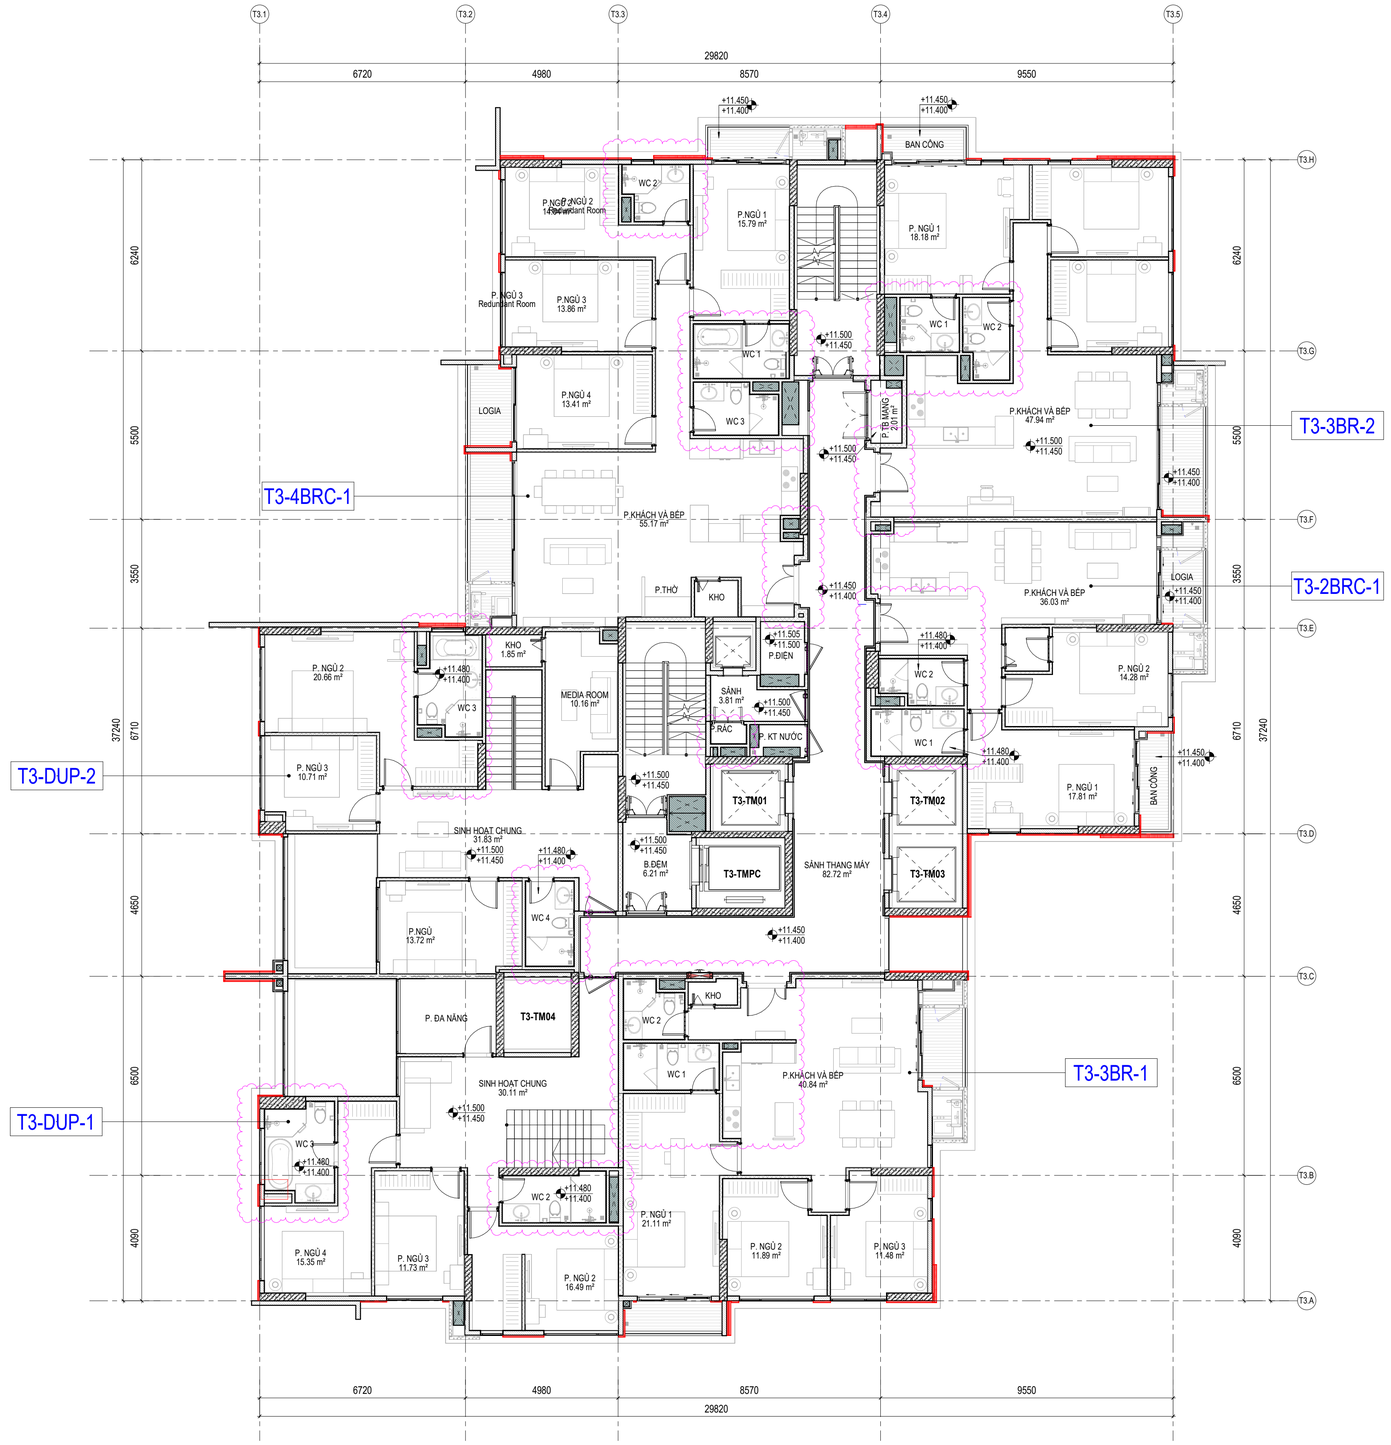

THỐNG KÊ DIỆN TÍCH CĂN HỘ TDH02							
STT	Tên căn hộ	Số lượng	Loại căn hộ(phòng ngủ)	IFA(m²)	GFA(m²)	NSA(m²)	Số người
1	T3-2BRC-1	1	2PN	97.16 m²	97.87 m²	89.50 m²	3
2	T3-3BR-1	1	3PN	114.38 m²	115.88 m²	107.26 m²	4
3	T3-3BR-2	1	3PN	116.78 m²	119.80 m²	110.33 m²	4
4	T3-4BRC-1	1	4PN	159.55 m²	160.90 m²	149.28 m²	5
5	T3-DUP-1	1	DUP	119.36 m²	108.08 m²	97.90 m²	5
6	T3-DUP-2	1	DUP	125.67 m²	114.42 m²	105.28 m²	5
TỔNG		6		732.89 m²	716.96 m²	659.54 m²	26

MẶT BẰNG TẦNG 3,5,7,9

TL: 1 : 100

DIỆN TÍCH SÀN XÂY DỰNG (CFA) :930.48 M2

PHIÊN BẢN	NỘI DUNG ĐIỀU CHỈNH	NGÀY NỘP

GHI CHÚ:

- CỐT +0.000 LẤY TẠI SÀN HOÀN THIỆN TẦNG 1 CÔNG TRÌNH TƯƠNG ĐƯƠNG COTE TUYỆT ĐỐI +7.900 (HỆ TỌA ĐỘ VN-2000)

- TÒA 1 CHIỀU CAO CÔNG TRÌNH TÍNH TỪ:
  + COTE HOÀN THIỆN +0.000: 43M
  + COTE NỀN TỰ NHIÊN THẤP NHẤT -1.000: 44M
- TÒA 2 CHIỀU CAO CÔNG TRÌNH TÍNH TỪ:
  + COTE HOÀN THIỆN +0.000: 50M
  + COTE NỀN TỰ NHIÊN THẤP NHẤT -1.000: 51M
- TÒA 3 CHIỀU CAO CÔNG TRÌNH TÍNH TỪ:
  + COTE HOÀN THIỆN +0.000: 59M
  + COTE NỀN TỰ NHIÊN THẤP NHẤT -1.000: 60M

- KHU VỰC TMDV BÀN GIAO THÔ, VỆ SINH KHÔNG XÂY, CHỈ BỐ TRÍ LAYOUT ĐỊNH HƯỚNG ĐẶT CÁC ĐẦU CHỜ.

- TỶ LỆ SỬ DỤNG VẬT LIỆU XANH KHÔNG NUNG ĐÁP ỨNG TỚI 90% KHỐI LƯỢNG GẠCH TRONG CÔNG TRÌNH

- TRONG PHÒNG RÁC KHÔNG BỐ TRÍ CÁC CHẤT, VẬT LIỆU CÓ KHẢ NĂNG GÂY CHÁY NỔ

- TƯỜNG NGĂN CHÁY, VÁCH NGĂN CHÁY TRONG CÁC GIAN PHÒNG ĐƯỢC NGĂN CHIA ĐẾN TRẦN BÊ TÔNG.

- VẬT LIỆU HOÀN THIỆN TRẦN, TƯỜNG, SÀN TRÊN CÁC ĐƯỜNG THOÁT NẠN, TRONG SẢNH THANG MÁY, SẢNH CHUNG, TẦNG KỸ THUẬT LÀ VẬT LIỆU KHÔNG CHÁY ĐẠT CV0

- TRONG CÁC KHÔNG GIAN TRẦN TREO KHÔNG BỐ TRÍ CÁC KÊNH, ĐƯỜNG ỐNG DẪN VẬN CHUYỂN CÁC CHẤT CHÁY DẠNG KHÍ, HỖN HỢP KHÍ, CHẤT LỎNG VÀ VẬT LIỆU CHÁY.

- TRONG CÔNG TRÌNH KHÔNG BỐ TRÍ TRẦN TREO CHO CÁC GIAN PHÒNG HẠNG A VÀ HẠNG B

- KHÔNG CÓ KÊNH, GIẾNG, ĐƯỜNG ỐNG ĐI QUA TƯỜNG NGĂN CHÁY LOẠI 1

ỐP FACADE : LÀM VIỆC VỚI TƯ VẤN FACADE

CHỦ ĐẦU TƯ / OWNER:
CÔNG TY CỔ PHẦN THƯƠNG MẠI DƯƠNG PHÚC THẮNG
DUONG PHUC THANG TRADING JOINT STOCK COMPANY
ĐỊA CHỈ / ADDRESS:
Tầng 16, Tòa OSI Tower, Khu tây Hồ Tây, Phường Xuân Đỉnh, Thành phố Hà Nội, Việt Nam.
Hotline : 0243 2077 272

TƯ VẤN KIẾN TRÚC CHÍNH / MAIN ARCHITECTURAL CONSULTANT:
CÔNG TY TNHH KIẾN TRÚC DP VIỆT NAM
DP ARCHITECTS VIETNAM CO.,LTD.
ĐỊA CHỈ / ADDRESS:
Tầng 4, số 82 Võ Văn Tần, Phường Xuân Hòa, TP.Hồ Chí Minh
Hotline : 0283 5357 507
Fax: 0283 5357 517
Email : dparchitects@dpa.com.sg

TƯ VẤN THIẾT KẾ / CONSULTANT:
CÔNG TY CỔ PHẦN INNO
INNO.,JSC
ĐỊA CHỈ / ADDRESS
HN: 39 Thượng Thụy, Phú Thượng, Hà Nội
HCM: 37 Nguyễn Văn Hưởng, An Khánh, TP. HCM
Hotline: 0243 212 1776 Email : ad@innojsc.com

TỔNG GIÁM ĐỐC / GENERAL DIRECTOR:
ĐOÀN VĂN ĐỘNG
CHỦ NHIỆM THIẾT KẾ / PROJECT MANAGER:
LƯU GIANG NAM
CHỦ TRÌ THIẾT KẾ / DESIGN MANAGER:
NGÔ NGỌC BÌNH
KIỂM / CHECKED BY:
VŨ TUẤN ANH
THIẾT KẾ / DESIGNER
LÊ THỊ THANH **NGUYỄN XUÂN HIỆN**
PHƯƠNG THỊ ÁNH TUYẾT **VŨ TIẾN DƯƠNG**

TÊN DỰ ÁN / PROJECT NAME:
XÂY DỰNG NHÀ Ở TẠI LÔ ĐẤT NO-02

ĐỊA ĐIỂM XÂY DỰNG / PROJECT ADDRESS:
LÔ ĐẤT NO-22, PHƯỜNG BỒ ĐỀ, HÀ NỘI

HẠNG MỤC / ITEM:
KIẾN TRÚC

HOÀN THÀNH / FINISHED DATE:	MÃ SỐ DỰ ÁN / PROJECT No:
TKCS	2501
HOÀN THÀNH / FINISHED DATE: 2026	PHIÊN BẢN / REVISION: 1

TÊN BẢN VẼ / SHEET NAME:
MẶT BẰNG TẦNG 3-5-7-9

SỐ HIỆU BẢN VẼ / SHEET NUMBER:
A.3-01.103

© 2025 - INNO.,jsc

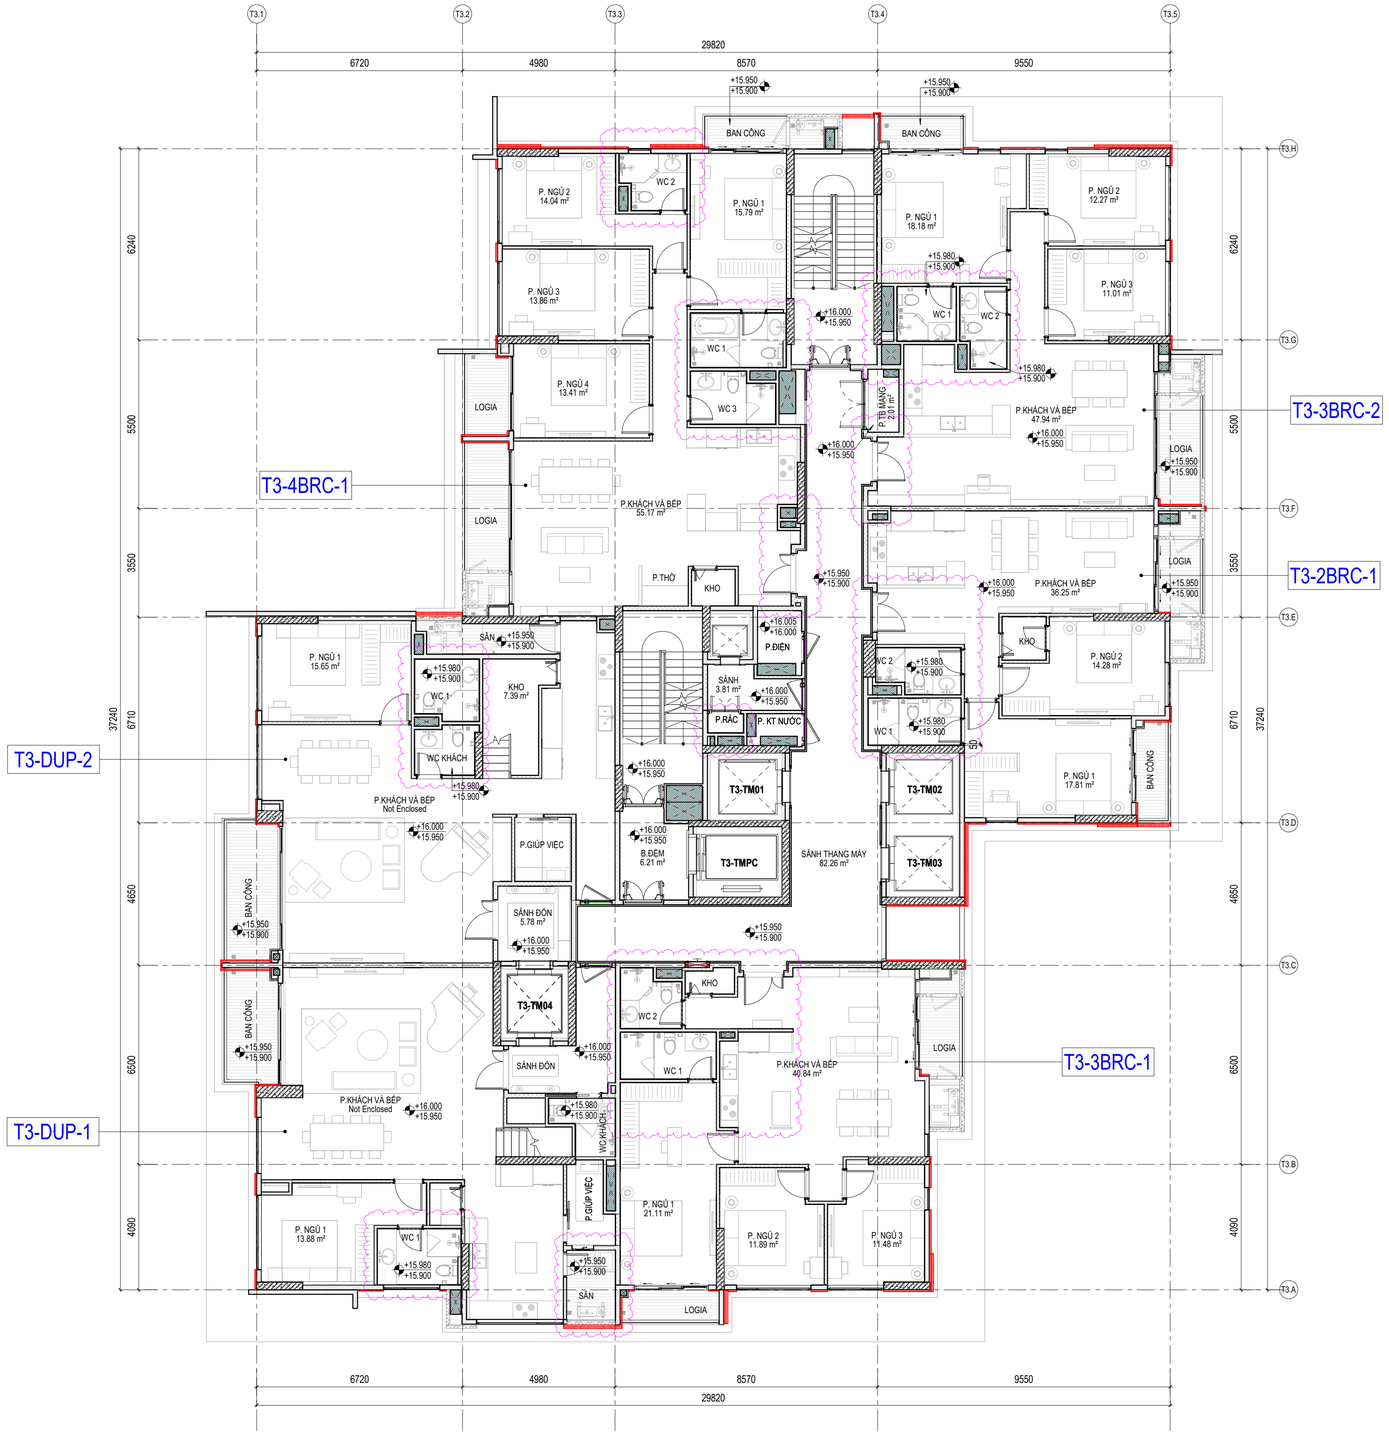

THỐNG KÊ DIỆN TÍCH CĂN HỘ TĐH01							
STT	Tên căn hộ	Số lượng	Loại căn hộ(Phòng ngủ)	IFA(m²)	GFA(m²)	NSA(m²)	Số người
1	T3-2BRC-1	1	2PN	97.16 m²	97.87 m²	89.50 m²	3
2	T3-3BRC-1	1	3PN	114.38 m²	116.09 m²	107.30 m²	4
3	T3-3BRC-2	1	3PN	116.78 m²	119.80 m²	110.33 m²	4
4	T3-4BRC-1	1	4PN	159.53 m²	160.90 m²	149.28 m²	5
5	T3-DUP-1	1	DUP	127.21 m²	128.92 m²	117.73 m²	5
6	T3-DUP-2	1	DUP	135.30 m²	136.37 m²	126.84 m²	5
TỔNG		6		750.35 m²	759.96 m²	700.97 m²	26

MẶT BẰNG TẦNG 4,6,8

TL: 1 : 100

DIỆN TÍCH SÀN XÂY DỰNG (CFA) :930.48 M2

PHIÊN BẢN	NỘI DUNG ĐIỀU CHỈNH	NGÀY NỘP

GHI CHÚ:

- CỐT +0.000 LẤY TẠI SÀN HOÀN THIỆN TẦNG 1 CÔNG TRÌNH TƯƠNG ĐƯƠNG COTE TUYỆT ĐỐI +7.900 (HỆ TỌA ĐỘ VN-2000)

- TÒA 1 CHIỀU CAO CÔNG TRÌNH TÍNH TỪ:
  + COTE HOÀN THIỆN +0.000: 43M
  + COTE NỀN TỰ NHIÊN THẤP NHẤT -1.000: 44M
- TÒA 2 CHIỀU CAO CÔNG TRÌNH TÍNH TỪ:
  + COTE HOÀN THIỆN +0.000: 50M
  + COTE NỀN TỰ NHIÊN THẤP NHẤT -1.000: 51M
- TÒA 3 CHIỀU CAO CÔNG TRÌNH TÍNH TỪ:
  + COTE HOÀN THIỆN +0.000: 59M
  + COTE NỀN TỰ NHIÊN THẤP NHẤT -1.000: 60M

- KHU VỰC TMDV BÀN GIAO THÔ, VỆ SINH KHÔNG XÂY, CHỈ BỐ TRÍ LAYOUT ĐỊNH HƯỚNG ĐẶT CÁC ĐẦU CHỜ.

- TỶ LỆ SỬ DỤNG VẬT LIỆU XANH KHÔNG NUNG ĐÁP ỨNG TỐI 90% KHỐI LƯỢNG GẠCH TRONG CÔNG TRÌNH

- TRONG PHÒNG RÁC KHÔNG BỐ TRÍ CÁC CHẤT, VẬT LIỆU CÓ KHẢ NĂNG GÂY CHÁY NỔ

- TƯỜNG NGĂN CHÁY, VÁCH NGĂN CHÁY TRONG CÁC GIAN PHÒNG ĐƯỢC NGĂN CHIA ĐẾN TRẦN BÊ TÔNG.

- VẬT LIỆU HOÀN THIỆN TRẦN, TƯỜNG, SÀN TRÊN CÁC ĐƯỜNG THOÁT NẠN, TRONG SẢNH THANG MÁY, SẢNH CHUNG, TẦNG KỸ THUẬT LÀ VẬT LIỆU KHÔNG CHÁY ĐẠT CV0

- TRONG CÁC KHÔNG GIAN TRẦN TREO KHÔNG BỐ TRÍ CÁC KÊNH, ĐƯỜNG ỐNG DẪN VẬN CHUYỂN CÁC CHẤT CHÁY DẠNG KHÍ, HỖN HỢP KHÍ, CHẤT LỎNG VÀ VẬT LIỆU CHÁY.

- TRONG CÔNG TRÌNH KHÔNG BỐ TRÍ TRẦN TREO CHO CÁC GIAN PHÒNG HẠNG A VÀ HẠNG B

- KHÔNG CÓ KÊNH, GIẾNG, ĐƯỜNG ỐNG ĐI QUA TƯỜNG NGĂN CHÁY LOẠI 1

ỐP FACADE : LÀM VIỆC VỚI TƯ VẤN FACADE

CHỦ ĐẦU TƯ / OWNER:
CÔNG TY CỔ PHẦN THƯƠNG MẠI DƯƠNG PHÚC THẮNG
DUONG PHUC THANG TRADING JOINT STOCK COMPANY
ĐỊA CHỈ / ADDRESS:
Tầng 16, Tòa OSI Tower, Khu tây Hồ Tây, Phường Xuân Đỉnh, Thành phố Hà Nội, Việt Nam.
Hotline : 0243 2077 272

TƯ VẤN KIẾN TRÚC CHÍNH / MAIN ARCHITECTURAL CONSULTANT:
CÔNG TY TNHH KIẾN TRÚC DP VIỆT NAM
DP ARCHITECTS VIETNAM CO.,LTD.
ĐỊA CHỈ / ADDRESS:
Tầng 4, số 82 Võ Văn Tần, Phường Xuân Hòa, TP.Hồ Chí Minh
Hotline : 0283 5357 507
Fax: 0283 5357 517
Email : dparchitects@dpa.com.sg

TƯ VẤN THIẾT KẾ / CONSULTANT:
CÔNG TY CỔ PHẦN INNO
INNO.,JSC
ĐỊA CHỈ / ADDRESS
HN: 39 Thượng Thụy, Phú Thượng, Hà Nội
HCM: 37 Nguyễn Văn Hưởng, An Khánh, TP. HCM
Hotline: 0243 212 1776 Email : ad@innojsc.com

TỔNG GIÁM ĐỐC / GENERAL DIRECTOR:
ĐOÀN VĂN ĐỘNG
CHỦ NHIỆM THIẾT KẾ / PROJECT MANAGER:
LƯU GIANG NAM
CHỦ TRÌ THIẾT KẾ / DESIGN MANAGER:
NGÔ NGỌC BÌNH
KIỂM / CHECKED BY:
VŨ TUẤN ANH
THIẾT KẾ / DESIGNER
LÊ THỊ THANH **NGUYỄN XUÂN HIỆN**
PHƯƠNG THỊ ÁNH TUYẾT **VŨ TIẾN DƯƠNG**

TÊN DỰ ÁN / PROJECT NAME:
XÂY DỰNG NHÀ Ở TẠI LÔ ĐẤT NO-02

ĐỊA ĐIỂM XÂY DỰNG / PROJECT ADDRESS:
LÔ ĐẤT NO-22, PHƯỜNG BỒ ĐỀ, HÀ NỘI

HẠNG MỤC / ITEM:
KIẾN TRÚC

HOÀN THÀNH / FINISHED DATE:	MÃ SỐ DỰ ÁN / PROJECT No:
TKCS	2501
HOÀN THÀNH / FINISHED DATE: 2026	PHIÊN BẢN / REVISION: 1

TÊN BẢN VẼ / SHEET NAME:
MẶT BẰNG TẦNG 4-6-8-10

SỐ HIỆU BẢN VẼ / SHEET NUMBER:
A.3-01.104

© 2025 - INNO_jsc

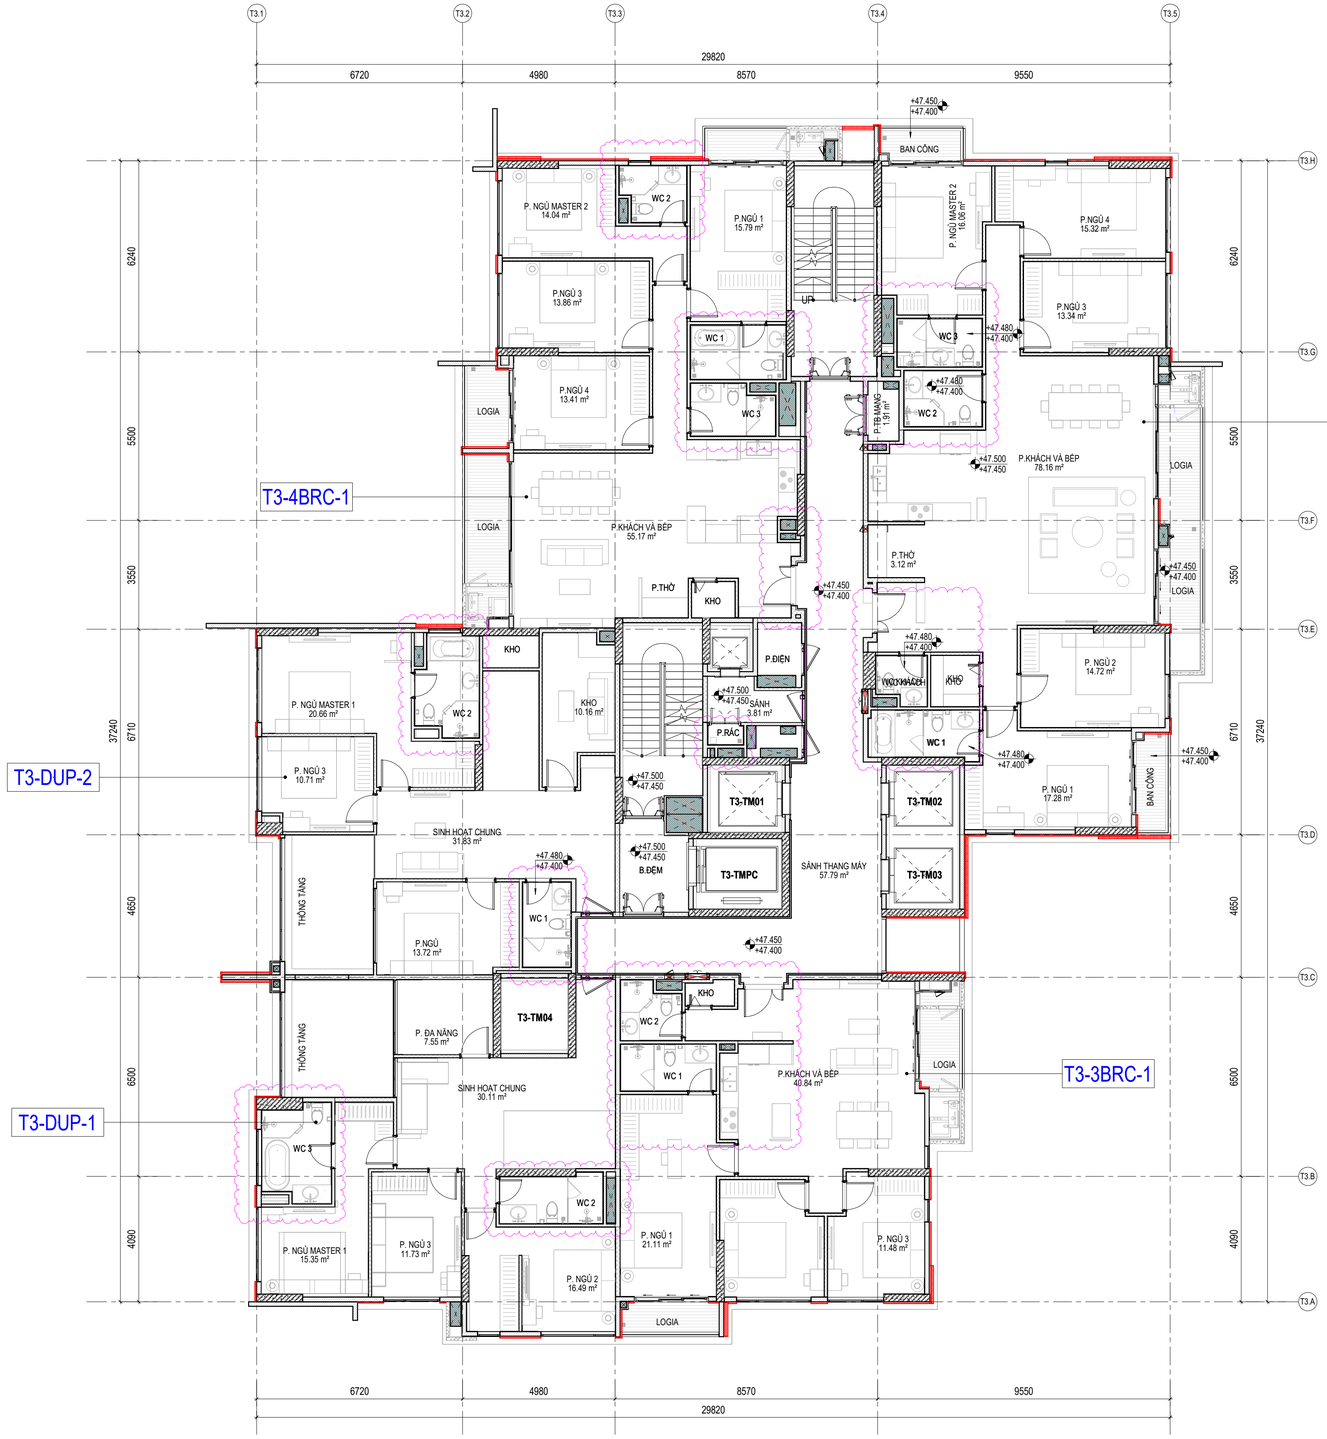

THỐNG KÊ DIỆN TÍCH CĂN HỘ TDH03							
STT	Tên căn hộ	Số lượng(căn)	Loại căn hộ(Phòng ngủ)	IFA(m²)	GFA(m²)	NSA(m²)	Số người
1	T3-3BRC-1	1	3PN	114.31 m²	115.84 m²	107.17 m²	4
2	T3-4BRC-1	1	4PN	159.51 m²	160.85 m²	149.18 m²	5
3	T3-DUP-1	1	DUP	119.34 m²	108.08 m²	97.94 m²	5
4	T3-DUP-2	1	DUP	125.67 m²	114.40 m²	105.34 m²	5
5	T3-PH	1	5PN	214.50 m²	218.08 m²	201.93 m²	5
TỔNG		5		733.32 m²	717.25 m²	661.56 m²	24

MẶT BẰNG TẦNG 11

TL: 1 : 100

DIỆN TÍCH SÀN XÂY DỰNG (CFA) :930.48 M2

PHIÊN BẢN	NỘI DUNG ĐIỀU CHỈNH	NGÀY NỘP

GHI CHÚ:

- CỐT +0.000 LẤY TẠI SÀN HOÀN THIỆN TẦNG 1 CÔNG TRÌNH TƯƠNG ĐƯƠNG COTE TUYỆT ĐỐI +7.900 (HỆ TỌA ĐỘ VN-2000)

- TÒA 1 CHIỀU CAO CÔNG TRÌNH TÍNH TỪ:
  + COTE HOÀN THIỆN +0.000: 43M
  + COTE NỀN TỰ NHIÊN THẤP NHẤT -1.000: 44M
- TÒA 2 CHIỀU CAO CÔNG TRÌNH TÍNH TỪ:
  + COTE HOÀN THIỆN +0.000: 50M
  + COTE NỀN TỰ NHIÊN THẤP NHẤT -1.000: 51M
- TÒA 3 CHIỀU CAO CÔNG TRÌNH TÍNH TỪ:
  + COTE HOÀN THIỆN +0.000: 59M
  + COTE NỀN TỰ NHIÊN THẤP NHẤT -1.000: 60M

- KHU VỰC TMDV BÀN GIAO THÔ, VỆ SINH KHÔNG XÂY, CHỈ BỐ TRÍ LAYOUT ĐỊNH HƯỚNG ĐẶT CÁC ĐẦU CHỜ.

- TỶ LỆ SỬ DỤNG VẬT LIỆU XANH KHÔNG NUNG ĐÁP ỨNG TỐI 90% KHỐI LƯỢNG GẠCH TRONG CÔNG TRÌNH

- TRONG PHÒNG RÁC KHÔNG BỐ TRÍ CÁC CHẤT, VẬT LIỆU CÓ KHẢ NĂNG GÂY CHÁY NỔ

- TƯỜNG NGĂN CHÁY, VÁCH NGĂN CHÁY TRONG CÁC GIAN PHÒNG ĐƯỢC NGĂN CHIA ĐẾN TRẦN BÊ TÔNG.

- VẬT LIỆU HOÀN THIỆN TRẦN, TƯỜNG, SÀN TRÊN CÁC ĐƯỜNG THOÁT NẠN, TRONG SẢNH THANG MÁY, SẢNH CHUNG, TẦNG KỸ THUẬT LÀ VẬT LIỆU KHÔNG CHÁY ĐẠT CV0

- TRONG CÁC KHÔNG GIAN TRẦN TREO KHÔNG BỐ TRÍ CÁC KÊNH, ĐƯỜNG ỐNG DẪN VẬN CHUYỂN CÁC CHẤT CHÁY DẠNG KHÍ, HỖN HỢP KHÍ, CHẤT LỎNG VÀ VẬT LIỆU CHÁY.

- TRONG CÔNG TRÌNH KHÔNG BỐ TRÍ TRẦN TREO CHO CÁC GIAN PHÒNG HẠNG A VÀ HẠNG B

- KHÔNG CÓ KÊNH, GIẾNG, ĐƯỜNG ỐNG ĐI QUA TƯỜNG NGĂN CHÁY LOẠI 1

ỐP FACADE : LÀM VIỆC VỚI TƯ VẤN FACADE

CHỦ ĐẦU TƯ / OWNER:
CÔNG TY CỔ PHẦN THƯƠNG MẠI DƯƠNG PHÚC THẮNG
DUONG PHUC THANG TRADING JOINT STOCK COMPANY

ĐỊA CHỈ / ADDRESS:
Tầng 16, Tòa OSI Tower, Khu tây Hồ Tây, Phường Xuân Đỉnh, Thành phố Hà Nội, Việt Nam.
Hotline : 0243 2077 272

TƯ VẤN KIẾN TRÚC CHÍNH / MAIN ARCHITECTURAL CONSULTANT:
CÔNG TY TNHH KIẾN TRÚC DP VIỆT NAM
DP ARCHITECTS VIETNAM CO.,LTD.

ĐỊA CHỈ / ADDRESS:
Tầng 4, số 82 Võ Văn Tần, Phường Xuân Hòa, TP.Hồ Chí Minh
Hotline : 0283 5357 507
Fax: 0283 5357 517
Email : dparchitects@dpa.com.sg

TƯ VẤN THIẾT KẾ / CONSULTANT:
CÔNG TY CỔ PHẦN INNO
INNO.,JSC

ĐỊA CHỈ / ADDRESS
HN: 39 Thượng Thụy, Phú Thượng, Hà Nội
HCM: 37 Nguyễn Văn Hưởng, An Khánh, TP. HCM
Hotline: 0243 212 1776 Email : ad@innojsc.com

TỔNG GIÁM ĐỐC / GENERAL DIRECTOR:
ĐOÀN VĂN ĐỘNG

CHỦ NHIỆM THIẾT KẾ / PROJECT MANAGER:
LƯU GIANG NAM

CHỦ TRÌ THIẾT KẾ / DESIGN MANAGER:
NGÔ NGỌC BÌNH

KIỂM / CHECKED BY:
VŨ TUẤN ANH

THIẾT KẾ / DESIGNER:
LÊ THỊ THANH **NGUYỄN XUÂN HIỆN**
PHƯƠNG THỊ ÁNH TUYẾT **VŨ TIẾN DƯƠNG**

TÊN DỰ ÁN / PROJECT NAME:
XÂY DỰNG NHÀ Ở TẠI LÔ ĐẤT NO-02

ĐỊA ĐIỂM XÂY DỰNG / PROJECT ADDRESS:
LÔ ĐẤT NO-22, PHƯỜNG BỒ ĐỀ, HÀ NỘI

HẠNG MỤC / ITEM:
KIẾN TRÚC

HOÀN THÀNH / FINISHED DATE:	MÃ SỐ DỰ ÁN / PROJECT No:
TKCS	2501
HOÀN THÀNH / FINISHED DATE: 2026	PHIÊN BẢN / REVISION: 1

TÊN BẢN VẼ / SHEET NAME:
MẶT BẰNG TẦNG 11

SỐ HIỆU BẢN VẼ / SHEET NUMBER:
A.3-01.105

© 2025 - INNO.,jsc

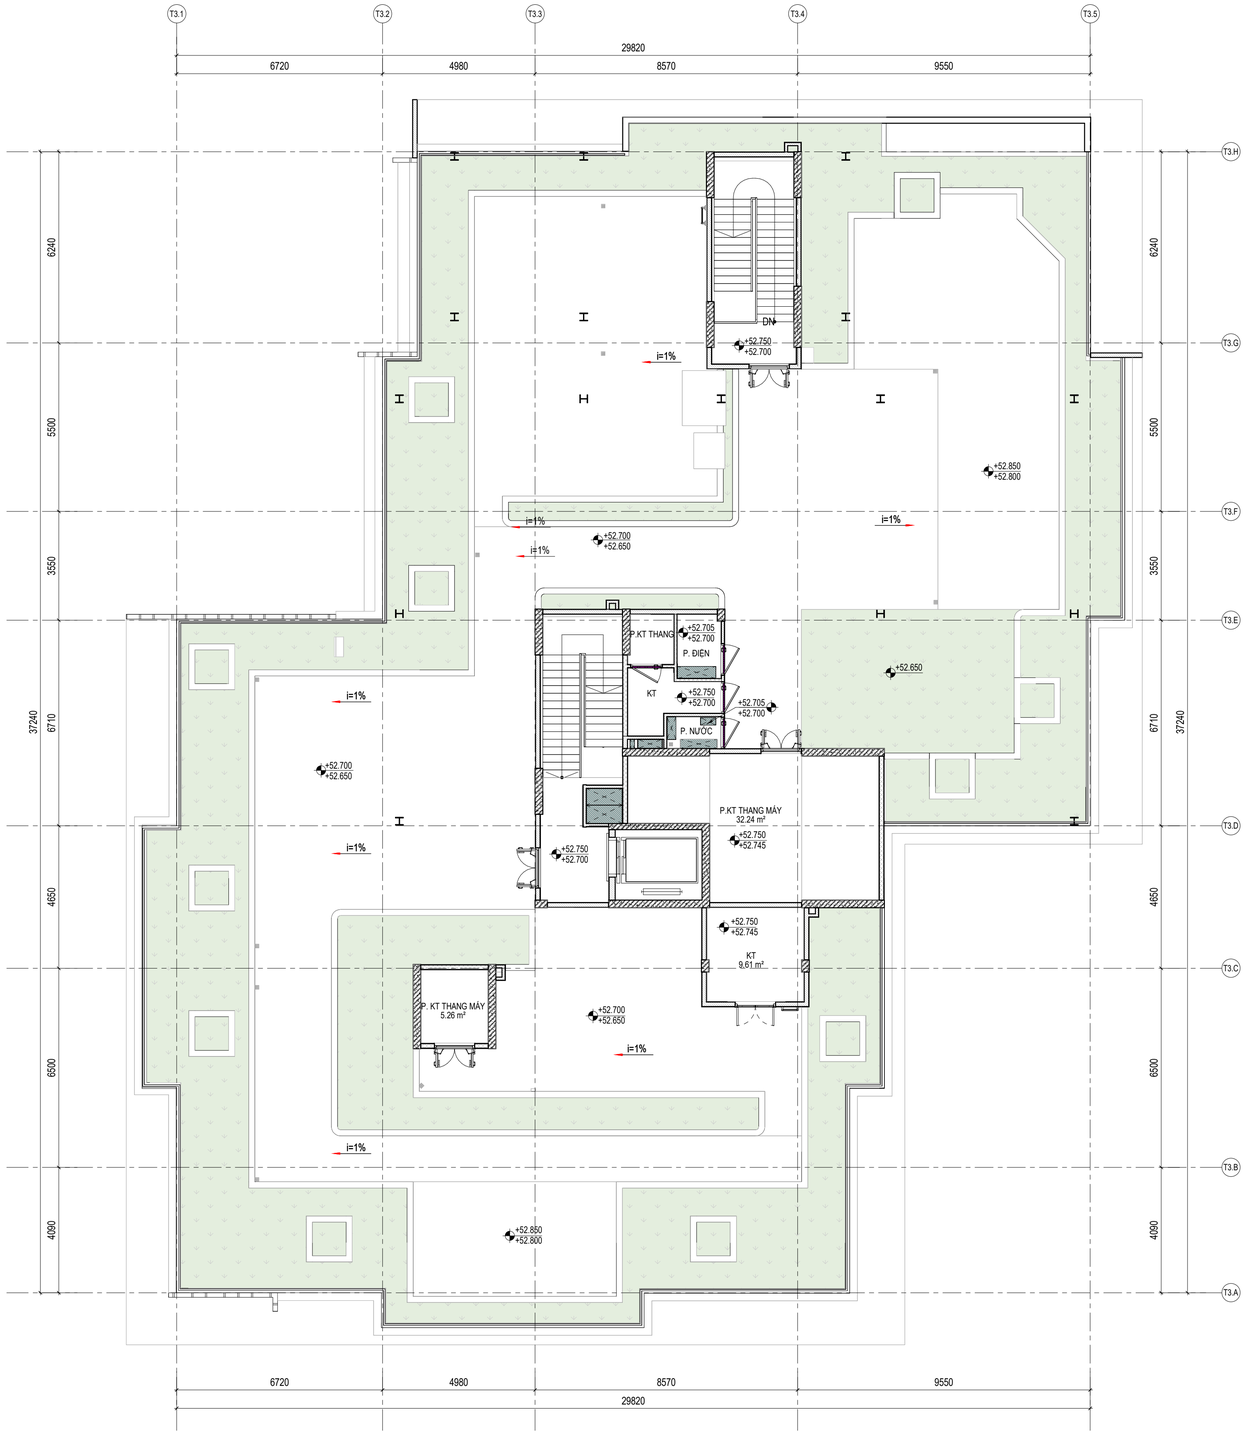

MẶT BẰNG TẦNG TUM

TL: 1 : 100

PHIÊN BẢN	NỘI DUNG ĐIỀU CHỈNH	NGÀY NỘP

GHI CHÚ:

- CỐT +0.000 LẤY TẠI SÀN HOÀN THIỆN TẦNG 1 CÔNG TRÌNH TƯƠNG ĐƯƠNG COTE TUYỆT ĐỐI +7.900 (HỆ TỌA ĐỘ VN-2000)

- TÒA 1 CHIỀU CAO CÔNG TRÌNH TÍNH TỪ:
  + COTE HOÀN THIỆN +0.000: 43M
  + COTE NỀN TỰ NHIÊN THẤP NHẤT -1.000: 44M
- TÒA 2 CHIỀU CAO CÔNG TRÌNH TÍNH TỪ:
  + COTE HOÀN THIỆN +0.000: 50M
  + COTE NỀN TỰ NHIÊN THẤP NHẤT -1.000: 51M
- TÒA 3 CHIỀU CAO CÔNG TRÌNH TÍNH TỪ:
  + COTE HOÀN THIỆN +0.000: 59M
  + COTE NỀN TỰ NHIÊN THẤP NHẤT -1.000: 60M

- KHU VỰC TMDV BÀN GIAO THÔ, VỆ SINH KHÔNG XÂY, CHỈ BỐ TRÍ LAYOUT ĐỊNH HƯỚNG ĐẶT CÁC ĐẦU CHỜ.

- TỶ LỆ SỬ DỤNG VẬT LIỆU XANH KHÔNG NUNG ĐÁP ỨNG TỚI 90% KHỐI LƯỢNG GẠCH TRONG CÔNG TRÌNH

- TRONG PHÒNG RÁC KHÔNG BỐ TRÍ CÁC CHẤT, VẬT LIỆU CÓ KHẢ NĂNG GÂY CHÁY NỔ

- TƯỜNG NGĂN CHÁY, VÁCH NGĂN CHÁY TRONG CÁC GIAN PHÒNG ĐƯỢC NGĂN CHIA ĐẾN TRẦN BÊ TÔNG.

- VẬT LIỆU HOÀN THIỆN TRẦN, TƯỜNG, SÀN TRÊN CÁC ĐƯỜNG THOÁT NẠN, TRONG SẢNH THANG MÁY, SẢNH CHUNG, TẦNG KỸ THUẬT LÀ VẬT LIỆU KHÔNG CHÁY ĐẠT CV0

- TRONG CÁC KHÔNG GIAN TRẦN TREO KHÔNG BỐ TRÍ CÁC KÊNH, ĐƯỜNG ỐNG DẪN VẬN CHUYỂN CÁC CHẤT CHÁY DẠNG KHÍ, HỖN HỢP KHÍ, CHẤT LỎNG VÀ VẬT LIỆU CHÁY.

- TRONG CÔNG TRÌNH KHÔNG BỐ TRÍ TRẦN TREO CHO CÁC GIAN PHÒNG HẠNG A VÀ HẠNG B

- KHÔNG CÓ KÊNH, GIẾNG, ĐƯỜNG ỐNG ĐI QUA TƯỜNG NGĂN CHÁY LOẠI 1

CHỦ ĐẦU TƯ / OWNER:
CÔNG TY CỔ PHẦN THƯƠNG MẠI DƯƠNG PHÚC THẮNG
DUONG PHUC THANG TRADING JOINT STOCK COMPANY

ĐỊA CHỈ / ADDRESS:
Tầng 16, Tòa OSI Tower, Khu tây Hồ Tây, Phường Xuân Đỉnh, Thành phố Hà Nội, Việt Nam.
Hotline : 0243 2077 272

TƯ VẤN KIẾN TRÚC CHÍNH / MAIN ARCHITECTURAL CONSULTANT:
CÔNG TY TNHH KIẾN TRÚC DP VIỆT NAM
DP ARCHITECTS VIETNAM CO.,LTD.

ĐỊA CHỈ / ADDRESS:
Tầng 4, số 82 Võ Văn Tần, Phường Xuân Hòa, TP.Hồ Chí Minh
Hotline : 0283 5357 507
Fax: 0283 5357 517
Email : dparchitects@dpa.com.sg

TƯ VẤN THIẾT KẾ / CONSULTANT:
CÔNG TY CỔ PHẦN INNO
INNO.,JSC

ĐỊA CHỈ / ADDRESS
HN: 39 Thượng Thụy, Phú Thượng, Hà Nội
HCM: 37 Nguyễn Văn Hưởng, An Khánh, TP. HCM
Hotline: 0243 212 1776 Email : ad@innojsc.com

TỔNG GIÁM ĐỐC / GENERAL DIRECTOR:
ĐOÀN VĂN ĐỘNG

CHỦ NHIỆM THIẾT KẾ / PROJECT MANAGER:
LƯU GIANG NAM

CHỦ TRÌ THIẾT KẾ / DESIGN MANAGER:
NGÔ NGỌC BÌNH

KIỂM / CHECKED BY:
VŨ TUẤN ANH

THIẾT KẾ / DESIGNER
LÊ THỊ THANH **NGUYỄN XUÂN HIỆN**
PHƯƠNG THỊ ÁNH TUYẾT **VŨ TIẾN DƯƠNG**

TÊN DỰ ÁN / PROJECT NAME:
XÂY DỰNG NHÀ Ở TẠI LÔ ĐẤT NO-02

ĐỊA ĐIỂM XÂY DỰNG / PROJECT ADDRESS:
LÔ ĐẤT NO-22, PHƯỜNG BỒ ĐỀ, HÀ NỘI

HẠNG MỤC / ITEM:
KIẾN TRÚC

HOÀN THÀNH / FINISHED DATE:	MÃ SỐ DỰ ÁN / PROJECT No:
TKCS	2501
HOÀN THÀNH / FINISHED DATE: 2026	PHIÊN BẢN / REVISION: 1

TÊN BẢN VẼ / SHEET NAME:
MẶT BẰNG TẦNG TUM

SỐ HIỆU BẢN VẼ / SHEET NUMBER:
A.3-01.106

© 2025 - INNO.,jsc

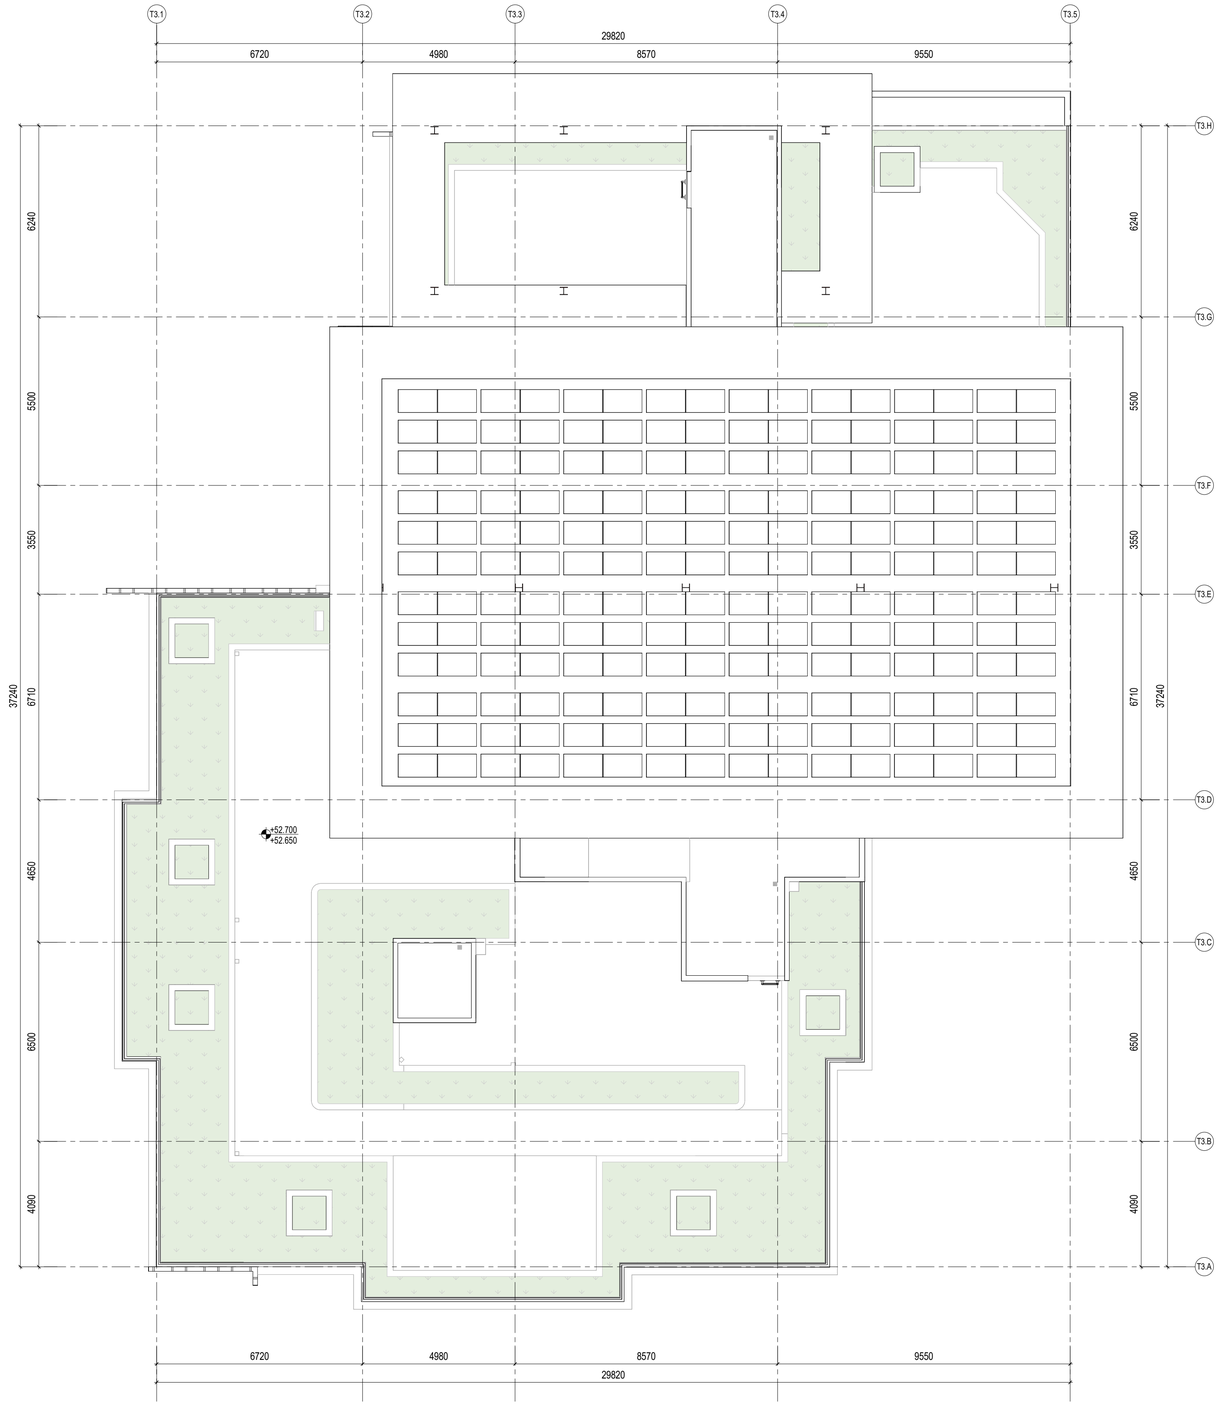

MẶT BẰNG TẦNG MÁI
TL: 1 : 100

PHIÊN BẢN	NỘI DUNG ĐIỀU CHỈNH	NGÀY NỘP

GHI CHÚ:

- CỐT +0.000 LẤY TẠI SÀN HOÀN THIỆN TẦNG 1 CÔNG TRÌNH TƯƠNG ĐƯƠNG COTE TUYỆT ĐỐI +7.900 (HỆ TỌA ĐỘ VN-2000)

- TÒA 1 CHIỀU CAO CÔNG TRÌNH TÍNH TỪ:
  + COTE HOÀN THIỆN +0.000: 43M
  + COTE NỀN TỰ NHIÊN THẤP NHẤT -1.000: 44M
- TÒA 2 CHIỀU CAO CÔNG TRÌNH TÍNH TỪ:
  + COTE HOÀN THIỆN +0.000: 50M
  + COTE NỀN TỰ NHIÊN THẤP NHẤT -1.000: 51M
- TÒA 3 CHIỀU CAO CÔNG TRÌNH TÍNH TỪ:
  + COTE HOÀN THIỆN +0.000: 59M
  + COTE NỀN TỰ NHIÊN THẤP NHẤT -1.000: 60M

- KHU VỰC TMDV BÀN GIAO THÔ, VỆ SINH KHÔNG XÂY, CHỈ BỐ TRÍ LAYOUT ĐỊNH HƯỚNG ĐẶT CÁC ĐẦU CHỜ.

- TỶ LỆ SỬ DỤNG VẬT LIỆU XANH KHÔNG NUNG ĐÁP ỨNG TỐI 90% KHỐI LƯỢNG GẠCH TRONG CÔNG TRÌNH

- TRONG PHÒNG RÁC KHÔNG BỐ TRÍ CÁC CHẤT, VẬT LIỆU CÓ KHẢ NĂNG GÂY CHÁY NỔ

- TƯỜNG NGĂN CHÁY, VÁCH NGĂN CHÁY TRONG CÁC GIAN PHÒNG ĐƯỢC NGĂN CHIA ĐẾN TRẦN BÊ TÔNG.

- VẬT LIỆU HOÀN THIỆN TRẦN, TƯỜNG, SÀN TRÊN CÁC ĐƯỜNG THOÁT NẠN, TRONG SẢNH THANG MÁY, SẢNH CHUNG, TẦNG KỸ THUẬT LÀ VẬT LIỆU KHÔNG CHÁY ĐẠT CV0

- TRONG CÁC KHÔNG GIAN TRẦN TREO KHÔNG BỐ TRÍ CÁC KÊNH, ĐƯỜNG ỐNG DẪN VẬN CHUYỂN CÁC CHẤT CHÁY DẠNG KHÍ, HỖN HỢP KHÍ, CHẤT LỎNG VÀ VẬT LIỆU CHÁY.

- TRONG CÔNG TRÌNH KHÔNG BỐ TRÍ TRẦN TREO CHO CÁC GIAN PHÒNG HẠNG A VÀ HẠNG B

- KHÔNG CÓ KÊNH, GIẾNG, ĐƯỜNG ỐNG ĐI QUA TƯỜNG NGĂN CHÁY LOẠI 1

CHỦ ĐẦU TƯ / OWNER:
CÔNG TY CỔ PHẦN THƯƠNG MẠI DƯƠNG PHÚC THẮNG
DUONG PHUC THANG TRADING JOINT STOCK COMPANY
ĐỊA CHỈ / ADDRESS:
Tầng 16, Tòa OSI Tower, Khu tây Hồ Tây, Phường Xuân Đỉnh, Thành phố Hà Nội, Việt Nam.
Hotline : 0243 2077 272

TƯ VẤN KIẾN TRÚC CHÍNH / MAIN ARCHITECTURAL CONSULTANT:
CÔNG TY TNHH KIẾN TRÚC DP VIỆT NAM
DP ARCHITECTS VIETNAM CO.,LTD.
ĐỊA CHỈ / ADDRESS:
Tầng 4, số 82 Võ Văn Tần, Phường Xuân Hòa, TP.Hồ Chí Minh
Hotline : 0283 5357 507
Fax: 0283 5357 517
Email : dparchitects@dpa.com.sg

TƯ VẤN THIẾT KẾ / CONSULTANT:
CÔNG TY CỔ PHẦN INNO
INNO.,JSC
ĐỊA CHỈ / ADDRESS
HN: 39 Thượng Thụy, Phú Thượng, Hà Nội
HCM: 37 Nguyễn Văn Hưởng, An Khánh, TP. HCM
Hotline: 0243 212 1776 Email : ad@innojsc.com

TỔNG GIÁM ĐỐC / GENERAL DIRECTOR:
ĐOÀN VĂN ĐỘNG

CHỦ NHIỆM THIẾT KẾ / PROJECT MANAGER:
LƯU GIANG NAM

CHỦ TRÌ THIẾT KẾ / DESIGN MANAGER:
NGÔ NGỌC BÌNH

KIỂM / CHECKED BY:
VŨ TUẤN ANH

THIẾT KẾ / DESIGNER:
LÊ THỊ THANH
NGUYỄN XUÂN HIỆN
PHƯƠNG THỊ ÁNH TUYẾT
VŨ TIẾN DƯƠNG

TÊN DỰ ÁN / PROJECT NAME:
XÂY DỰNG NHÀ Ở TẠI LÔ ĐẤT NO-02

ĐỊA ĐIỂM XÂY DỰNG / PROJECT ADDRESS:
LÔ ĐẤT NO-22, PHƯỜNG BỒ ĐỀ, HÀ NỘI

HẠNG MỤC / ITEM:
KIẾN TRÚC

HOÀN THÀNH / FINISHED DATE:	MÃ SỐ DỰ ÁN / PROJECT No:
TKCS	2501
HOÀN THÀNH / FINISHED DATE: 2026	PHIÊN BẢN / REVISION: 2

TÊN BẢN VẼ / SHEET NAME:
MẶT BẰNG MÁI

SỐ HIỆU BẢN VẼ / SHEET NUMBER:
A.3-01.107

© 2025 - INNO.,jsc

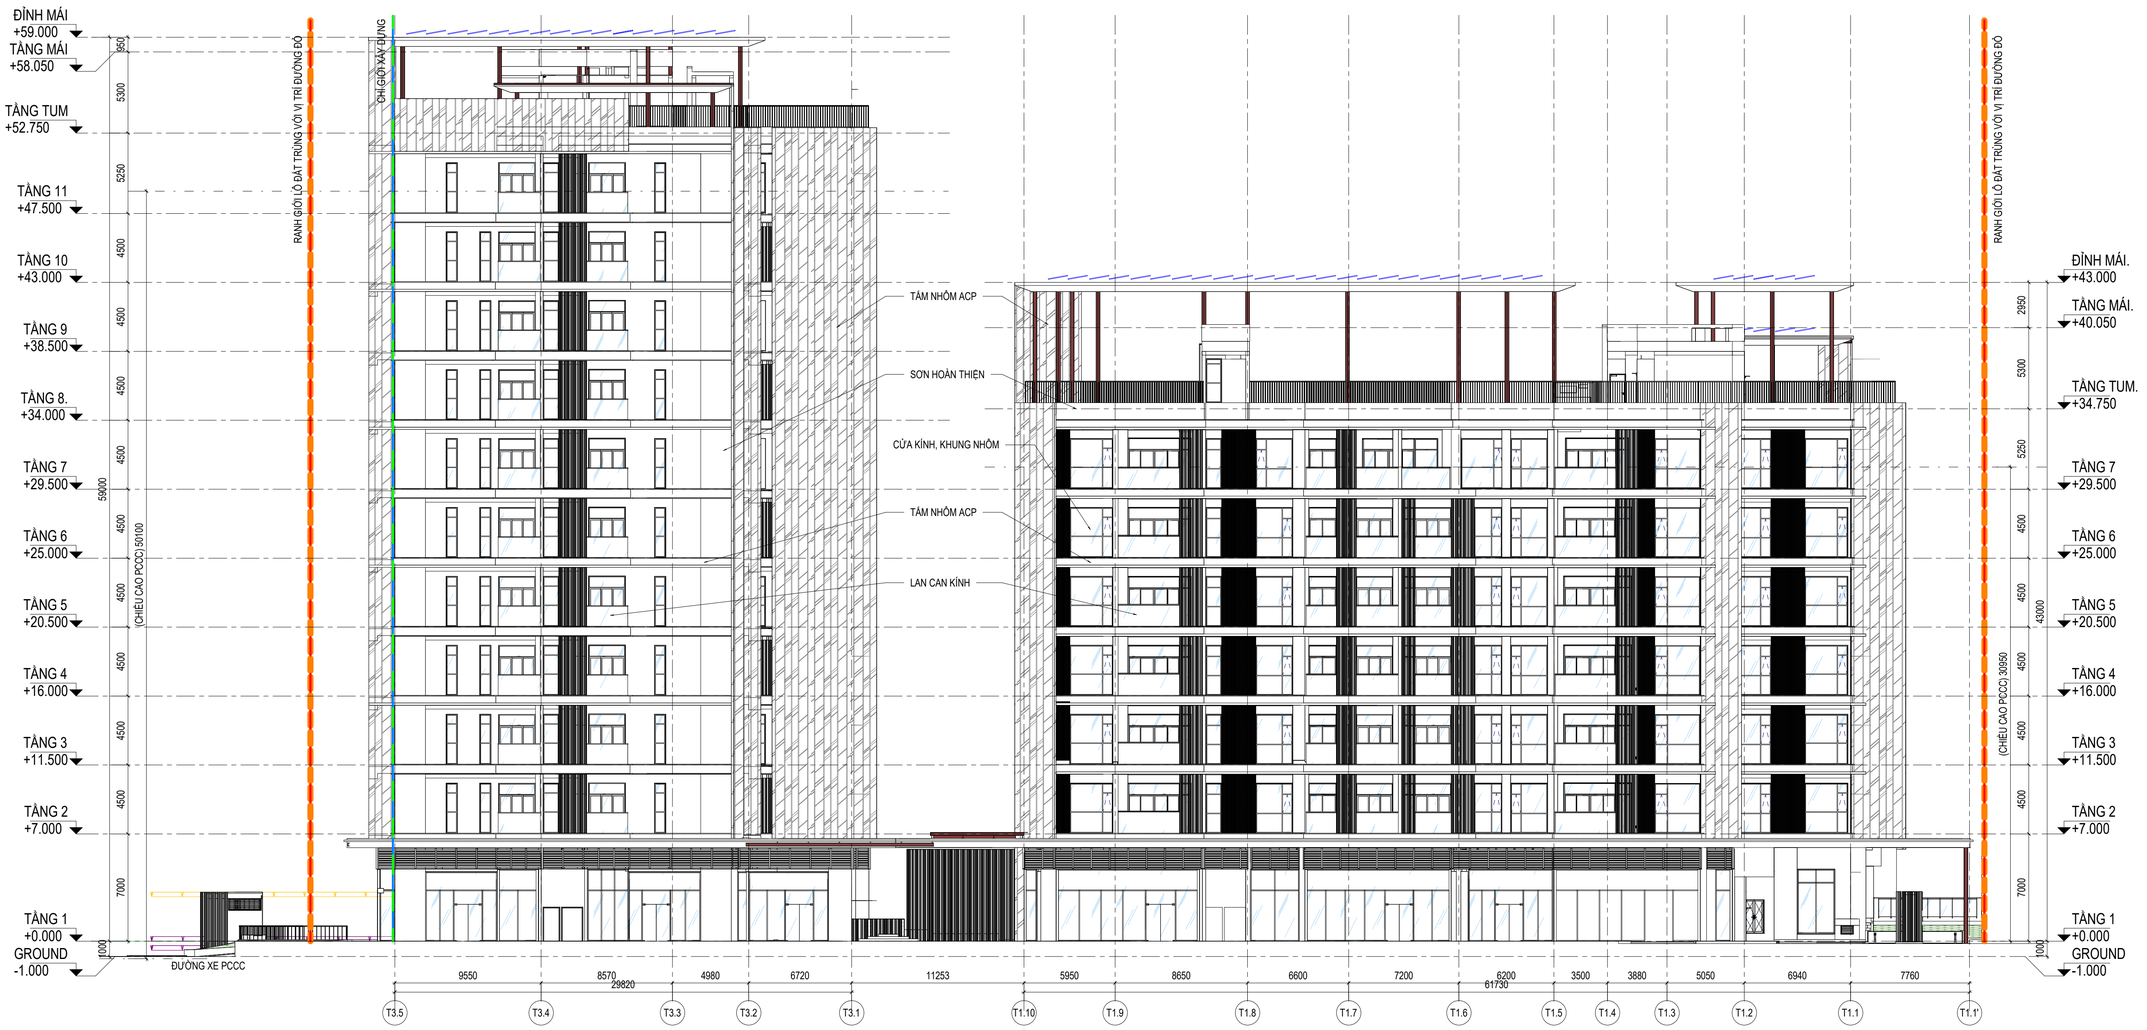

MẶT ĐỨNG CÔNG TRÌNH 1

TL: 1 : 200

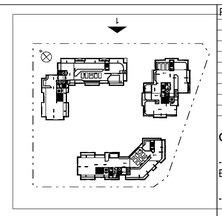

PHIÊN BẢN	NỘI DUNG ĐIỀU CHỈNH	NGÀY NỘP

GHI CHÚ:

- CỐT +0.000 LẤY TẠI SÀN HOÀN THIỆN TẦNG 1 CÔNG TRÌNH TƯƠNG ĐƯƠNG COTE TUYỆT ĐỐI +7.900 (HỆ TỌA ĐỘ VN-2000)

- TÒA 1 CHIỀU CAO CÔNG TRÌNH TÍNH TỪ:
  + COTE HOÀN THIỆN +0.000: 43M
  + COTE NỀN TỰ NHIÊN THẤP NHẤT -1.000: 44M
- TÒA 2 CHIỀU CAO CÔNG TRÌNH TÍNH TỪ:
  + COTE HOÀN THIỆN +0.000: 50M
  + COTE NỀN TỰ NHIÊN THẤP NHẤT -1.000: 51M
- TÒA 3 CHIỀU CAO CÔNG TRÌNH TÍNH TỪ:
  + COTE HOÀN THIỆN +0.000: 59M
  + COTE NỀN TỰ NHIÊN THẤP NHẤT -1.000: 60M

- KHU VỰC TMDV BÀN GIAO THÔ, VỆ SINH KHÔNG XÂY, CHỈ BỐ TRÍ LAYOUT ĐỊNH HƯỚNG ĐẶT CÁC ĐẦU CHỜ.

- TỶ LỆ SỬ DỤNG VẬT LIỆU XANH KHÔNG NUNG ĐÁP ỨNG TỚI 90% KHỐI LƯỢNG GẠCH TRONG CÔNG TRÌNH

- TRONG PHÒNG RÁC KHÔNG BỐ TRÍ CÁC CHẤT, VẬT LIỆU CÓ KHẢ NĂNG GÂY CHÁY NỔ

- TƯỜNG NGĂN CHÁY, VÁCH NGĂN CHÁY TRONG CÁC GIAN PHÒNG ĐƯỢC NGĂN CHIA ĐẾN TRẦN BÊ TÔNG.

- VẬT LIỆU HOÀN THIỆN TRẦN, TƯỜNG, SÀN TRÊN CÁC ĐƯỜNG THOÁT NẠN, TRONG SẢNH THANG MÁY, SẢNH CHUNG, TẦNG KỸ THUẬT LÀ VẬT LIỆU KHÔNG CHÁY ĐẠT CV0

- TRONG CÁC KHÔNG GIAN TRẦN TREO KHÔNG BỐ TRÍ CÁC KÊNH, ĐƯỜNG ỐNG DẪN VẬN CHUYỂN CÁC CHẤT CHÁY DẠNG KHÍ, HỖN HỢP KHÍ, CHẤT LỎNG VÀ VẬT LIỆU CHÁY.

- TRONG CÔNG TRÌNH KHÔNG BỐ TRÍ TRẦN TREO CHO CÁC GIAN PHÒNG HẠNG A VÀ HẠNG B

- KHÔNG CÓ KÊNH, GIẾNG, ĐƯỜNG ỐNG ĐI QUA TƯỜNG NGĂN CHÁY LOẠI 1

CHỦ ĐẦU TƯ / OWNER:
CÔNG TY CỔ PHẦN THƯƠNG MẠI DƯƠNG PHÚC THẮNG
DUONG PHUC THANG TRADING JOINT STOCK COMPANY

ĐỊA CHỈ / ADDRESS:
Tầng 16, Tòa OSI Tower, Khu tây Hồ Tây, Phường Xuân Đỉnh, Thành phố Hà Nội, Việt Nam.
Hotline : 0243 2077 272

TƯ VẤN KIẾN TRÚC CHÍNH / MAIN ARCHITECTURAL CONSULTANT:
CÔNG TY TNHH KIẾN TRÚC DP VIỆT NAM
DP ARCHITECTS VIETNAM CO.,LTD.

ĐỊA CHỈ / ADDRESS:
Tầng 4, số 82 Võ Văn Tần, Phường Xuân Hòa, TP.Hồ Chí Minh
Hotline : 0283 5357 507
Fax: 0283 5357 517
Email : dparchitects@dpa.com.sg

TƯ VẤN THIẾT KẾ / CONSULTANT:
CÔNG TY CỔ PHẦN INNO
INNO.,JSC

ĐỊA CHỈ / ADDRESS
HN: 39 Thượng Thụy, Phú Thượng, Hà Nội
HCM: 37 Nguyễn Văn Hưởng, An Khánh, TP. HCM
Hotline: 0243 212 1776 Email : ad@innojsc.com

TỔNG GIÁM ĐỐC / GENERAL DIRECTOR:
ĐOÀN VĂN ĐỘNG

CHỦ NHIỆM THIẾT KẾ / PROJECT MANAGER:
LƯU GIANG NAM

CHỦ TRÌ THIẾT KẾ / DESIGN MANAGER:
NGÔ NGỌC BÌNH

KIỂM / CHECKED BY:
VŨ TUẤN ANH

THIẾT KẾ / DESIGNER
LÊ THỊ THANH **NGUYỄN XUÂN HIỆN**
PHƯƠNG THỊ ÁNH TUYẾT **VŨ TIẾN DƯƠNG**

TÊN DỰ ÁN / PROJECT NAME:
XÂY DỰNG NHÀ Ở TẠI LÔ ĐẤT NO-02

ĐỊA ĐIỂM XÂY DỰNG / PROJECT ADDRESS:
LÔ ĐẤT NO-22, PHƯỜNG BỒ ĐỀ, HÀ NỘI

HẠNG MỤC / ITEM:
KIẾN TRÚC

HOÀN THÀNH / FINISHED DATE:	MÃ SỐ DỰ ÁN / PROJECT No:
TKCS	2501
HOÀN THÀNH / FINISHED DATE: 2026	PHIÊN BẢN / REVISION: 0

TÊN BẢN VẼ / SHEET NAME:
MẶT ĐỨNG 1

SỐ HIỆU BẢN VẼ / SHEET NUMBER:
A-02.101

© 2025 - INNO.,jsc

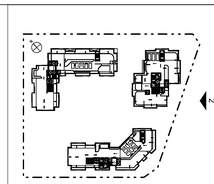

PHIÊN BẢN	NỘI DUNG ĐIỀU CHỈNH	NGÀY NỘP

GHI CHÚ:

- CỐT +0.000 LẤY TẠI SÀN HOÀN THIỆN TẦNG 1 CÔNG TRÌNH TƯƠNG ĐƯƠNG COTE TUYỆT ĐỐI +7.900 (HỆ TỌA ĐỘ VN-2000)

- TÒA 1 CHIỀU CAO CÔNG TRÌNH TÍNH TỪ:
  + COTE HOÀN THIỆN +0.000: 43M
  + COTE NỀN TỰ NHIÊN THẤP NHẤT -1.000: 44M
- TÒA 2 CHIỀU CAO CÔNG TRÌNH TÍNH TỪ:
  + COTE HOÀN THIỆN +0.000: 50M
  + COTE NỀN TỰ NHIÊN THẤP NHẤT -1.000: 51M
- TÒA 3 CHIỀU CAO CÔNG TRÌNH TÍNH TỪ:
  + COTE HOÀN THIỆN +0.000: 59M
  + COTE NỀN TỰ NHIÊN THẤP NHẤT -1.000: 60M

- KHU VỰC TMDV BÀN GIAO THÔ, VỆ SINH KHÔNG XÂY, CHỈ BỐ TRÍ LAYOUT ĐỊNH HƯỚNG ĐẶT CÁC ĐẦU CHỜ.

- TỶ LỆ SỬ DỤNG VẬT LIỆU XANH KHÔNG NUNG ĐÁP ỨNG TỐI 90% KHỐI LƯỢNG GẠCH TRONG CÔNG TRÌNH

- TRONG PHÒNG RÁC KHÔNG BỐ TRÍ CÁC CHẤT, VẬT LIỆU CÓ KHẢ NĂNG GÂY CHÁY NỔ

- TƯỜNG NGĂN CHÁY, VÁCH NGĂN CHÁY TRONG CÁC GIAN PHÒNG ĐƯỢC NGĂN CHIA BẰNG TRẦN BÊ TÔNG.

- VẬT LIỆU HOÀN THIỆN TRẦN, TƯỜNG, SÀN TRÊN CÁC ĐƯỜNG THOÁT NẠN, TRONG SẢNH THANG MÁY, SẢNH CHUNG, TẦNG KỸ THUẬT LÀ VẬT LIỆU KHÔNG CHÁY ĐẠT CV0

- TRONG CÁC KHÔNG GIAN TRẦN TREO KHÔNG BỐ TRÍ CÁC KÊNH, ĐƯỜNG ỐNG DẪN VẬN CHUYỂN CÁC CHẤT CHÁY DẠNG KHÍ, HỖN HỢP KHÍ, CHẤT LỎNG VÀ VẬT LIỆU CHÁY.

- TRONG CÔNG TRÌNH KHÔNG BỐ TRÍ TRẦN TREO CHO CÁC GIAN PHÒNG HẠNG A VÀ HẠNG B

- KHÔNG CÓ KÊNH, GIẾNG, ĐƯỜNG ỐNG ĐI QUA TƯỜNG NGĂN CHÁY LOẠI 1

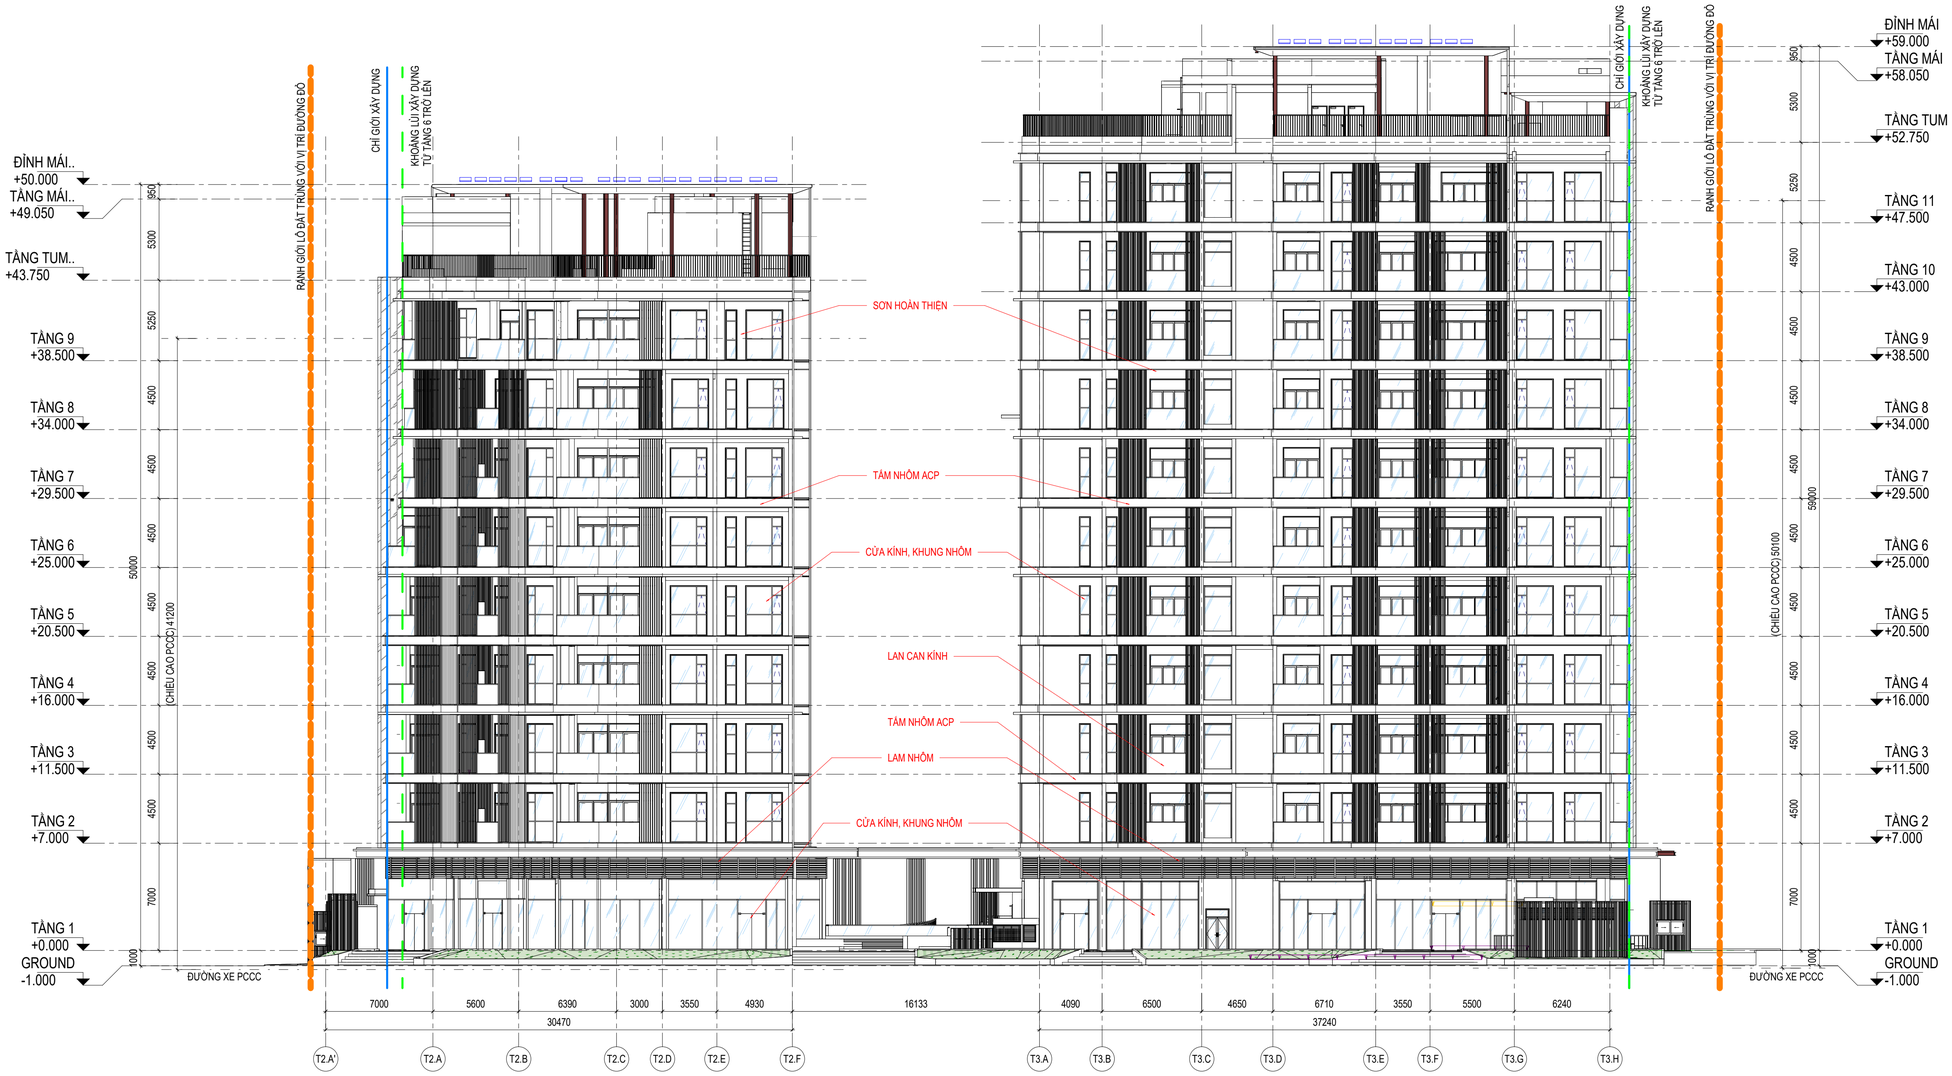

MẶT ĐỨNG CÔNG TRÌNH 2
TL: 1 : 200

CHỦ ĐẦU TƯ / OWNER:
CÔNG TY CỔ PHẦN THƯƠNG MẠI DƯƠNG PHÚC THẮNG
DUONG PHUC THANG TRADING JOINT STOCK COMPANY
ĐỊA CHỈ / ADDRESS:
Tầng 16, Tòa OSI Tower, Khu tây Hồ Tây, Phường Xuân Đỉnh, Thành phố Hà Nội, Việt Nam.
Hotline : 0243 2077 272

TƯ VẤN KIẾN TRÚC CHÍNH / MAIN ARCHITECTURAL CONSULTANT:
CÔNG TY TNHH KIẾN TRÚC DP VIỆT NAM
DP ARCHITECTS VIETNAM CO.,LTD.
ĐỊA CHỈ / ADDRESS:
Tầng 4, số 82 Võ Văn Tần, Phường Xuân Hòa, TP.Hồ Chí Minh
Hotline : 0283 5357 507
Fax: 0283 5357 517
Email : dparchitects@dpa.com.sg

TƯ VẤN THIẾT KẾ / CONSULTANT:
CÔNG TY CỔ PHẦN INNO
INNO.,JSC
ĐỊA CHỈ / ADDRESS:
HN: 39 Thượng Thụy, Phú Thượng, Hà Nội
HCM: 37 Nguyễn Văn Hưởng, An Khánh, TP. HCM
Hotline: 0243 212 1776 Email : ad@innojsc.com

TỔNG GIÁM ĐỐC / GENERAL DIRECTOR:
ĐOÀN VĂN ĐỘNG
CHỦ NHIỆM THIẾT KẾ / PROJECT MANAGER:
LƯU GIANG NAM
CHỦ TRÌ THIẾT KẾ / DESIGN MANAGER:
NGÔ NGỌC BÌNH
KIỂM / CHECKED BY:
VŨ TUẤN ANH
THIẾT KẾ / DESIGNER
LÊ THỊ THANH **NGUYỄN XUÂN HIỆN**
PHƯƠNG THỊ ÁNH TUYẾT **VŨ TIẾN DƯƠNG**

TÊN DỰ ÁN / PROJECT NAME:
XÂY DỰNG NHÀ Ở TẠI LÔ ĐẤT NO-02

ĐỊA ĐIỂM XÂY DỰNG / PROJECT ADDRESS:
LÔ ĐẤT NO-22, PHƯỜNG BỒ ĐỀ, HÀ NỘI

HẠNG MỤC / ITEM:
KIẾN TRÚC

HOÀN THÀNH / FINISHED DATE:	MÃ SỐ DỰ ÁN / PROJECT No:
TKCS	2501
HOÀN THÀNH / FINISHED DATE: 2026	PHIÊN BẢN / REVISION: **0**

TÊN BẢN VẼ / SHEET NAME:
MẶT ĐỨNG 2

SỐ HIỆU BẢN VẼ / SHEET NUMBER:
A-02.102

© 2025 - INNO.,jsc

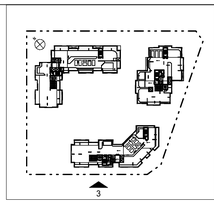

PHIÊN BẢN	NỘI DUNG ĐIỀU CHỈNH	NGÀY NỘP

GHI CHÚ:

- CỐT +0.000 LẤY TẠI SÀN HOÀN THIỆN TẦNG 1 CÔNG TRÌNH TƯƠNG ĐƯƠNG COTE TUYỆT ĐỐI +7.900 (HỆ TỌA ĐỘ VN-2000)

- TÒA 1 CHIỀU CAO CÔNG TRÌNH TÍNH TỪ:
  + COTE HOÀN THIỆN +0.000: 43M
  + COTE NỀN TỰ NHIÊN THẤP NHẤT -1.000: 44M
- TÒA 2 CHIỀU CAO CÔNG TRÌNH TÍNH TỪ:
  + COTE HOÀN THIỆN +0.000: 50M
  + COTE NỀN TỰ NHIÊN THẤP NHẤT -1.000: 51M
- TÒA 3 CHIỀU CAO CÔNG TRÌNH TÍNH TỪ:
  + COTE HOÀN THIỆN +0.000: 59M
  + COTE NỀN TỰ NHIÊN THẤP NHẤT -1.000: 60M

- KHU VỰC TMDV BÀN GIAO THÔ, VỆ SINH KHÔNG XÂY, CHỈ BỐ TRÍ LAYOUT ĐỊNH HƯỚNG ĐẶT CÁC ĐẦU CHỜ.

- TỶ LỆ SỬ DỤNG VẬT LIỆU XANH KHÔNG NUNG ĐÁP ỨNG TỐI 90% KHỐI LƯỢNG GẠCH TRONG CÔNG TRÌNH

- TRONG PHÒNG RÁC KHÔNG BỐ TRÍ CÁC CHẤT, VẬT LIỆU CÓ KHẢ NĂNG GÂY CHÁY NỔ

- TƯỜNG NGĂN CHÁY, VÁCH NGĂN CHÁY TRONG CÁC GIAN PHÒNG ĐƯỢC NGĂN CHIA ĐẾN TRẦN BÊ TÔNG.

- VẬT LIỆU HOÀN THIỆN TRẦN, TƯỜNG, SÀN TRÊN CÁC ĐƯỜNG THOÁT NẠN, TRONG SẢNH THANG MÁY, SẢNH CHUNG, TẦNG KỸ THUẬT LÀ VẬT LIỆU KHÔNG CHÁY ĐẠT CV0

- TRONG CÁC KHÔNG GIAN TRẦN TREO KHÔNG BỐ TRÍ CÁC KÊNH, ĐƯỜNG ỐNG DẪN VẬN CHUYỂN CÁC CHẤT CHÁY DẠNG KHÍ, HỖN HỢP KHÍ, CHẤT LỎNG VÀ VẬT LIỆU CHÁY.

- TRONG CÔNG TRÌNH KHÔNG BỐ TRÍ TRẦN TREO CHO CÁC GIAN PHÒNG HẠNG A VÀ HẠNG B

- KHÔNG CÓ KÊNH, GIẾNG, ĐƯỜNG ỐNG ĐI QUA TƯỜNG NGĂN CHÁY LOẠI 1

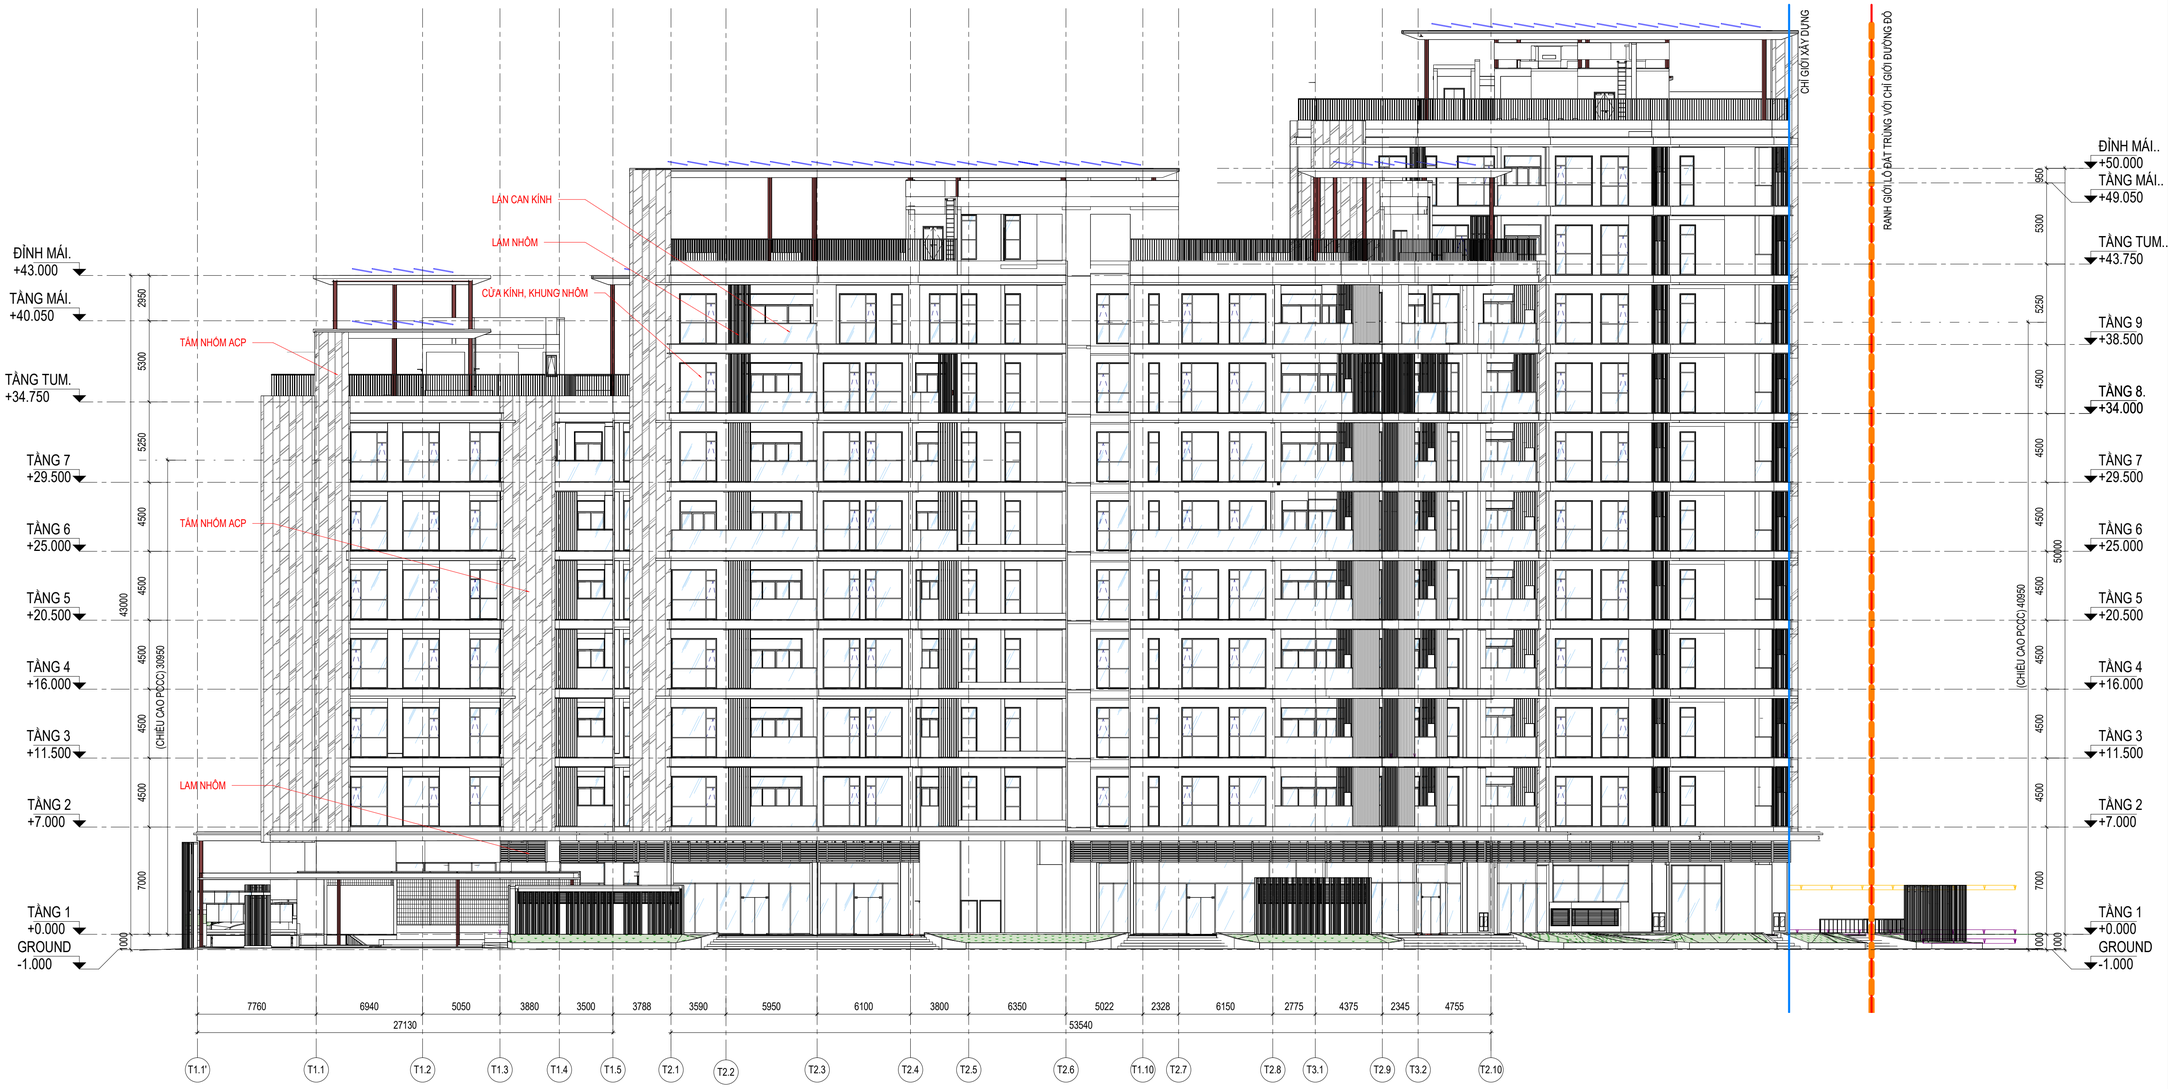

MẶT ĐỨNG CÔNG TRÌNH 3
TL: 1 : 200

CHỦ ĐẦU TƯ / OWNER:
CÔNG TY CỔ PHẦN THƯƠNG MẠI DƯƠNG PHÚC THẮNG
DUONG PHUC THANG TRADING JOINT STOCK COMPANY
ĐỊA CHỈ / ADDRESS:
Tầng 16, Tòa Odi Tower, Khu tây Hồ Tây, Phường Xuân Đỉnh, Thành phố Hà Nội, Việt Nam.
Hotline : 0243 2077 272

TƯ VẤN KIẾN TRÚC CHÍNH / MAIN ARCHITECTURAL CONSULTANT:
CÔNG TY TNHH KIẾN TRÚC DP VIỆT NAM
DP ARCHITECTS VIETNAM CO.,LTD.
ĐỊA CHỈ / ADDRESS:
Tầng 4, số 82 Võ Văn Tần, Phường Xuân Hòa, TP.Hồ Chí Minh
Hotline : 0283 5357 507
Fax: 0283 5357 517
Email : dparchitects@dpa.com.sg

TƯ VẤN THIẾT KẾ / CONSULTANT:
CÔNG TY CỔ PHẦN INNO
INNO.,JSC
ĐỊA CHỈ / ADDRESS
HN: 39 Thượng Thụy, Phú Thượng, Hà Nội
HCM: 37 Nguyễn Văn Hưởng, An Khánh, TP. HCM
Hotline: 0243 212 1776 Email : ad@innojsc.com

TỔNG GIÁM ĐỐC / GENERAL DIRECTOR:
ĐOÀN VĂN ĐỘNG
CHỦ NHIỆM THIẾT KẾ / PROJECT MANAGER:
LƯU GIANG NAM
CHỦ TRÌ THIẾT KẾ / DESIGN MANAGER:
NGÔ NGỌC BÌNH
KIỂM / CHECKED BY:
VŨ TUẤN ANH
THIẾT KẾ / DESIGNER
LÊ THỊ THANH **NGUYỄN XUÂN HIỆN**
PHƯƠNG THỊ ÁNH TUYẾT **VŨ TIẾN DƯƠNG**

TÊN DỰ ÁN / PROJECT NAME:
XÂY DỰNG NHÀ Ở TẠI LÔ ĐẤT NO-02

ĐỊA ĐIỂM XÂY DỰNG / PROJECT ADDRESS:
LÔ ĐẤT NO-22, PHƯỜNG BỒ ĐỀ, HÀ NỘI

HẠNG MỤC / ITEM:
KIẾN TRÚC

HOÀN THÀNH / FINISHED DATE:	MÃ SỐ DỰ ÁN / PROJECT No:
TKCS	2501
HOÀN THÀNH / FINISHED DATE: 2026	PHIÊN BẢN / REVISION: 0

TÊN BẢN VẼ / SHEET NAME:
MẶT ĐỨNG 3

SỐ HIỆU BẢN VẼ / SHEET NUMBER:
A-02.103

© 2025 - INNO.,jsc

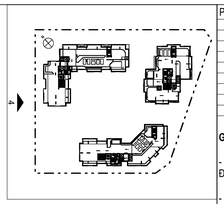

PHIÊN BẢN	NỘI DUNG ĐIỀU CHỈNH	NGÀY NỘP

GHI CHÚ:

- CỐT +0.000 LẤY TẠI SÀN HOÀN THIỆN TẦNG 1 CÔNG TRÌNH TƯƠNG ĐƯƠNG COTE TUYỆT ĐỐI +7.900 (HỆ TỌA ĐỘ VN-2000)

- TÒA 1 CHIỀU CAO CÔNG TRÌNH TÍNH TỪ:
  + COTE HOÀN THIỆN +0.000: 43M
  + COTE NỀN TỰ NHIÊN THẤP NHẤT -1.000: 44M
- TÒA 2 CHIỀU CAO CÔNG TRÌNH TÍNH TỪ:
  + COTE HOÀN THIỆN +0.000: 50M
  + COTE NỀN TỰ NHIÊN THẤP NHẤT -1.000: 51M
- TÒA 3 CHIỀU CAO CÔNG TRÌNH TÍNH TỪ:
  + COTE HOÀN THIỆN +0.000: 59M
  + COTE NỀN TỰ NHIÊN THẤP NHẤT -1.000: 60M

- KHU VỰC TMDV BÀN GIAO THÔ, VỆ SINH KHÔNG XÂY, CHỈ BỐ TRÍ LAYOUT ĐỊNH HƯỚNG ĐẶT CÁC ĐẦU CHỜ.

- TỶ LỆ SỬ DỤNG VẬT LIỆU XANH KHÔNG NUNG ĐÁP ỨNG TỚI 90% KHỐI LƯỢNG GẠCH TRONG CÔNG TRÌNH

- TRONG PHÒNG RÁC KHÔNG BỐ TRÍ CÁC CHẤT, VẬT LIỆU CÓ KHẢ NĂNG GÂY CHÁY NỔ

- TƯỜNG NGĂN CHÁY, VÁCH NGĂN CHÁY TRONG CÁC GIAN PHÒNG ĐƯỢC NGĂN CHIA ĐẾN TRẦN BÊ TÔNG.

- VẬT LIỆU HOÀN THIỆN TRẦN, TƯỜNG, SÀN TRÊN CÁC ĐƯỜNG THOÁT NẠN, TRONG SẢNH THANG MÁY, SẢNH CHUNG, TẦNG KỸ THUẬT LÀ VẬT LIỆU KHÔNG CHÁY ĐẠT CV0

- TRONG CÁC KHÔNG GIAN TRẦN TREO KHÔNG BỐ TRÍ CÁC KÊNH, ĐƯỜNG ỐNG DẪN VẬN CHUYỂN CÁC CHẤT CHÁY DẠNG KHÍ, HỖN HỢP KHÍ, CHẤT LỎNG VÀ VẬT LIỆU CHÁY.

- TRONG CÔNG TRÌNH KHÔNG BỐ TRÍ TRẦN TREO CHO CÁC GIAN PHÒNG HẠNG A VÀ HẠNG B

- KHÔNG CÓ KÊNH, GIẾNG, ĐƯỜNG ỐNG ĐI QUA TƯỜNG NGĂN CHÁY LOẠI 1

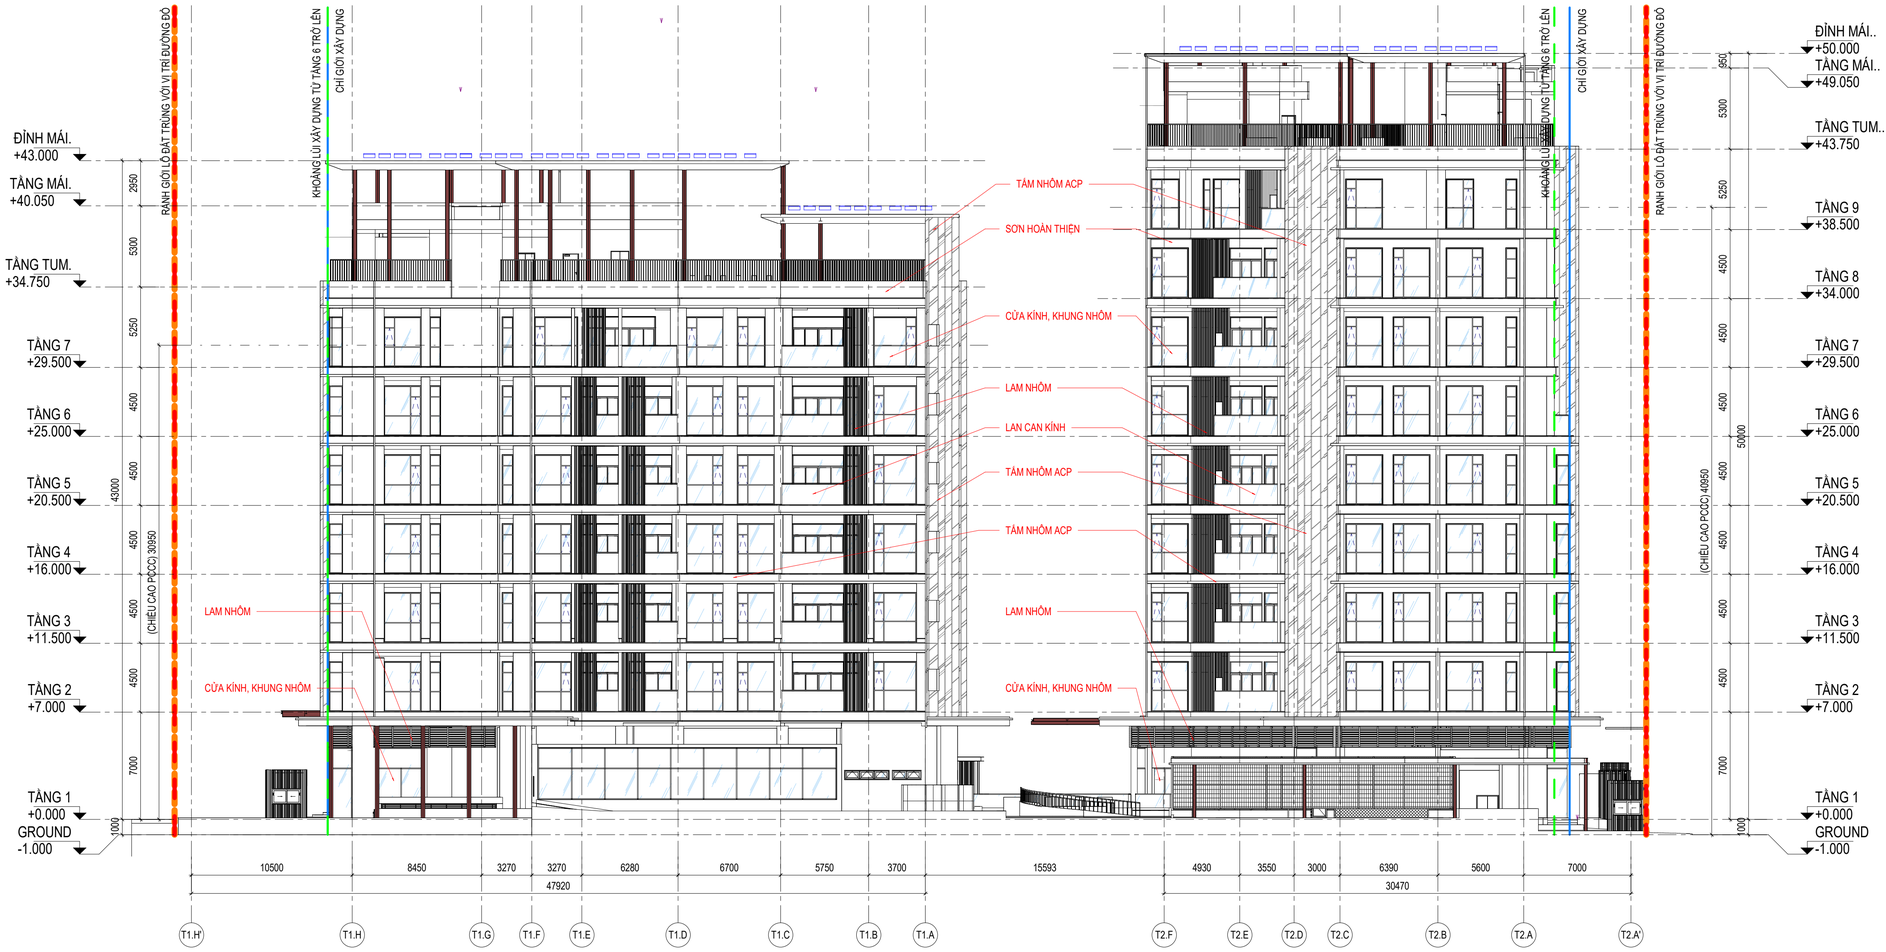

MẶT ĐỨNG CÔNG TRÌNH 4
TL: 1 : 200

CHỦ ĐẦU TƯ / OWNER:
CÔNG TY CỔ PHẦN THƯƠNG MẠI DƯƠNG PHÚC THẮNG
DUONG PHUC THANG TRADING JOINT STOCK COMPANY
ĐỊA CHỈ / ADDRESS:
Tầng 16, Tòa OSI Tower, Khu tây Hồ Tây, Phường Xuân Đỉnh, Thành phố Hà Nội, Việt Nam.
Hotline : 0243 2077 272

TƯ VẤN KIẾN TRÚC CHÍNH / MAIN ARCHITECTURAL CONSULTANT:
CÔNG TY TNHH KIẾN TRÚC DP VIỆT NAM
DP ARCHITECTS VIETNAM CO.,LTD.
ĐỊA CHỈ / ADDRESS:
Tầng 4, số 82 Võ Văn Tần, Phường Xuân Hòa, TP.Hồ Chí Minh
Hotline : 0283 5357 507
Fax: 0283 5357 517
Email : dparchitects@dpa.com.sg

TƯ VẤN THIẾT KẾ / CONSULTANT:
CÔNG TY CỔ PHẦN INNO
INNO.,JSC
ĐỊA CHỈ / ADDRESS:
HN: 39 Thượng Thụy, Phú Thượng, Hà Nội
HCM: 37 Nguyễn Văn Hưởng, An Khánh, TP. HCM
Hotline: 0243 212 1776 Email : ad@innojsc.com

TỔNG GIÁM ĐỐC / GENERAL DIRECTOR:
ĐOÀN VĂN ĐỘNG
CHỦ NHIỆM THIẾT KẾ / PROJECT MANAGER:
LƯU GIANG NAM
CHỦ TRÌ THIẾT KẾ / DESIGN MANAGER:
NGÔ NGỌC BÌNH
KIỂM / CHECKED BY:
VŨ TUẤN ANH
THIẾT KẾ / DESIGNER
LÊ THỊ THANH **NGUYỄN XUÂN HIỆN**
PHƯƠNG THỊ ÁNH TUYẾT **VŨ TIẾN DƯƠNG**

TÊN DỰ ÁN / PROJECT NAME:
XÂY DỰNG NHÀ Ở TẠI LÔ ĐẤT NO-02

ĐỊA ĐIỂM XÂY DỰNG / PROJECT ADDRESS:
LÔ ĐẤT NO-22, PHƯỜNG BỒ ĐỀ, HÀ NỘI

HẠNG MỤC / ITEM:
KIẾN TRÚC

HOÀN THÀNH / FINISHED DATE:	MÃ SỐ DỰ ÁN / PROJECT No:
TKCS	2501
HOÀN THÀNH / FINISHED DATE: 2026	PHIÊN BẢN / REVISION: 0

TÊN BẢN VẼ / SHEET NAME:
MẶT ĐỨNG 4

SỐ HIỆU BẢN VẼ / SHEET NUMBER:
A-02.104

© 2025 - INNO.,jsc

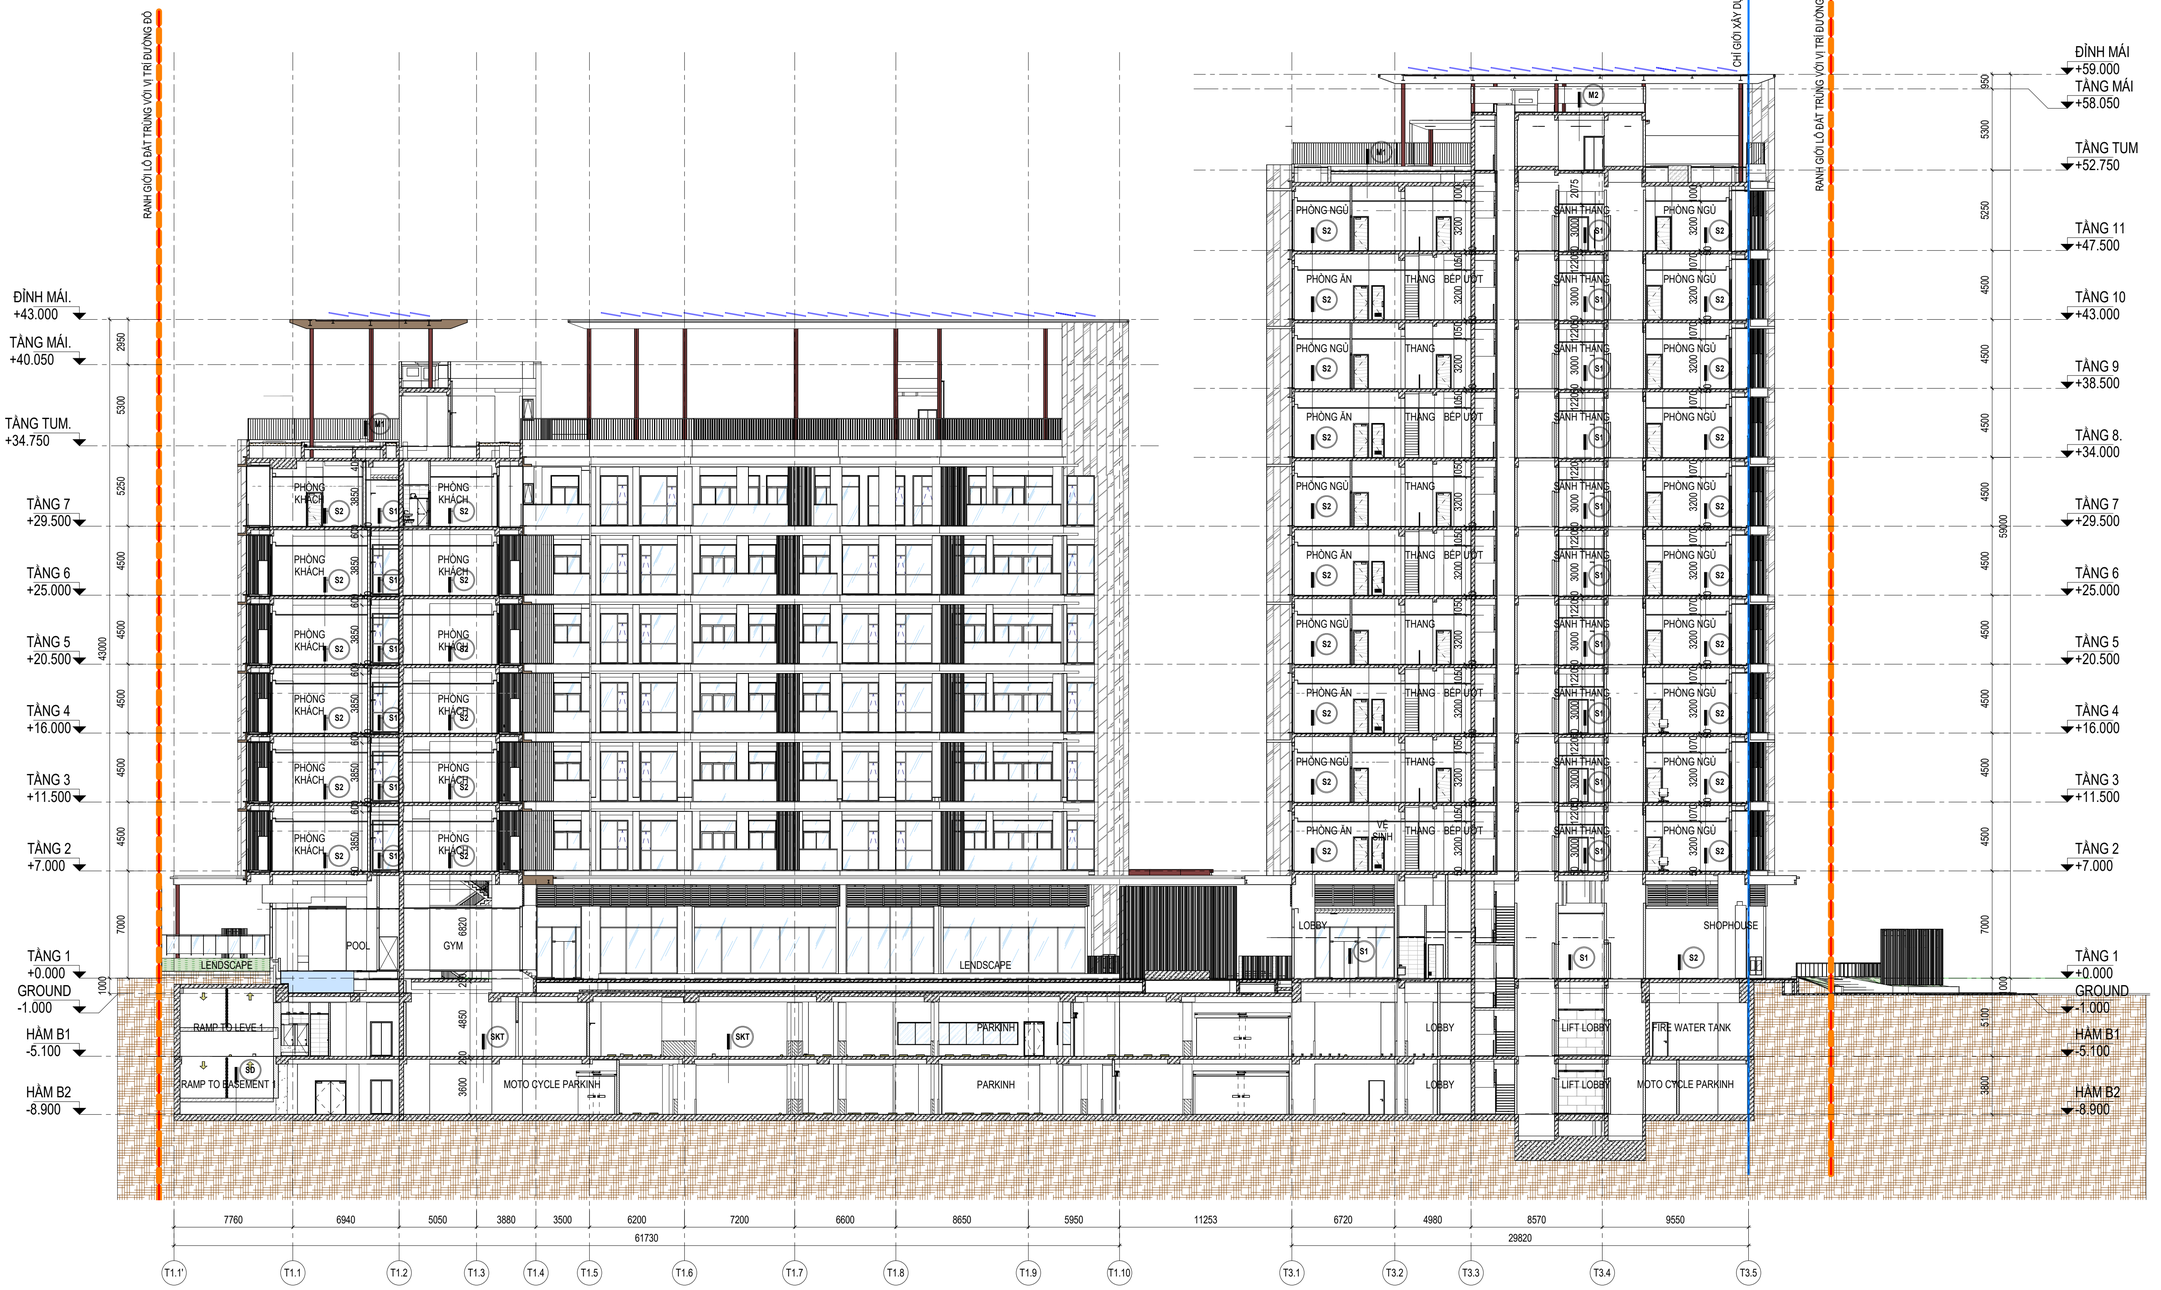

MẶT CẮT A-A
TL: 1 : 200

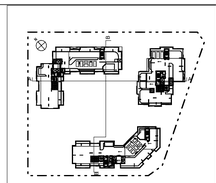

PHIÊN BẢN	NỘI DUNG ĐIỀU CHỈNH	NGÀY NỘP

GHI CHÚ:

- CỐT +0.000 LẤY TẠI SÀN HOÀN THIỆN TẦNG 1 CÔNG TRÌNH TƯƠNG ĐƯƠNG COTE TUYỆT ĐỐI +7.900 (HỆ TỌA ĐỘ VN-2000)

- TÒA 1 CHIỀU CAO CÔNG TRÌNH TÍNH TỪ:
  + COTE HOÀN THIỆN +0.000: 43M
  + COTE NỀN TỰ NHIÊN THẤP NHẤT -1.000: 44M
- TÒA 2 CHIỀU CAO CÔNG TRÌNH TÍNH TỪ:
  + COTE HOÀN THIỆN +0.000: 50M
  + COTE NỀN TỰ NHIÊN THẤP NHẤT -1.000: 51M
- TÒA 3 CHIỀU CAO CÔNG TRÌNH TÍNH TỪ:
  + COTE HOÀN THIỆN +0.000: 59M
  + COTE NỀN TỰ NHIÊN THẤP NHẤT -1.000: 60M

- KHU VỰC TMDV BÀN GIAO THÔ, VỆ SINH KHÔNG XÂY, CHỈ BỐ TRÍ LAYOUT ĐỊNH HƯỚNG ĐẶT CÁC ĐẦU CHỜ.

- TỶ LỆ SỬ DỤNG VẬT LIỆU XANH KHÔNG NUNG ĐÁP ỨNG TỚI 90% KHỐI LƯỢNG GẠCH TRONG CÔNG TRÌNH

- TRONG PHÒNG RÁC KHÔNG BỐ TRÍ CÁC CHẤT, VẬT LIỆU CÓ KHẢ NĂNG GÂY CHÁY NỔ

- TƯỜNG NGĂN CHÁY, VÁCH NGĂN CHÁY TRONG CÁC GIAN PHÒNG ĐƯỢC NGĂN CHIA ĐẾN TRẦN BÊ TÔNG.

- VẬT LIỆU HOÀN THIỆN TRẦN, TƯỜNG, SÀN TRÊN CÁC ĐƯỜNG THOÁT NẠN, TRONG SẢNH THANG MÁY, SẢNH CHUNG, TẦNG KỸ THUẬT LÀ VẬT LIỆU KHÔNG CHÁY ĐẠT CV0

- TRONG CÁC KHÔNG GIAN TRẦN TREO KHÔNG BỐ TRÍ CÁC KÊNH, ĐƯỜNG ỐNG DẪN VẬN CHUYỂN CÁC CHẤT CHÁY DẠNG KHÍ, HỖN HỢP KHÍ, CHẤT LỎNG VÀ VẬT LIỆU CHÁY.

- TRONG CÔNG TRÌNH KHÔNG BỐ TRÍ TRẦN TREO CHO CÁC GIAN PHÒNG HẠNG A VÀ HẠNG B

- KHÔNG CÓ KÊNH, GIẾNG, ĐƯỜNG ỐNG ĐI QUA TƯỜNG NGĂN CHÁY LOẠI 1

CHỦ ĐẦU TƯ / OWNER:
CÔNG TY CỔ PHẦN THƯƠNG MẠI DƯƠNG PHÚC THẮNG
DUONG PHUC THANG TRADING JOINT STOCK COMPANY
ĐỊA CHỈ / ADDRESS:
Tầng 16, Tòa OSI Tower, Khu tây Hồ Tây, Phường Xuân Đỉnh, Thành phố Hà Nội, Việt Nam.
Hotline : 0243 2077 272

TƯ VẤN KIẾN TRÚC CHÍNH / MAIN ARCHITECTURAL CONSULTANT:
CÔNG TY TNHH KIẾN TRÚC DP VIỆT NAM
DP ARCHITECTS VIETNAM CO.,LTD.
ĐỊA CHỈ / ADDRESS:
Tầng 4, số 82 Võ Văn Tần, Phường Xuân Hòa, TP.Hồ Chí Minh
Hotline : 0283 5357 507
Fax: 0283 5357 517
Email : dparchitects@dpa.com.sg

TƯ VẤN THIẾT KẾ / CONSULTANT:
CÔNG TY CỔ PHẦN INNO
INNO.,JSC
ĐỊA CHỈ / ADDRESS
HN: 39 Thượng Thụy, Phú Thượng, Hà Nội
HCM: 37 Nguyễn Văn Hưởng, An Khánh, TP. HCM
Hotline: 0243 212 1776 Email : ad@innojsc.com

TỔNG GIÁM ĐỐC / GENERAL DIRECTOR:
ĐOÀN VĂN ĐỘNG
CHỦ NHIỆM THIẾT KẾ / PROJECT MANAGER:
LƯU GIANG NAM
CHỦ TRÌ THIẾT KẾ / DESIGN MANAGER:
NGÔ NGỌC BÌNH
KIỂM / CHECKED BY:
VŨ TUẤN ANH
THIẾT KẾ / DESIGNER
LÊ THỊ THANH **NGUYỄN XUÂN HIỆN**
PHƯƠNG THỊ ÁNH TUYẾT **VŨ TIẾN DƯƠNG**

TÊN DỰ ÁN / PROJECT NAME:
XÂY DỰNG NHÀ Ở TẠI LÔ ĐẤT NO-02

ĐỊA ĐIỂM XÂY DỰNG / PROJECT ADDRESS:
LÔ ĐẤT NO-22, PHƯỜNG BỒ ĐỀ, HÀ NỘI

HẠNG MỤC / ITEM:
KIẾN TRÚC

HOÀN THÀNH / FINISHED DATE:	MÃ SỐ DỰ ÁN / PROJECT No:
TKCS	2501
HOÀN THÀNH / FINISHED DATE: 2026	PHIÊN BẢN / REVISION: 0

TÊN BẢN VẼ / SHEET NAME:
MẶT CẮT A-A

SỐ HIỆU BẢN VẼ / SHEET NUMBER:
A-03.101

© 2025 - INNO.,JSC

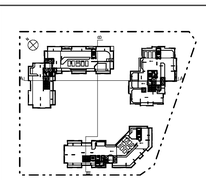

PHIÊN BẢN	NỘI DUNG ĐIỀU CHỈNH	NGÀY NỘP

GHI CHÚ:

- CỐT +0.000 LẤY TẠI SÀN HOÀN THIỆN TẦNG 1 CÔNG TRÌNH TƯƠNG ĐƯƠNG COTE TUYỆT ĐỐI +7.900 (HỆ TỌA ĐỘ VN-2000)

- TÒA 1 CHIỀU CAO CÔNG TRÌNH TÍNH TỪ:
  + COTE HOÀN THIỆN +0.000: 43M
  + COTE NỀN TỰ NHIÊN THẤP NHẤT -1.000: 44M
- TÒA 2 CHIỀU CAO CÔNG TRÌNH TÍNH TỪ:
  + COTE HOÀN THIỆN +0.000: 50M
  + COTE NỀN TỰ NHIÊN THẤP NHẤT -1.000: 51M
- TÒA 3 CHIỀU CAO CÔNG TRÌNH TÍNH TỪ:
  + COTE HOÀN THIỆN +0.000: 59M
  + COTE NỀN TỰ NHIÊN THẤP NHẤT -1.000: 60M

- KHU VỰC TMDV BÀN GIAO THÔ, VỆ SINH KHÔNG XÂY, CHỈ BỐ TRÍ LAYOUT ĐỊNH HƯỚNG ĐẶT CÁC ĐẦU CHỜ.

- TỶ LỆ SỬ DỤNG VẬT LIỆU XANH KHÔNG NUNG ĐÁP ỨNG TỐI 90% KHỐI LƯỢNG GẠCH TRONG CÔNG TRÌNH

- TRONG PHÒNG RÁC KHÔNG BỐ TRÍ CÁC CHẤT, VẬT LIỆU CÓ KHẢ NĂNG GÂY CHÁY NỔ

- TƯỜNG NGĂN CHÁY, VÁCH NGĂN CHÁY TRONG CÁC GIAN PHÒNG ĐƯỢC NGĂN CHIA ĐẾN TRẦN BÊ TÔNG.

- VẬT LIỆU HOÀN THIỆN TRẦN, TƯỜNG, SÀN TRÊN CÁC ĐƯỜNG THOÁT NẠN, TRONG SẢNH THANG MÁY, SẢNH CHUNG, TẦNG KỸ THUẬT LÀ VẬT LIỆU KHÔNG CHÁY ĐẠT CV0

- TRONG CÁC KHÔNG GIAN TRẦN TREO KHÔNG BỐ TRÍ CÁC KÊNH, ĐƯỜNG ỐNG DẪN VẬN CHUYỂN CÁC CHẤT CHÁY DẠNG KHÍ, HỖN HỢP KHÍ, CHẤT LỎNG VÀ VẬT LIỆU CHÁY.

- TRONG CÔNG TRÌNH KHÔNG BỐ TRÍ TRẦN TREO CHO CÁC GIAN PHÒNG HẠNG A VÀ HẠNG B

- KHÔNG CÓ KÊNH, GIẾNG, ĐƯỜNG ỐNG ĐI QUA TƯỜNG NGĂN CHÁY LOẠI 1

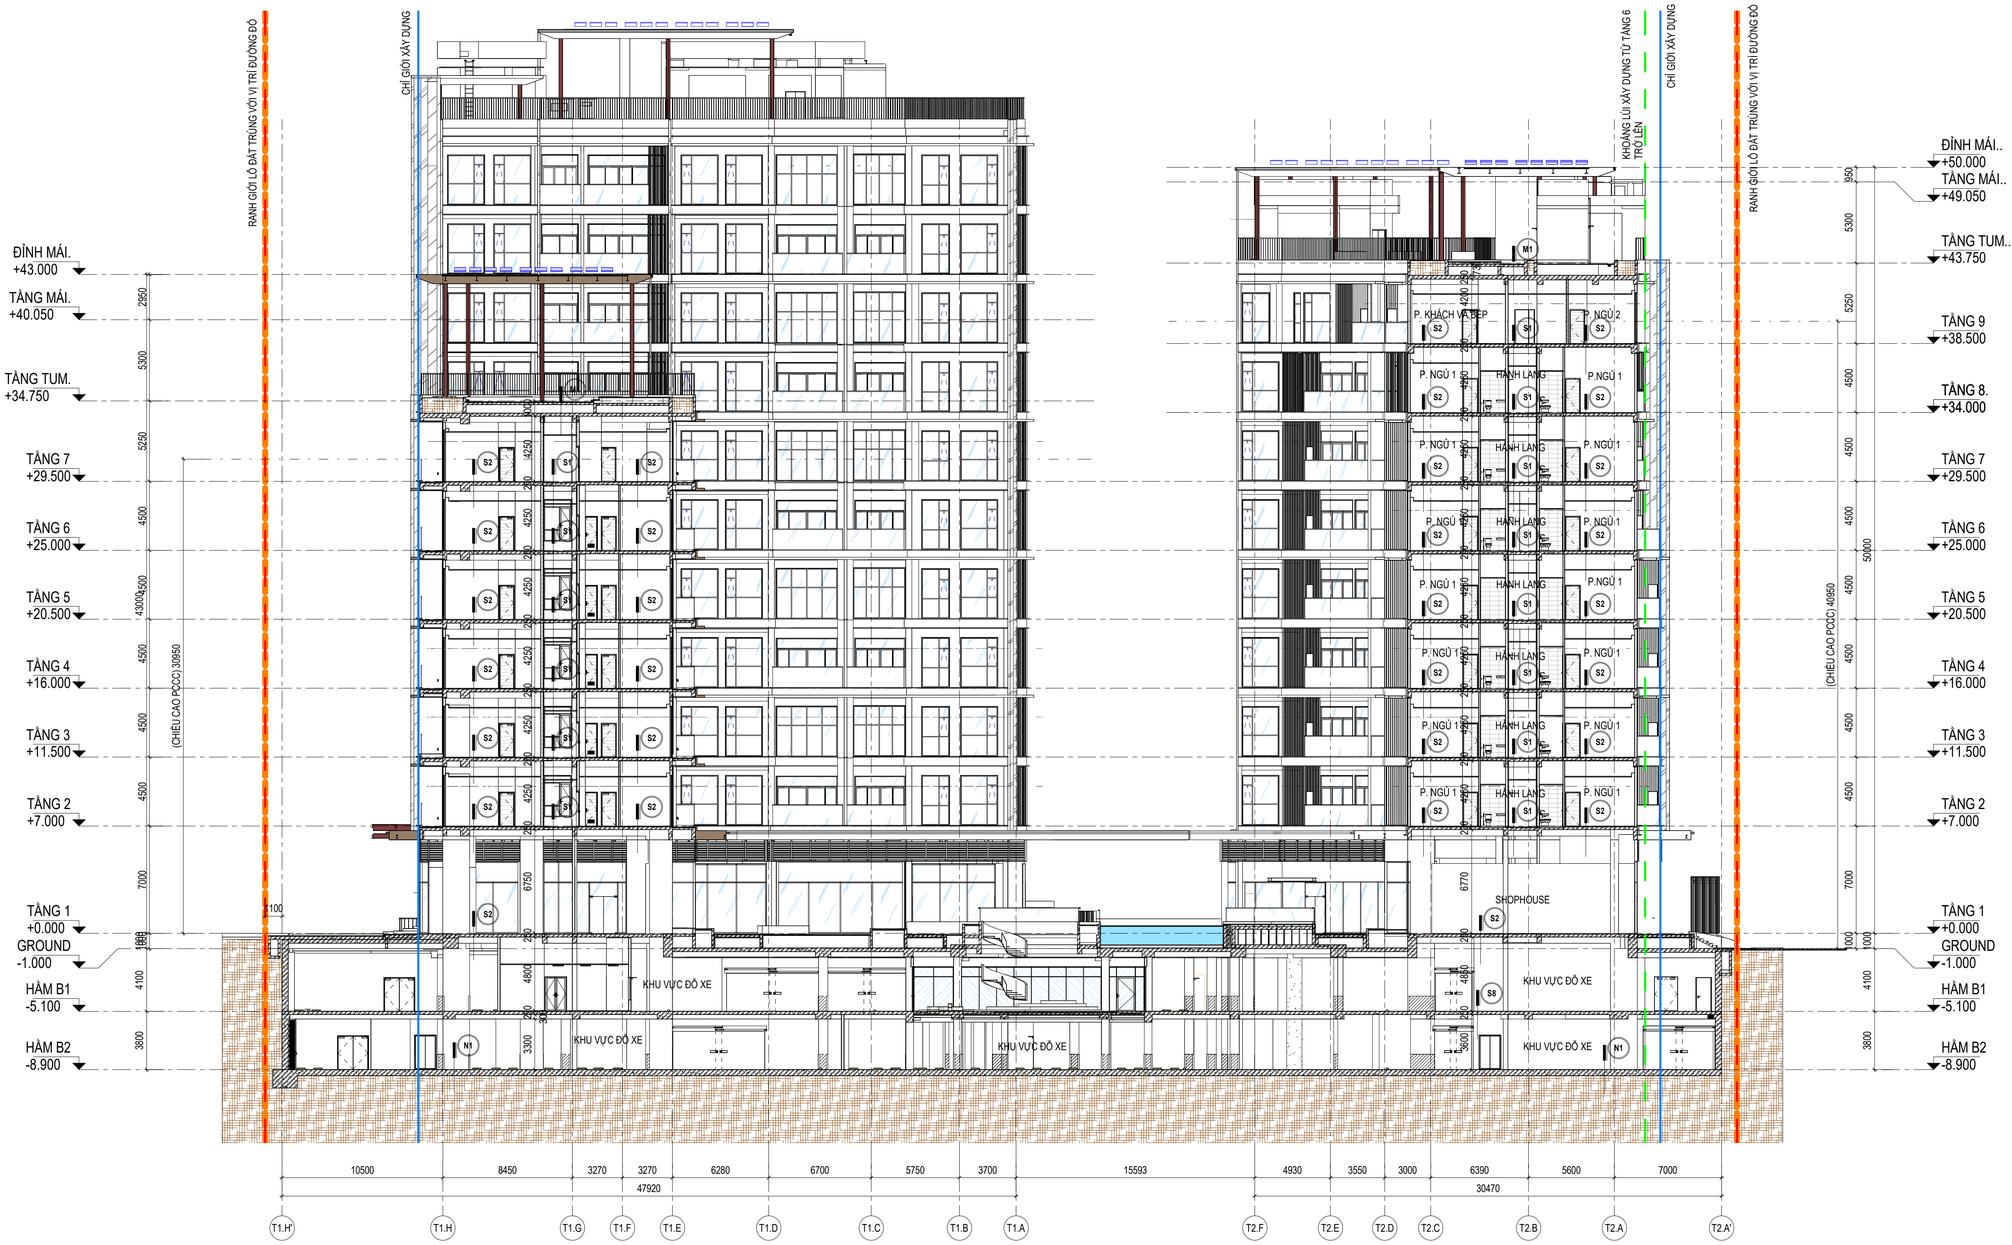

MẶT CẮT B-B
TL: 1 : 200

CHỦ ĐẦU TƯ / OWNER:
CÔNG TY CỔ PHẦN THƯƠNG MẠI DƯƠNG PHÚC THẮNG
DUONG PHUC THANG TRADING JOINT STOCK COMPANY
ĐỊA CHỈ / ADDRESS:
Tầng 18, Tòa Diễn Tower, Khu tây Hồ Tây, Phường Xuân Đỉnh, Thành phố Hà Nội, Việt Nam.
Hotline : 0243 2077 272

TƯ VẤN KIẾN TRÚC CHÍNH / MAIN ARCHITECTURAL CONSULTANT:
CÔNG TY TNHH KIẾN TRÚC DP VIỆT NAM
DP ARCHITECTS VIETNAM CO.,LTD.
ĐỊA CHỈ / ADDRESS:
Tầng 4, số 82 Võ Văn Tần, Phường Xuân Hòa, TP.Hồ Chí Minh
Hotline : 0283 5357 507
Fax: 0283 5357 517
Email : dparchitects@dpa.com.sg

TƯ VẤN THIẾT KẾ / CONSULTANT:
CÔNG TY CỔ PHẦN INNO
INNO.,JSC
ĐỊA CHỈ / ADDRESS:
HN: 39 Thượng Thụy, Phú Thượng, Hà Nội
HCM: 37 Nguyễn Văn Hưởng, An Khánh, TP. HCM
Hotline: 0243 212 1776 Email : ad@innojsc.com

TỔNG GIÁM ĐỐC / GENERAL DIRECTOR:
ĐOÀN VĂN ĐỘNG
CHỦ NHIỆM THIẾT KẾ / PROJECT MANAGER:
LƯU GIANG NAM
CHỦ TRÌ THIẾT KẾ / DESIGN MANAGER:
NGÔ NGỌC BÌNH
KIỂM / CHECKED BY:
VŨ TUẤN ANH
THIẾT KẾ / DESIGNER
LÊ THỊ THANH **NGUYỄN XUÂN HIỆN**
PHƯƠNG THỊ ÁNH TUYẾT **VŨ TIẾN DƯƠNG**

TÊN DỰ ÁN / PROJECT NAME:
XÂY DỰNG NHÀ Ở TẠI LÔ ĐẤT NO-02

ĐỊA ĐIỂM XÂY DỰNG / PROJECT ADDRESS:
LÔ ĐẤT NO-22, PHƯỜNG BỒ ĐỀ, HÀ NỘI

HẠNG MỤC / ITEM:
KIẾN TRÚC

HOÀN THÀNH / FINISHED DATE:	MÃ SỐ DỰ ÁN / PROJECT No:
TKCS	2501
HOÀN THÀNH / FINISHED DATE: 2026	PHIÊN BẢN / REVISION: 0

TÊN BẢN VẼ / SHEET NAME:
MẶT CẮT B-B

SỐ HIỆU BẢN VẼ / SHEET NUMBER:
A-03.102

© 2025 - INNO.,jsc